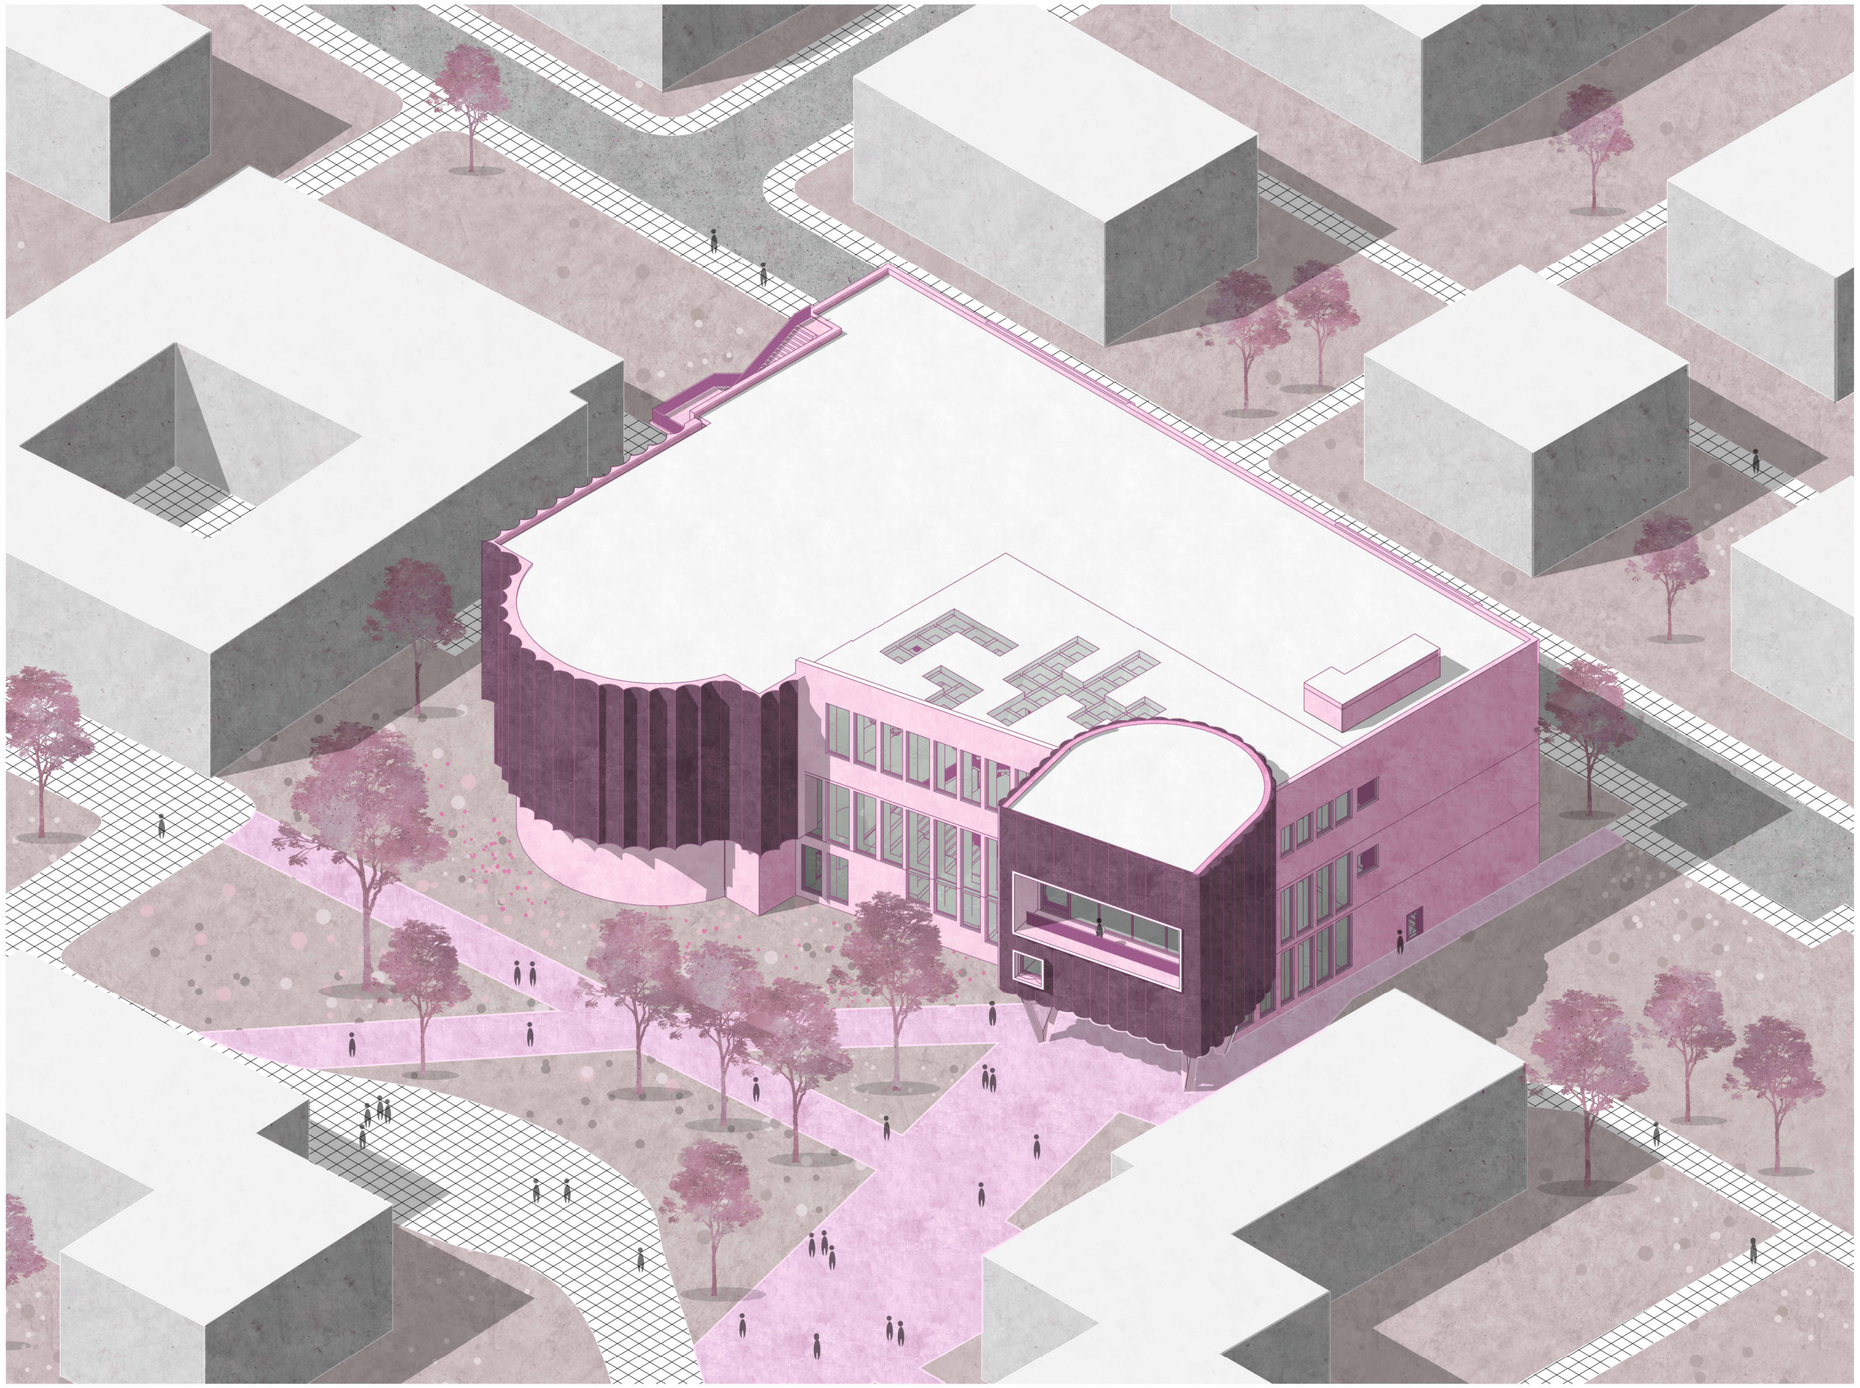

Creative Center at York St John University / Tate + Co

Автор курса: Дарья Климчук
Куратор: Дарья Климчук
Выполнила: Тамила Трубицина

Изм.	Кол.уч.	Лист	№док.	Подп.	Дата	АР		
Разработал						Титул	Стадия	Лист	Листов
Проверил							П	00	

Формат А2А

Согласовано

Согласовано

Взам. инв. №

Подп. и дата

Инв. № подл.

Ведомость рабочих чертежей основного комплекта

Лист	Наименование	Примечание
01	Общие данные	
02	Кладочный план 1-го этажа на отм. 0,000	
03	Кладочный план 2-го этажа на отм.	
04	План эргономики 1 этажа на отм. +0.000	
05	План отделки стен на отм. +0.000	
06	План напольных покрытий на отм. +0.000	
07	План размещения сантехнического оборудования на отм. +0.000	
08	План размещения осветительного оборудования на отм. +0.000	
09	План маркировки дверных проемов на отм. +0.000	
10	Развертки стен и аксонометрия актового зала	
11	Взрыв схемы, Аксонометрия	
12	Фасад-1, Разрез 9-3	
13	Фасады-2,3,4	
14	3d-разрезы, Вид-1	
15	Виды-2,3,4	

Согласовано

Согласовано

Взам. инв. №

Подп. и дата

Инв. № подл.

Изм.	Кол.уч.	Лист	№док.	Подп.	Дата	АР		
						Общие данные	Стадия	Лист	Листов
							П	01	

Формат А2А

Кладочный план на отм. +0,000 М 1:200

Экспликация помещений 1-го этажа

Номер	Наименование	Площадь	Примечание
1	Актовый зал	370,53	
2	Главный холл	390,86	
3	Тамбур	8,85	
4	Тамбур	10,37	
5	Тамбур	18,08	
6	Тамбур	9,95	
7	Тамбур	8,53	
8	Тамбур	16,00	
9	Тамбур	12,27	
10	Тамбур	4,79	
11	Тех. помещение	4,29	
12	Кабинет	33,70	
13	Кабинет	50,55	
14	Студия рисунка	140,94	
15	Тех. помещение	11,60	
16	С/у	5,16	
17	С/у	2,71	
18	Тех. помещение	30,55	
19	Склад	10,67	
20	С/у	14,32	
21	Склад	5,90	
22	Кухня	105,01	
23	Кабинет	46,24	
24	Класс компьютеров	78,85	
25	Лестница	28,07	
26	Тамбур	11,04	
27	Тех. помещение	3,56	
28	Тамбур	35,25	
29	Кабинет	124,97	
Общий итог		1593,60	

Условные обозначения

1 — Номер помещения

+ 0,000 — Высотная отметка чистого пола

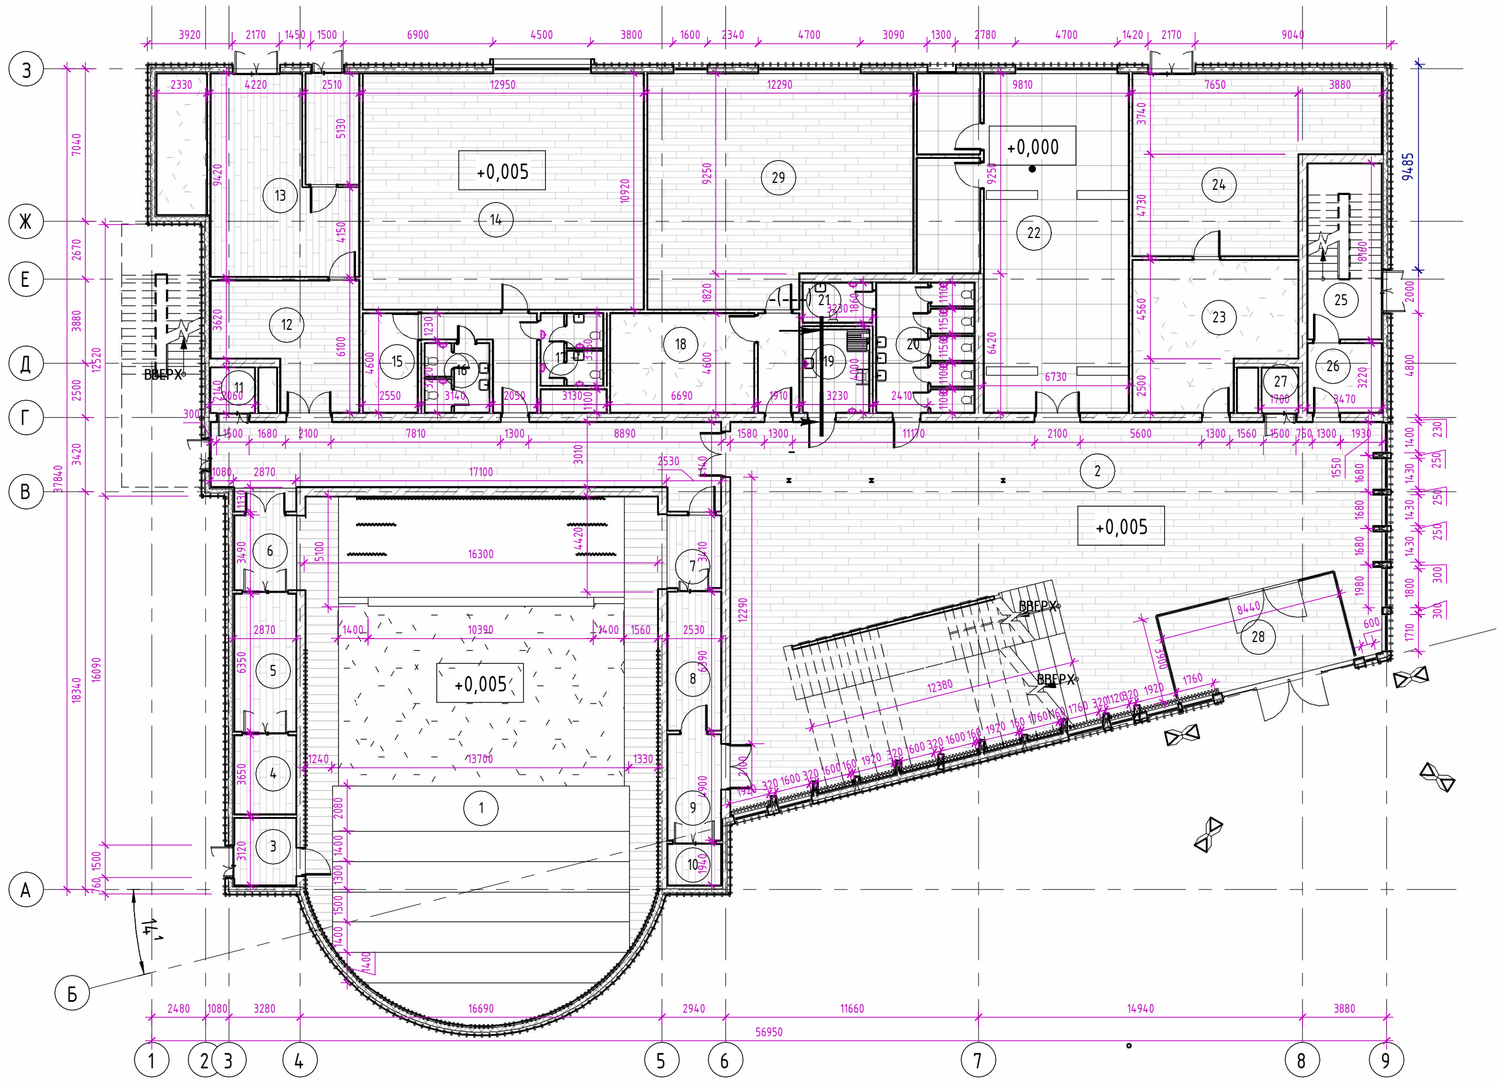

Согласовано

Согласовано

Взам. инв. №

Подп. и дата

Инв. № подл.

Изм.	Кол.уч.	Лист	№док.	Подп.	Дата	АР		
Разработал						Кладочный план 1-го этажа на отм. 0,000	Стадия	Лист	Листов
Проверил							П	02	

Формат А2А

План эргономики 1 этажа на отм. +0.000

Экспликация помещений 1-го этажа

Номер	Наименование	Площадь	Примечание
1	Актовый зал	370,53	
2	Главный холл	390,86	
3	Тамбур	8,85	
4	Тамбур	10,37	
5	Тамбур	18,08	
6	Тамбур	9,95	
7	Тамбур	8,53	
8	Тамбур	16,00	
9	Тамбур	12,27	
10	Тамбур	4,79	
11	Тех. помещение	4,29	
12	Кабинет	33,70	
13	Кабинет	50,55	
14	Студия рисунка	140,94	
15	Тех. помещение	11,60	
16	С/у	5,16	
17	С/у	2,71	
18	Тех. помещение	30,55	
19	Склад	10,67	
20	С/у	14,32	
21	Склад	5,90	
22	Кухня	105,01	
23	Кабинет	46,24	
24	Класс компьютеров	78,85	
25	Лестница	28,07	
26	Тамбур	11,04	
27	Тех. помещение	3,56	
28	Тамбур	35,25	
29	Кабинет	124,97	
Общий итог		1593,60	

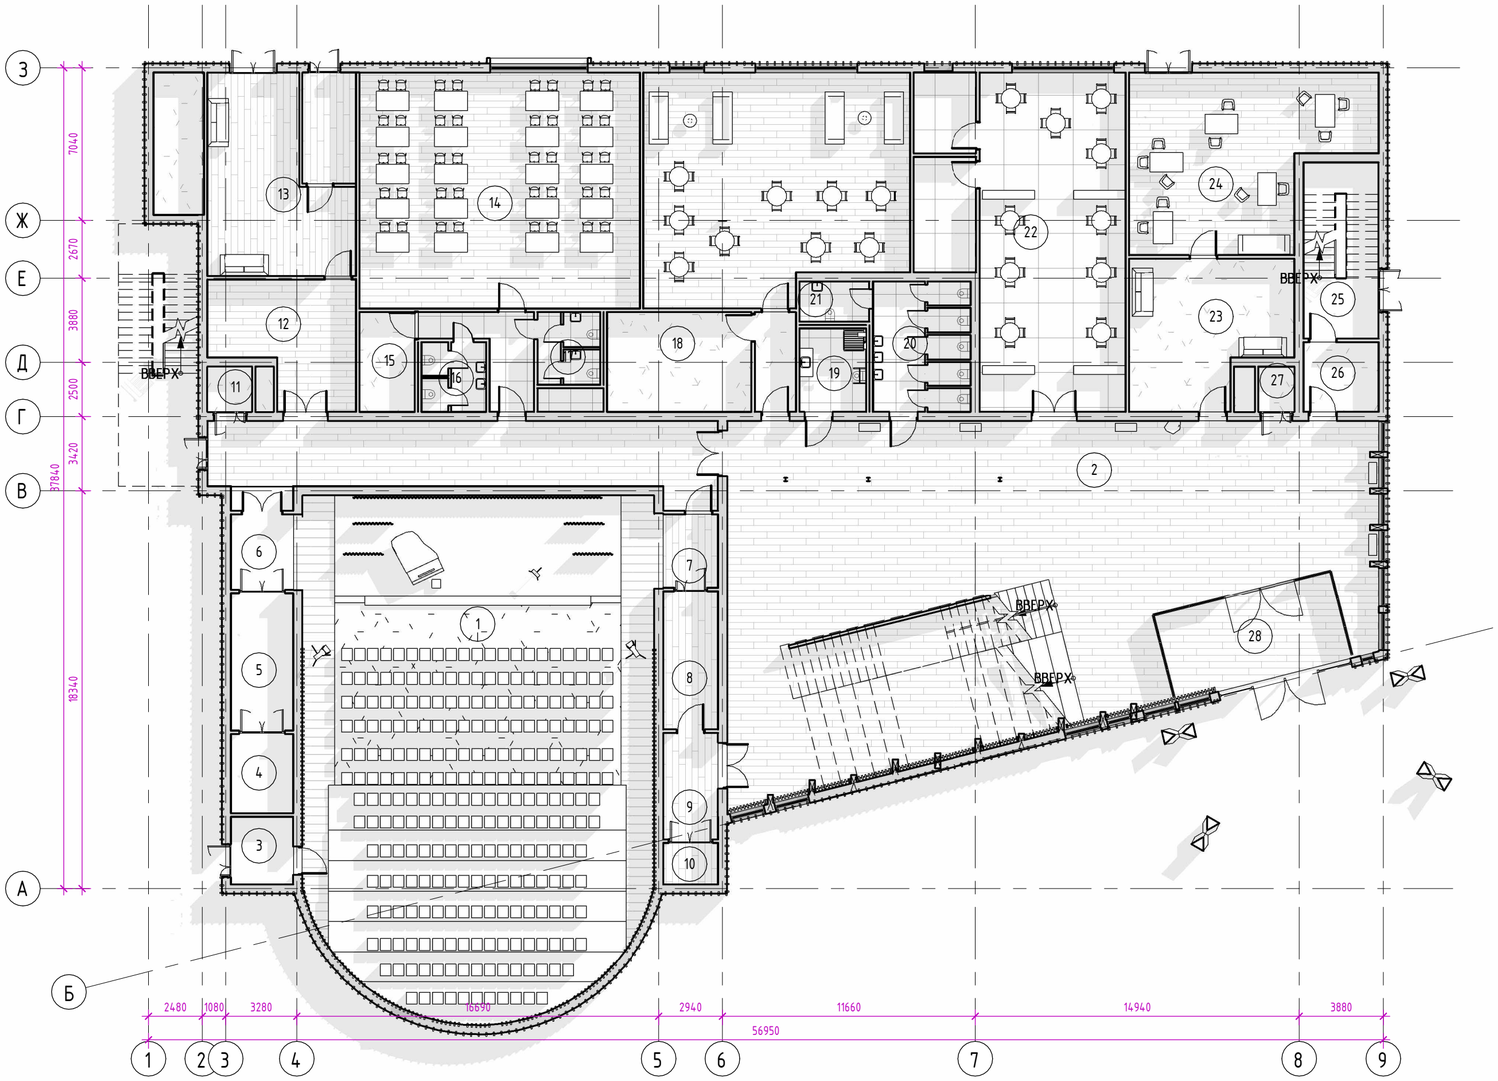

План зонирования

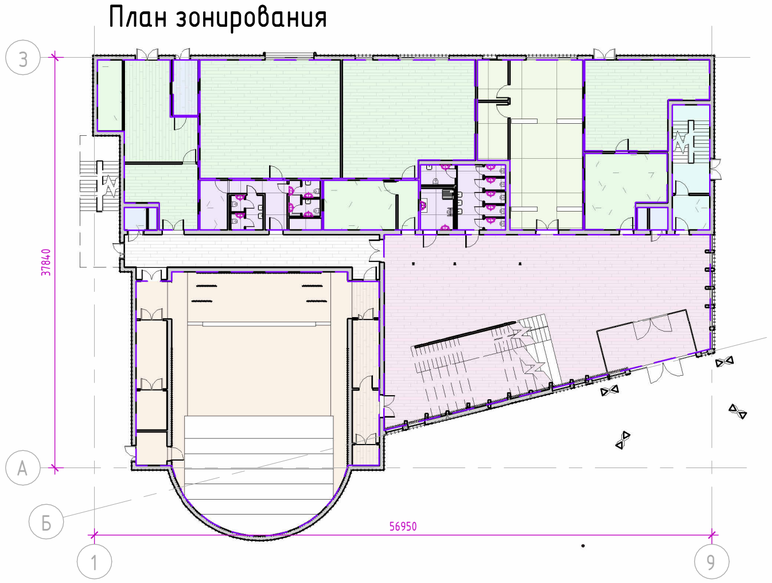

Легенда зонирования

- Зона актового зала
- Зона главного холла
- Зона лестничной площадки
- Зона пищевого блока
- Зона с/у
- Зона тех. помещений
- Зона учебных помещений

Согласовано

Согласовано

Взам. инв. №

Подп. и дата

Инв. № подл.

Изм.	Кол.уч.	Лист	№док.	Подп.	Дата	АР		
Разработал						План эргономики 1 этажа на отм. +0.000	Стадия	Лист	Листов
Проверил							П	04	

Формат А2А

План отделки стен на отм. +0,000 М 1:200

Экспликация помещений 1-го этажа			
Номер	Наименование	Площадь	Примечание
1	Актовый зал	370,53	
2	Главный холл	390,86	
3	Тамбур	8,85	
4	Тамбур	10,37	
5	Тамбур	18,08	
6	Тамбур	9,95	
7	Тамбур	8,53	
8	Тамбур	16,00	
9	Тамбур	12,27	
10	Тамбур	4,79	
11	Тех. помещение	4,29	
12	Кабинет	33,70	
13	Кабинет	50,55	
14	Студия рисунка	140,94	
15	Тех. помещение	11,60	
16	С/у	5,16	
17	С/у	2,71	
18	Тех. помещение	30,55	
19	Склад	10,67	
20	С/у	14,32	
21	Склад	5,90	
22	Кухня	105,01	
23	Кабинет	46,24	
24	Класс компьютеров	78,85	
25	Лестница	28,07	
26	Тамбур	11,04	
27	Тех. помещение	3,56	
28	Тамбур	35,25	
29	Кабинет	124,97	
Общий итог		1593,60	

Условные обозначения

1 — Номер помещения

От-1 — Отделка стен

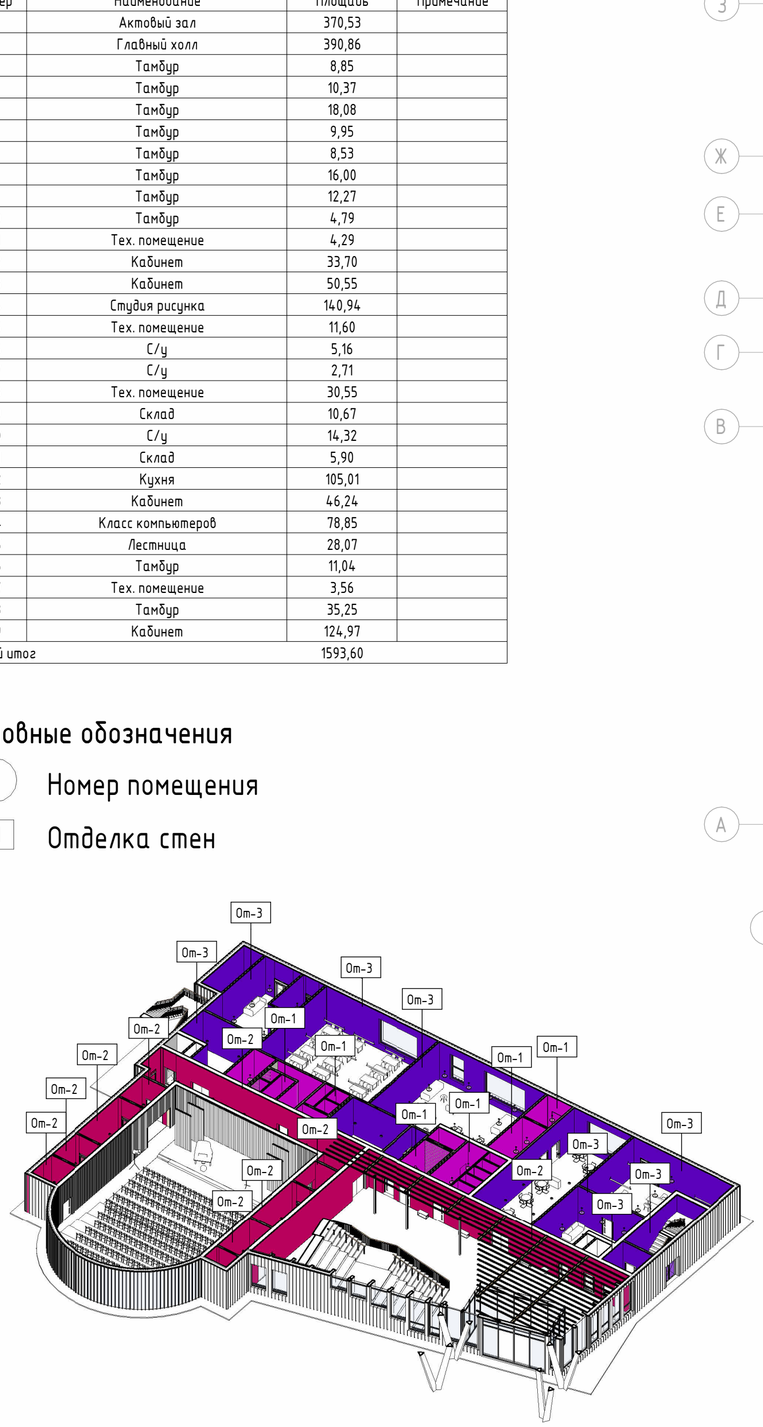

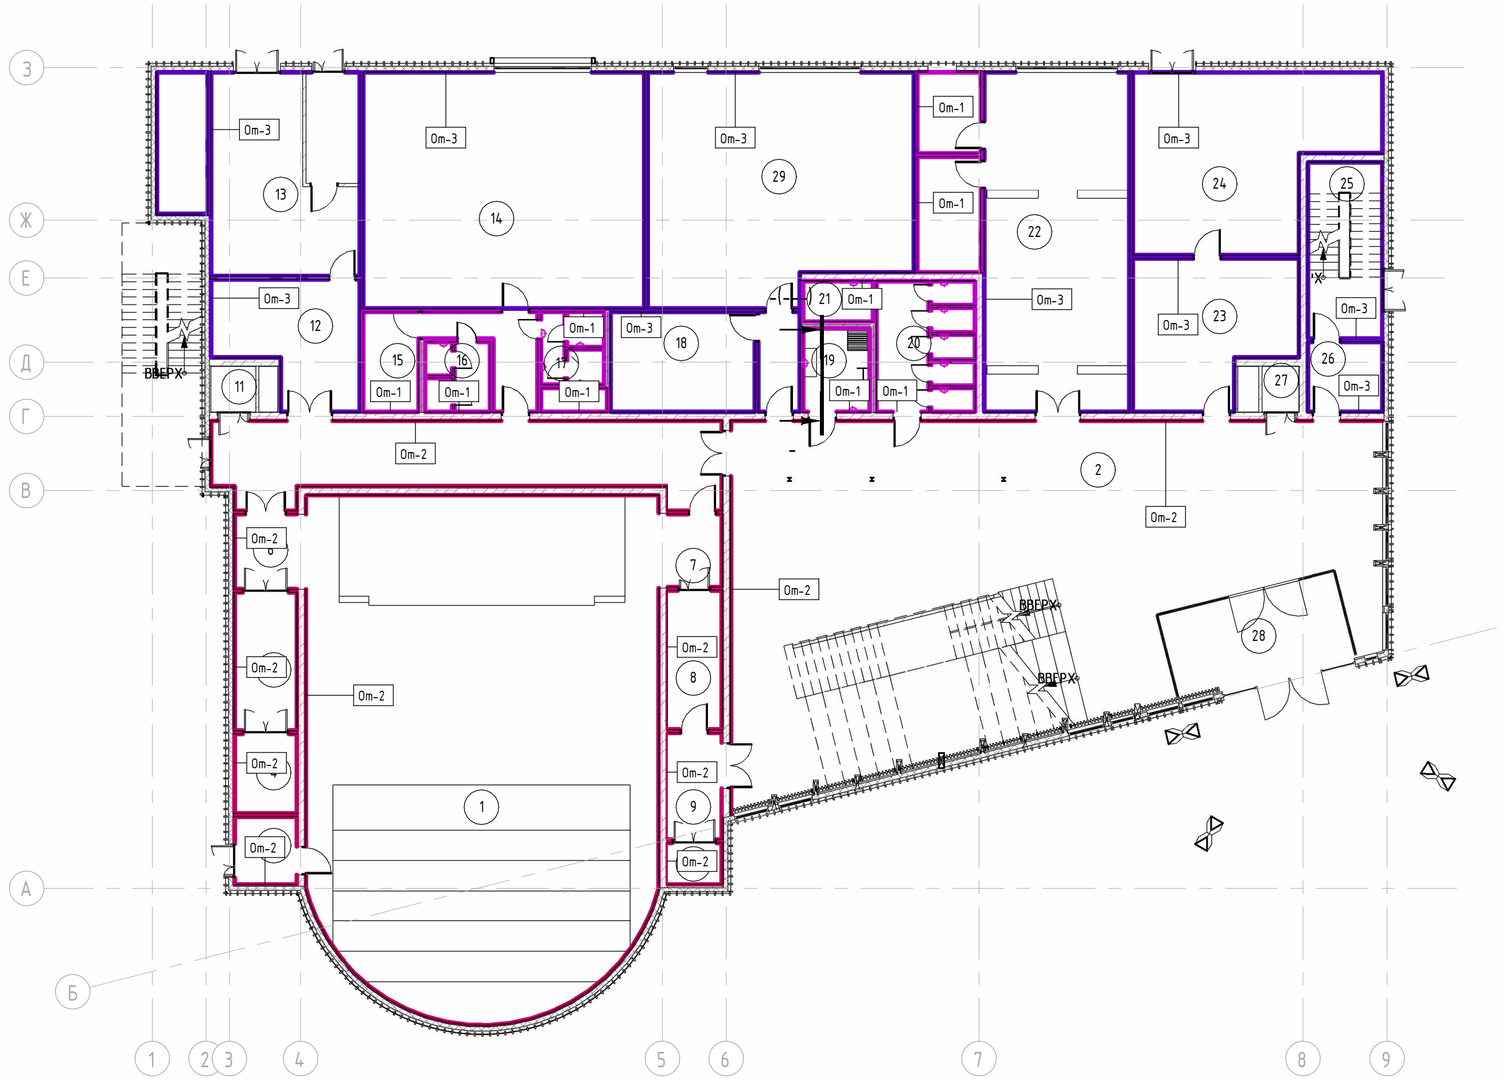

Спецификация отделки стен 1-го этажа				
Марка	УО	Описание	S,м2	Примечание
От-1		Плитка керамическая 250*250	871,33	
От-2		Вагонка, Хвоя штиль10мм	1232,49	
От-3		Штукатурка белая 10мм	1664,46	

Изм.	Кол.уч.	Лист	№док.	Подп.	Дата	АР			
Разработал						План отделки стен на отм. +0.000	Стадия	Лист	Листов
Проверил							П	05	

Формат А2А

Согласовано

Согласовано

Взам. инв. №

Подп. и дата

Инв. № подл.

План напольных покрытий на отм. +0,000 М 1:200

Экспликация помещений 1-го этажа			
Номер	Наименование	Площадь	Примечание
1	Актовый зал	370,53	
2	Главный холл	390,86	
3	Тамбур	8,85	
4	Тамбур	10,37	
5	Тамбур	18,08	
6	Тамбур	9,95	
7	Тамбур	8,53	
8	Тамбур	16,00	
9	Тамбур	12,27	
10	Тамбур	4,79	
11	Тех. помещение	4,29	
12	Кабинет	33,70	
13	Кабинет	50,55	
14	Студия рисунка	140,94	
15	Тех. помещение	11,60	
16	С/у	5,16	
17	С/у	2,71	
18	Тех. помещение	30,55	
19	Склад	10,67	
20	С/у	14,32	
21	Склад	5,90	
22	Кухня	105,01	
23	Кабинет	46,24	
24	Класс компьютеров	78,85	
25	Лестница	28,07	
26	Тамбур	11,04	
27	Тех. помещение	3,56	
28	Тамбур	35,25	
29	Кабинет	124,97	
Общий итог		1593,60	

Условные обозначения

П-1 — Марка напольного покрытия

+ 45,30 — Площадь

+ 0,000 — Высотная отметка чистого пола

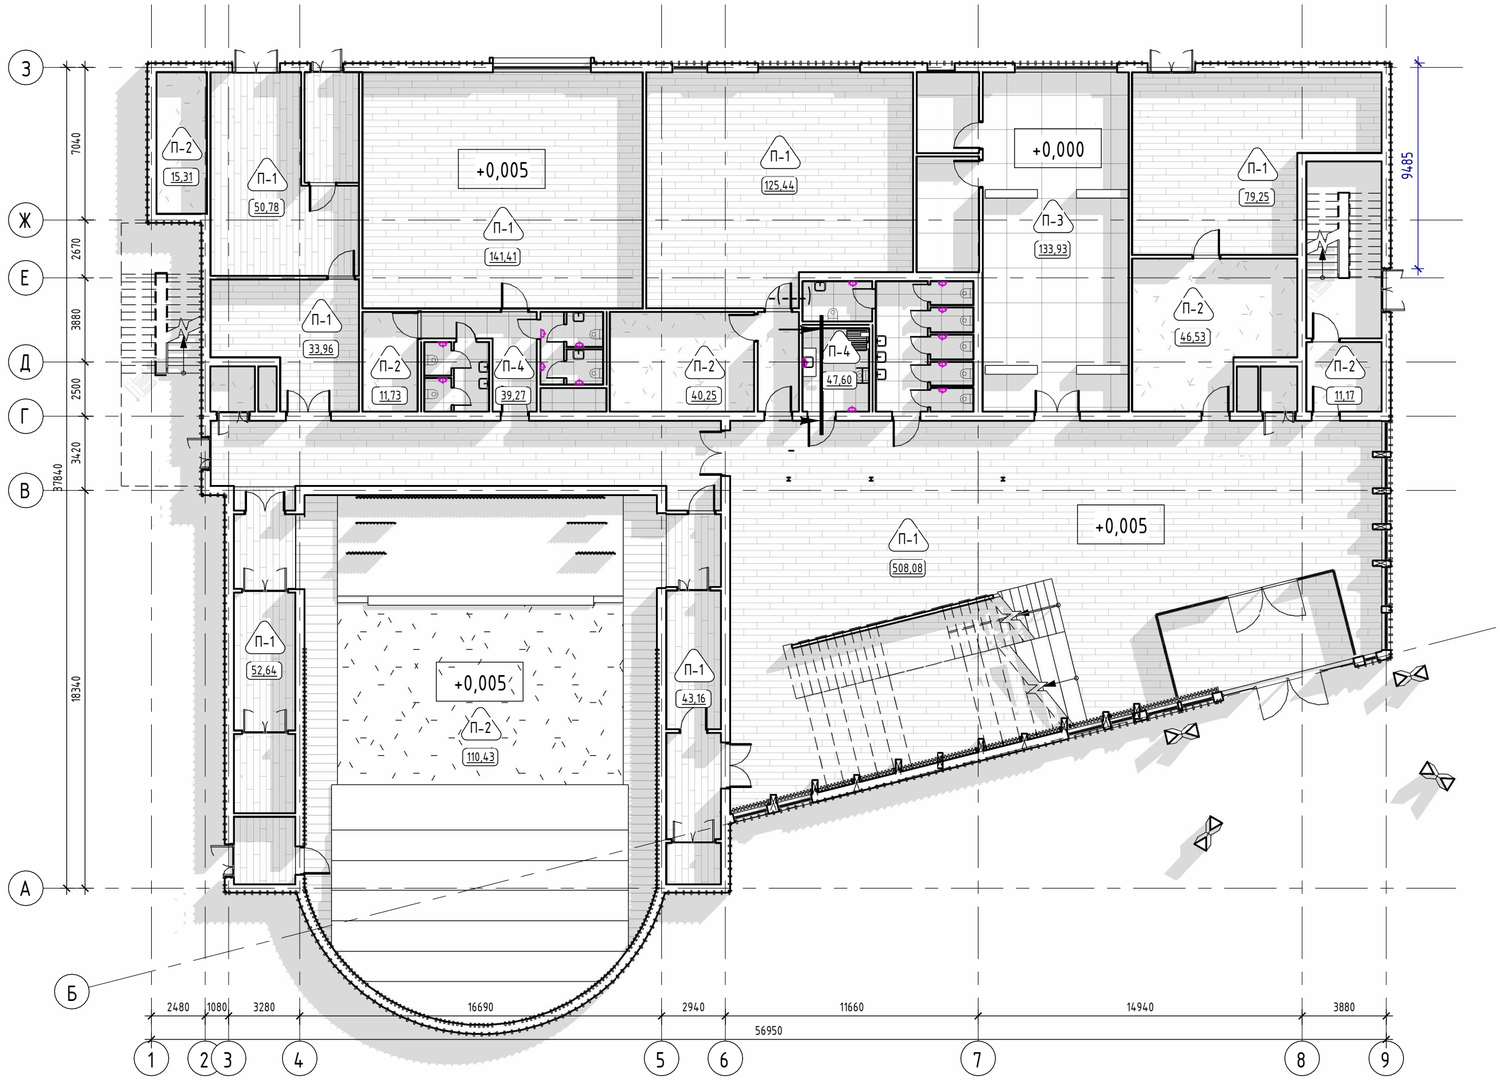

Спецификация перекрытий				
Изображение	Марка	Описание	S,м2	Примечание
	П-1	Паркетная доска светлая	1108,07	
	П-2	Бетонное покрытие	362,85	
	П-3	Кухонная плитка	133,93	
	П-4	Плитка с/у	86,87	

Изм.	Кол.уч.	Лист	№док.	Подп.	Дата	АР			
Разработал						План напольных покрытий на отм. +0.000	Стадия	Лист	Листов
Проверил							П	06	

Формат А2А

Согласовано

Согласовано

Взам. инв. №

Подп. и дата

Инв. № подл.

План размещения сантехнического оборудования на отм. +0,000 М 1:50

Сантехническое оборудование		
Марка	Описание	Количество
Сх-1	Раковина	9
Сх-2	Унитаз	11
Сх-3	Душевая кабина	1

Условные обозначения

Сх-1 — Марка сантехнического оборудования

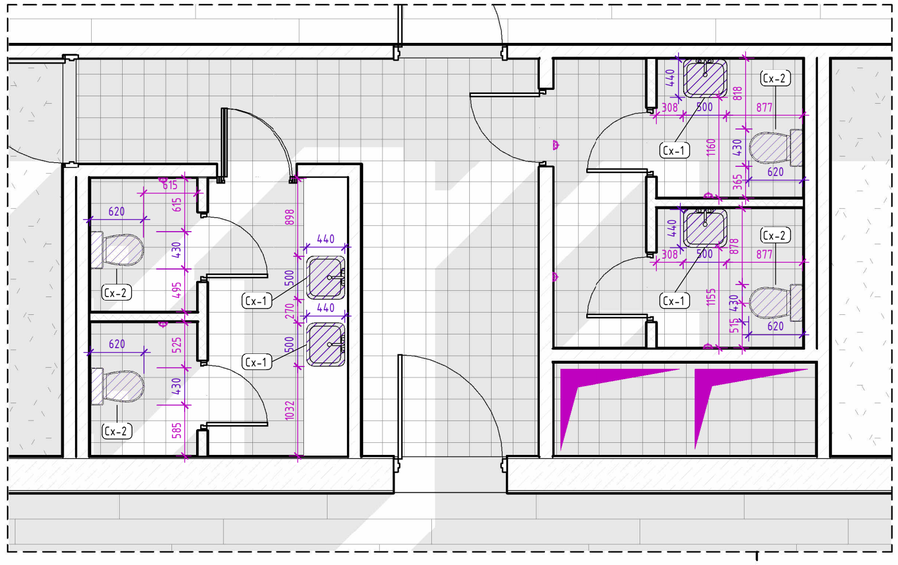

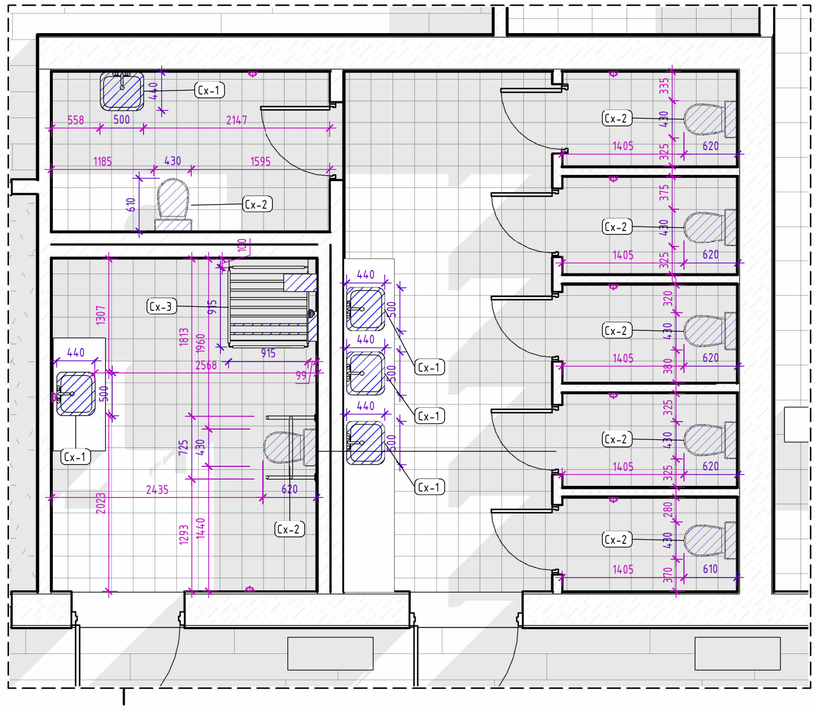

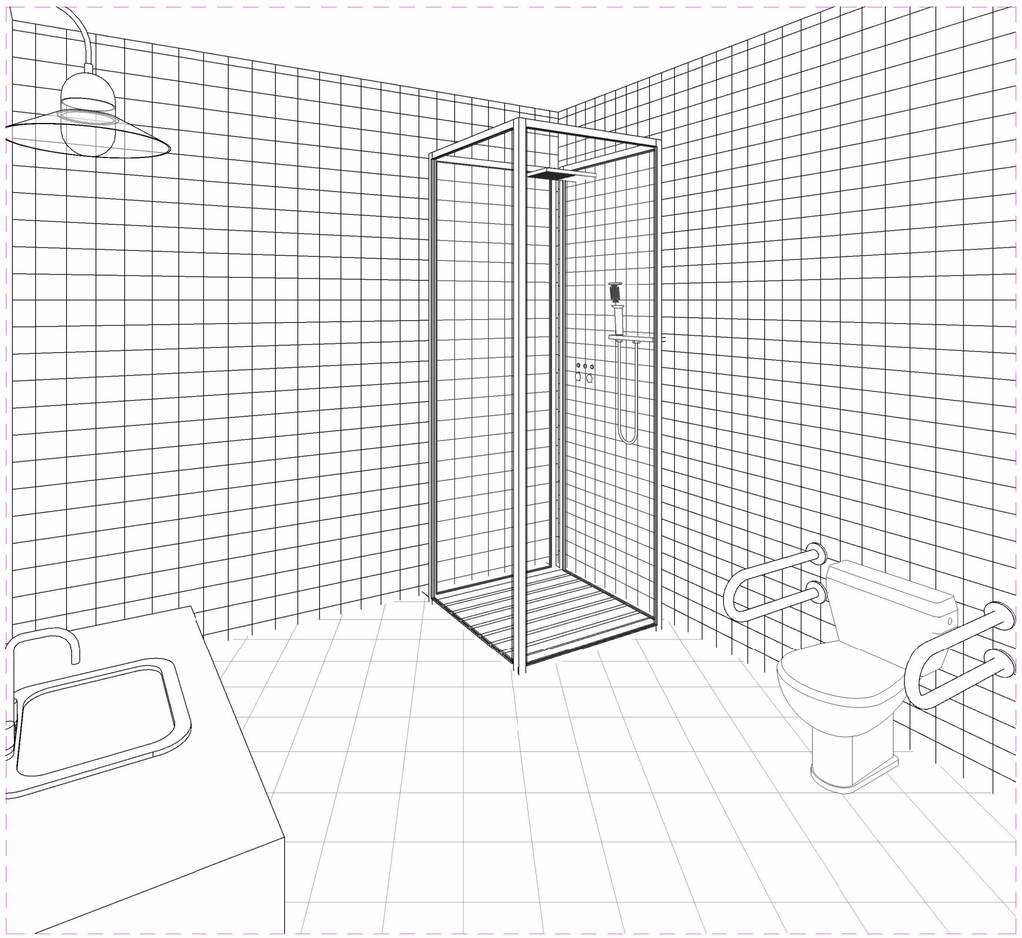

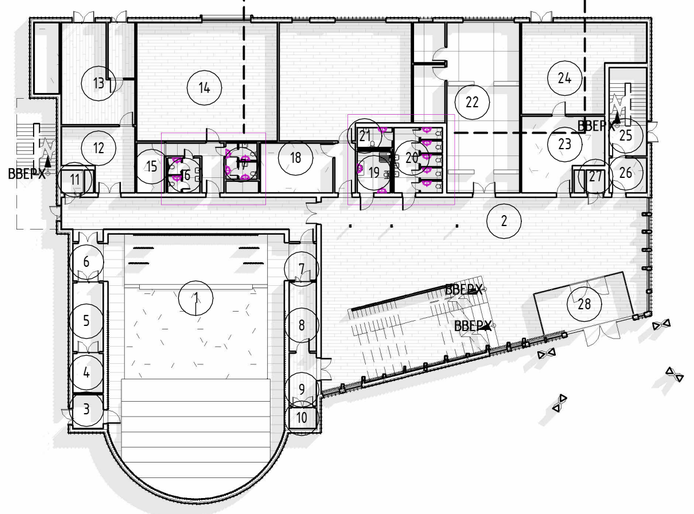

Экспликация помещений 1-го этажа

Номер	Наименование	Площадь	Примечание
1	Актовый зал	370,53	
2	Главный холл	390,86	
3	Тамбур	8,85	
4	Тамбур	10,37	
5	Тамбур	18,08	
6	Тамбур	9,95	
7	Тамбур	8,53	
8	Тамбур	16,00	
9	Тамбур	12,27	
10	Тамбур	4,79	
11	Тех. помещение	4,29	
12	Кабинет	33,70	
13	Кабинет	50,55	
14	Студия рисунка	140,94	
15	Тех. помещение	11,60	
16	С/у	5,16	
17	С/у	2,71	
18	Тех. помещение	30,55	
19	Склад	10,67	
20	С/у	14,32	
21	Склад	5,90	
22	Кухня	105,01	
23	Кабинет	46,24	
24	Класс компьютеров	78,85	
25	Лестница	28,07	
26	Тамбур	11,04	
27	Тех. помещение	3,56	
28	Тамбур	35,25	
29	Кабинет	124,97	
Общий итог		1593,60	

Согласовано

Согласовано

Взам. инв. №

Подп. и дата

Инв. № подл.

Изм.	Кол.уч.	Лист	№док.	Подп.	Дата	АР			
Разработал						План размещения сантехнического оборудования на отм. +0.000	Стадия	Лист	Листов
Проверил							П	07	

Формат А2А

План размещения осветительного оборудования на отм. +0,000

Экспликация помещений 1-го этажа

Номер	Наименование	Площадь	Примечание
1	Актовый зал	370,53	
2	Главный холл	390,86	
3	Тамбур	8,85	
4	Тамбур	10,37	
5	Тамбур	18,08	
6	Тамбур	9,95	
7	Тамбур	8,53	
8	Тамбур	16,00	
9	Тамбур	12,27	
10	Тамбур	4,79	
11	Тех. помещение	4,29	
12	Кабинет	33,70	
13	Кабинет	50,55	
14	Студия рисунка	140,94	
15	Тех. помещение	11,60	
16	С/у	5,16	
17	С/у	2,71	
18	Тех. помещение	30,55	
19	Склад	10,67	
20	С/у	14,32	
21	Склад	5,90	
22	Кухня	105,01	
23	Кабинет	46,24	
24	Класс компьютеров	78,85	
25	Лестница	28,07	
26	Тамбур	11,04	
27	Тех. помещение	3,56	
28	Тамбур	35,25	
29	Кабинет	124,97	
Общий итог		1593,60	

Спецификация осветительных приборов

Марка	Изображение	Описание	Число
Ос-1		Recessed luminaire	2
Ос-2		EAE_ARI_36W	2
Ос-3		Светильник потолочный 36W	45
Ос-4		Подвесной светильник 100W	34
Ос-5		Настеный светильник 100W	14
Ос-6		Подвесной светильник длинный 277W	13

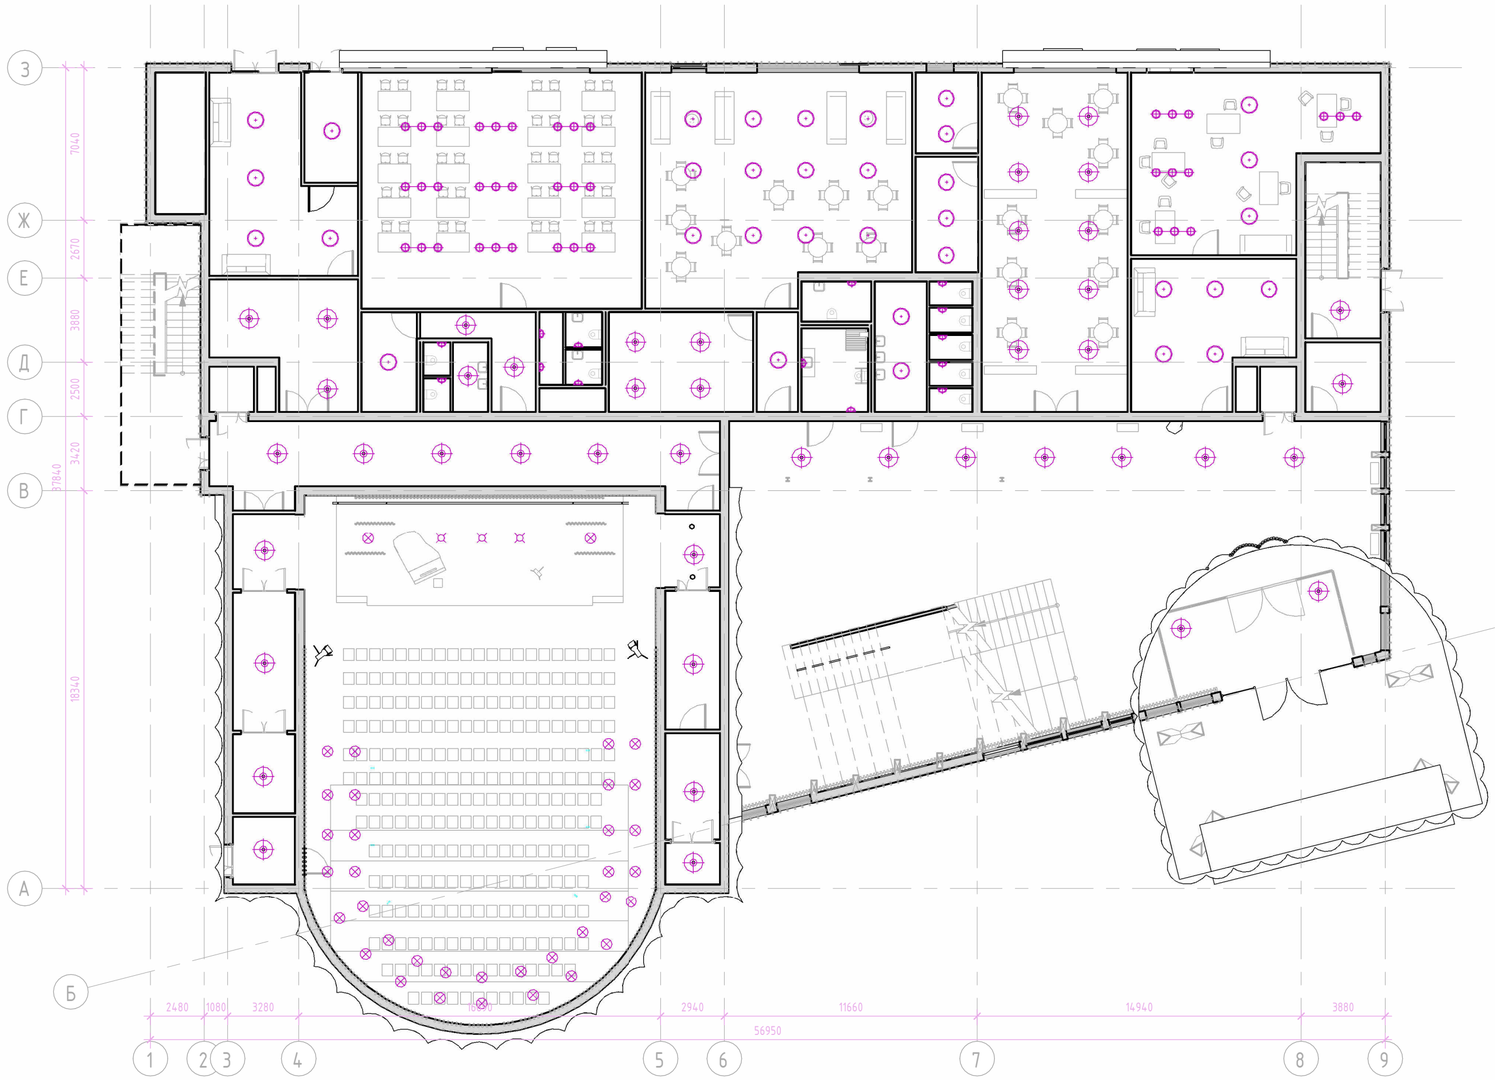

Условные обозначения

Марка осветительного прибора

1 Номер помещения

Изм.	Кол.уч.	Лист	№док.	Подп.	Дата	АР			
Разработал						План размещения осветительного оборудования на отм. +0.000	Стадия	Лист	Листов
Проверил							П	08	

Согласовано

Согласовано

Взам. инв. №

Подп. и дата

Инв. № подл.

Формат А2А

План маркировки дверных проемов на отм. +0,000

Экспликация помещений 1-го этажа

Номер	Наименование	Площадь	Примечание
1	Актовый зал	370,53	
2	Главный холл	390,86	
3	Тамбур	8,85	
4	Тамбур	10,37	
5	Тамбур	18,08	
6	Тамбур	9,95	
7	Тамбур	8,53	
8	Тамбур	16,00	
9	Тамбур	12,27	
10	Тамбур	4,79	
11	Тех. помещение	4,29	
12	Кабинет	33,70	
13	Кабинет	50,55	
14	Студия рисунка	140,94	
15	Тех. помещение	11,60	
16	С/у	5,16	
17	С/у	2,71	
18	Тех. помещение	30,55	
19	Склад	10,67	
20	С/у	14,32	
21	Склад	5,90	
22	Кухня	105,01	
23	Кабинет	46,24	
24	Класс компьютеров	78,85	
25	Лестница	28,07	
26	Тамбур	11,04	
27	Тех. помещение	3,56	
28	Тамбур	35,25	
29	Кабинет	124,97	
Общий итог		1593,60	

Спецификация дверных проемов

Марка	Описание	Габариты		Количество
		Высота	Ширина	
Д-1	Porte Alu Grand Trafic KL-GT	2400	2110	2
Д-2	Дверь маятниковая одинарная	2100	1200	61
Д-3	Porte Alu Grand Trafic KL-GT	2400	1500	13
Д-4	Дверь маятниковая двойная	2000	1800	1
Д-5	Дверь маятниковая двойная 2	2100	2000	8
Д-6	Дверь деревянная наружная остекленная	2100	900	2
Д-7	Дверь деревянная внутренняя глухая	2100	800	7
Д-8	Дверь деревянная внутренняя глухая	2100	800	2
Д-9	Porte Alu Grand Trafic KL-GT	2435	2170	2
Д-11	Дверь Витраж одинарная	<варианты>	<варианты>	5
Д-12	Porte Alu Grand Trafic KL-GT	2400	2000	3

Условные обозначения

Д-1 / В-2100 Ш-900 — Марка дверного проема

1 — Номер помещения

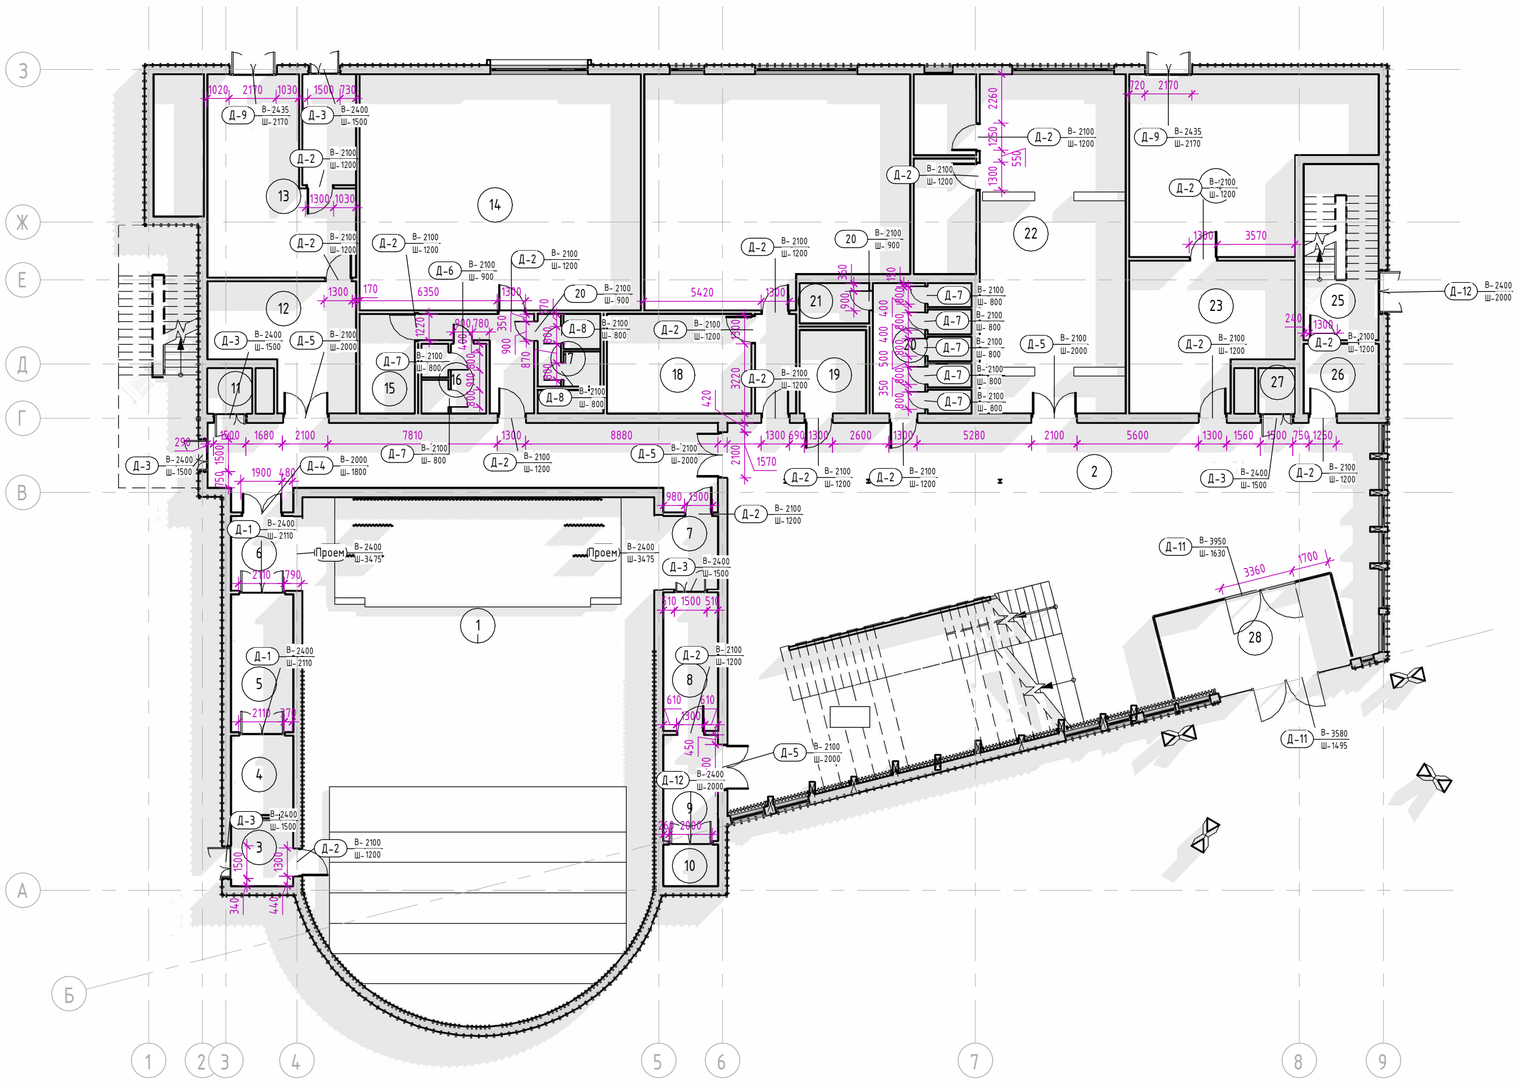

Марка	Д-1	Д-2	Д-3	Д-4	Д-5	Д-6	Д-7	Д-9	Д-10	Д-12
Описание	Porte Alu Grand Trafic KL-GTписание	Дверь маятников. одинарная	Porte Alu Grand Trafic KL-GT	Дверь маятников. двойная	Дверь маятников. двойная 2	Дверь дерев. наруж.остекл.	Дверь дерев. внутр. глух.	Porte Alu Grand Trafic KL-GT	Firepoof sliding double door	Porte Alu Grand Trafic KL-GT
Схема фасада	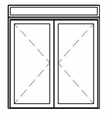	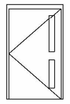		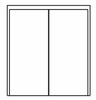	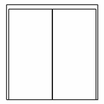	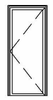	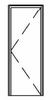	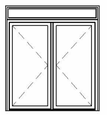	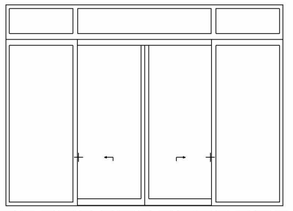	
Схема на плане					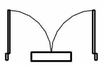					

Изм.	Кол.уч.	Лист	№док.	Подп.	Дата	АР			
Разработал						План маркировки дверных проемов на отм. +0.000	Стадия	Лист	Листов
Проверил							П	09	

Согласовано

Согласовано

Взам. инв. №

Подп. и дата

Инв. № подл.

Формат А2А

Развертки стен и аксонометрия актового зала

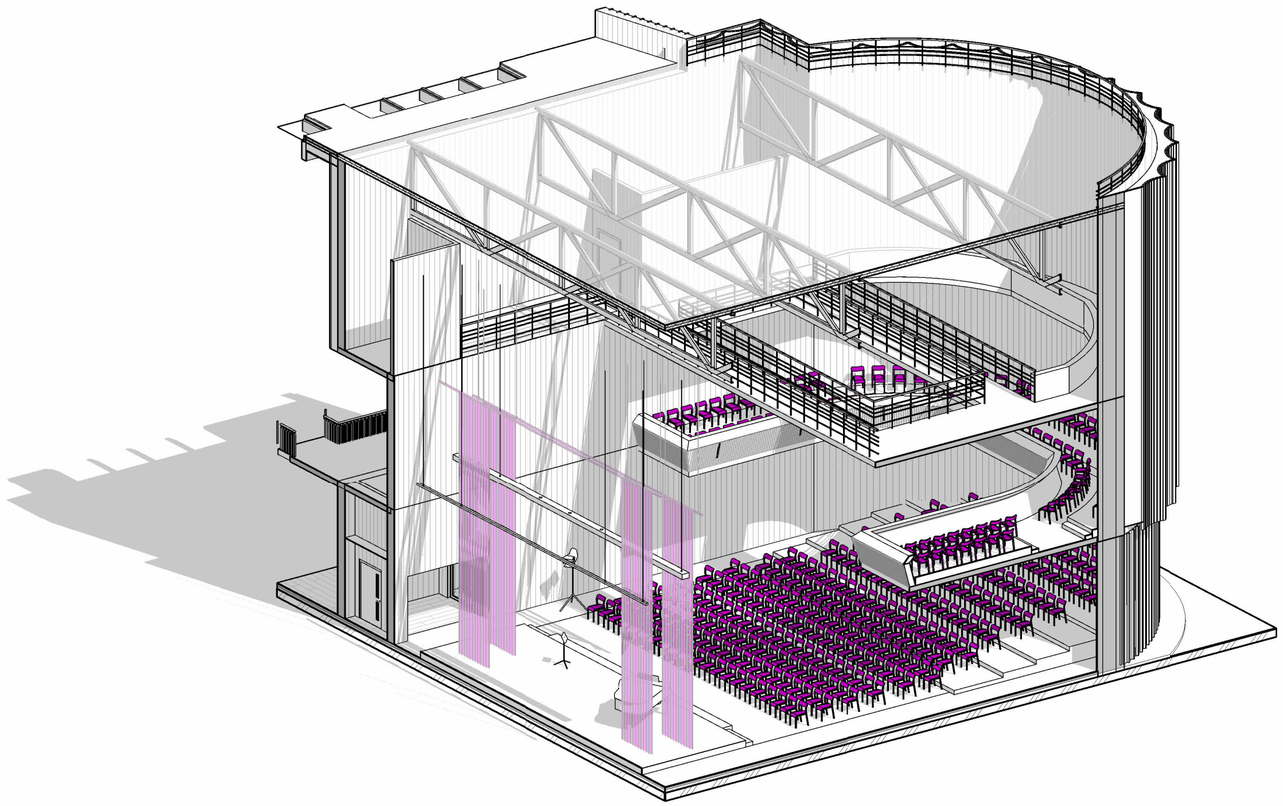

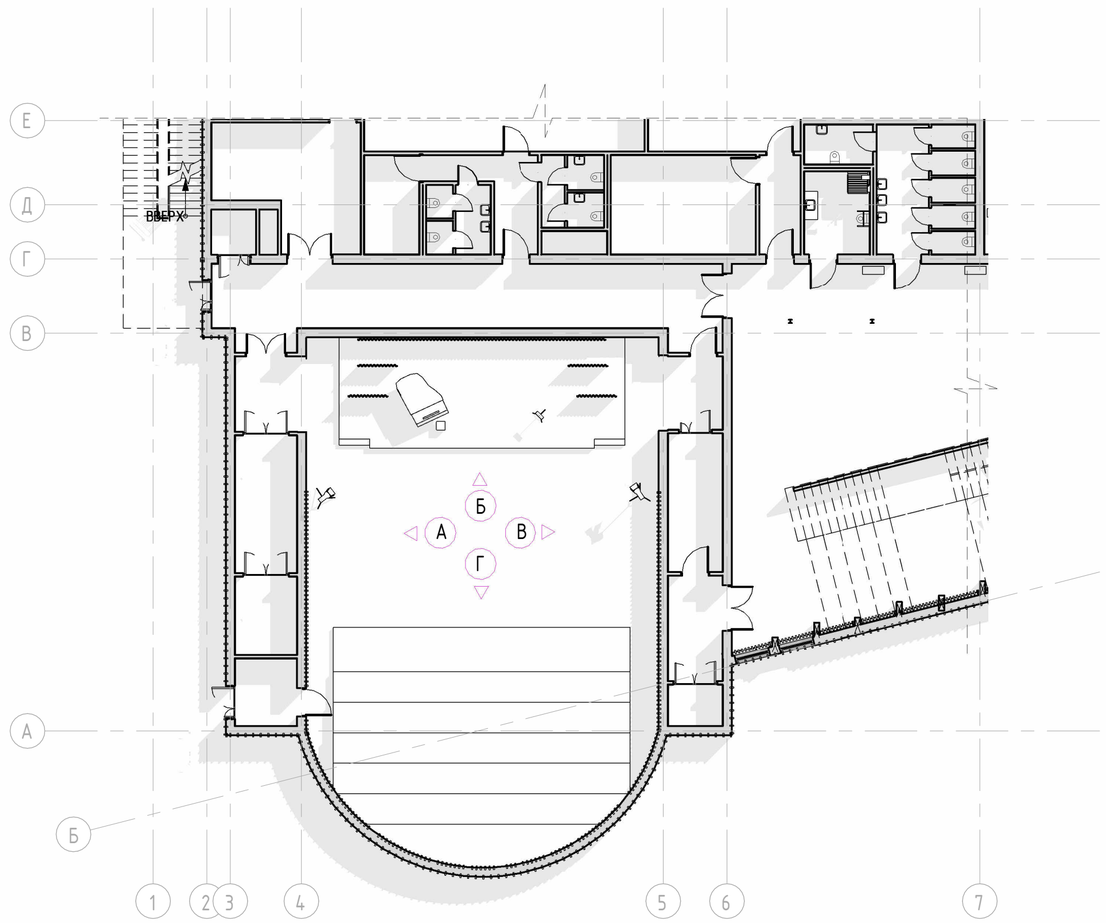

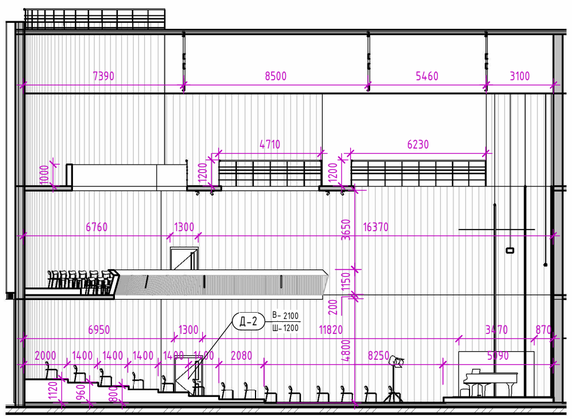

Фасад А

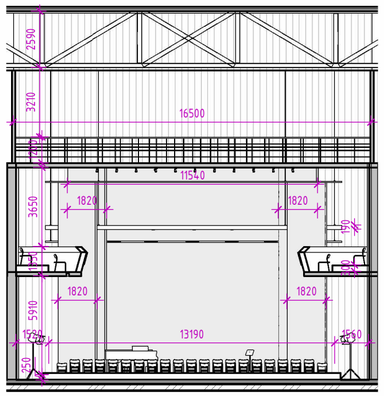

Фасад Б

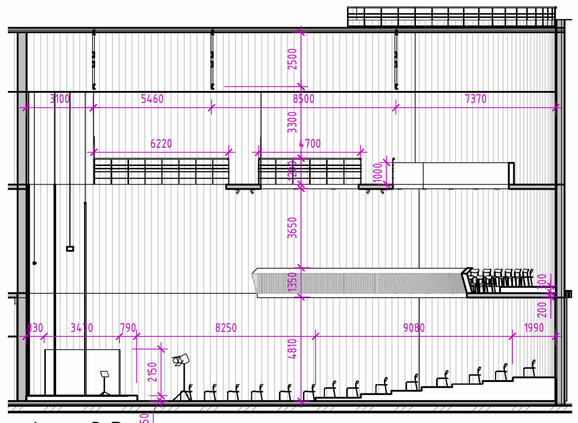

Фасад В

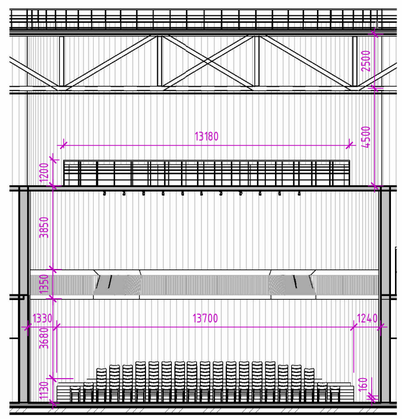

Фасад Г

Условные обозначения

Д-1 — В-2100 / Ш-900 — Марка дверного проема

Б — Направление фасада

Изм.	Кол.уч.	Лист	№док.	Подп.	Дата	АР		
Разработал						Развертки стен и аксонометрия актового зала	Стадия	Лист	Листов
Проверил							П	10	

Формат А2А

Согласовано

Согласовано

Взам. инв. №

Подп. и дата

Инв. № подл.

Взрыв схема, Аксонометрия

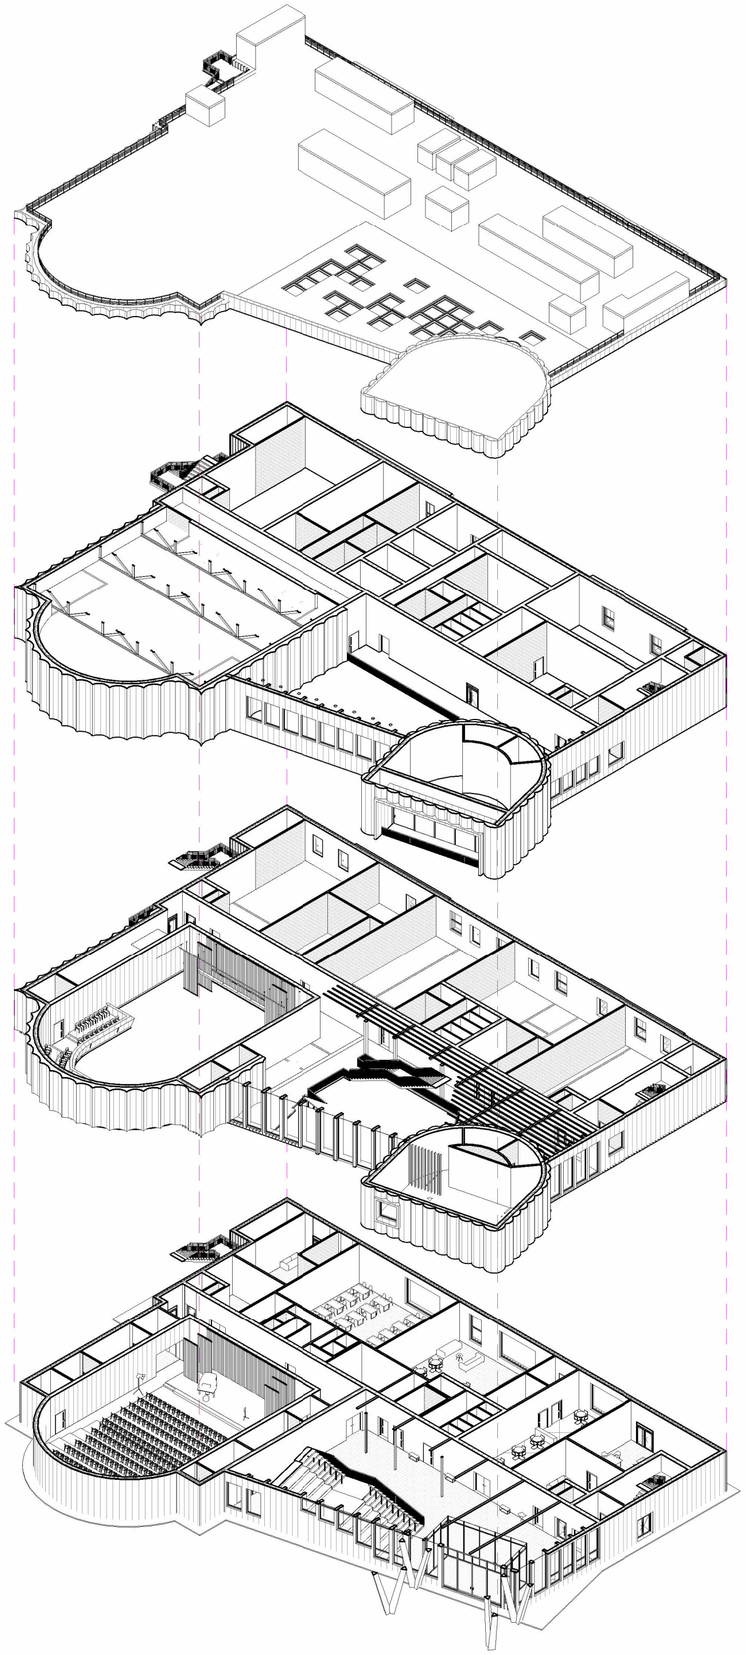

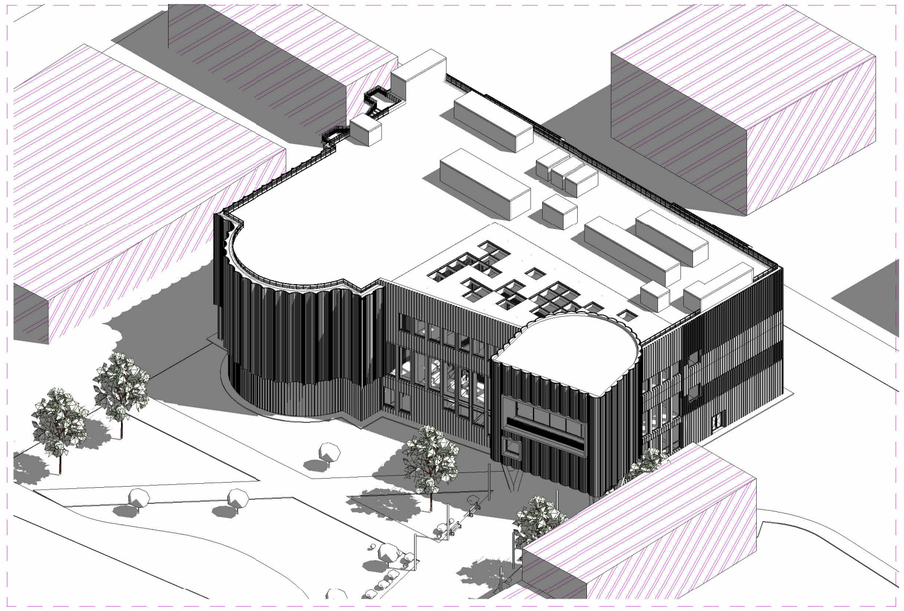

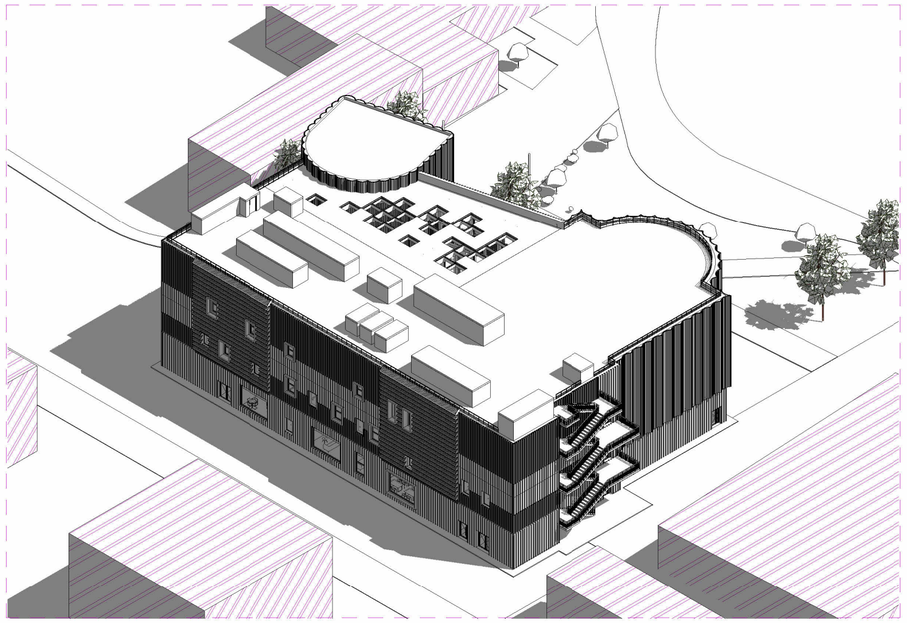

Изм.	Кол.уч.	Лист	№док.	Подп.	Дата	АР		
Разработал						Взрыв схемы, Аксонометрия	Стадия	Лист	Листов
Проверил							П	11	

Согласовано

Согласовано

Взам. инв. №

Подп. и дата

Инв. № подл.

Формат А2А

Фасад-1, Разрез 9-3

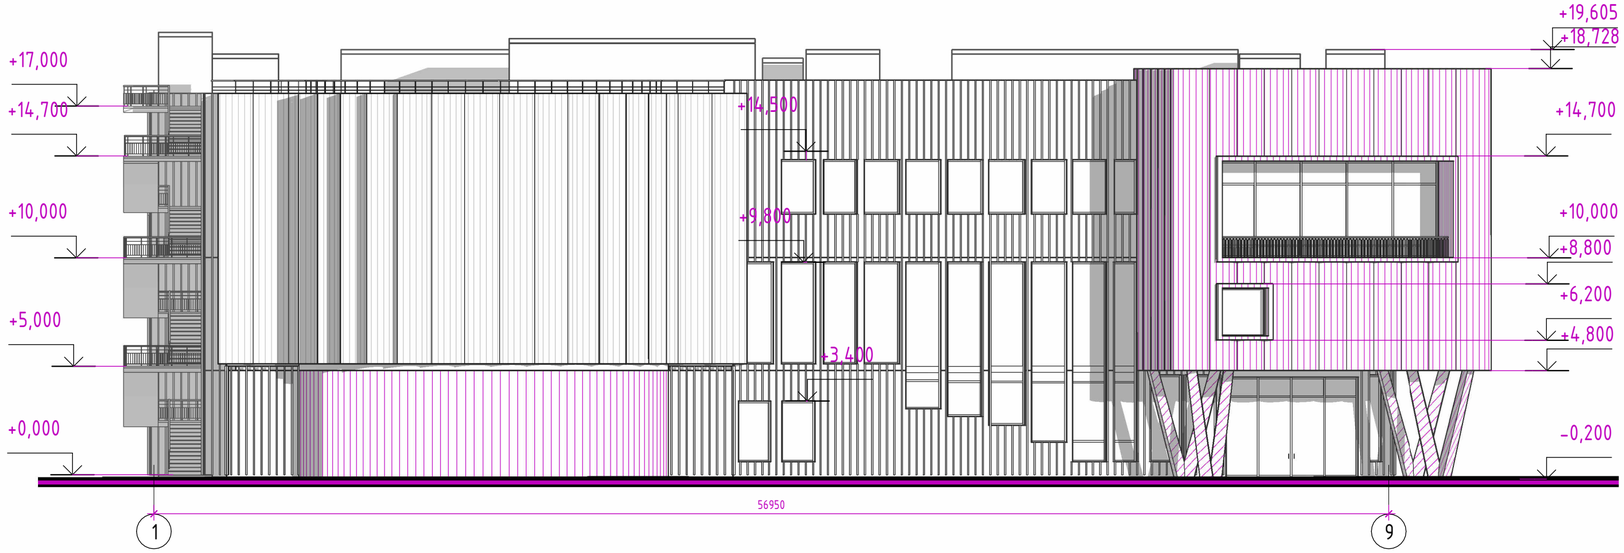

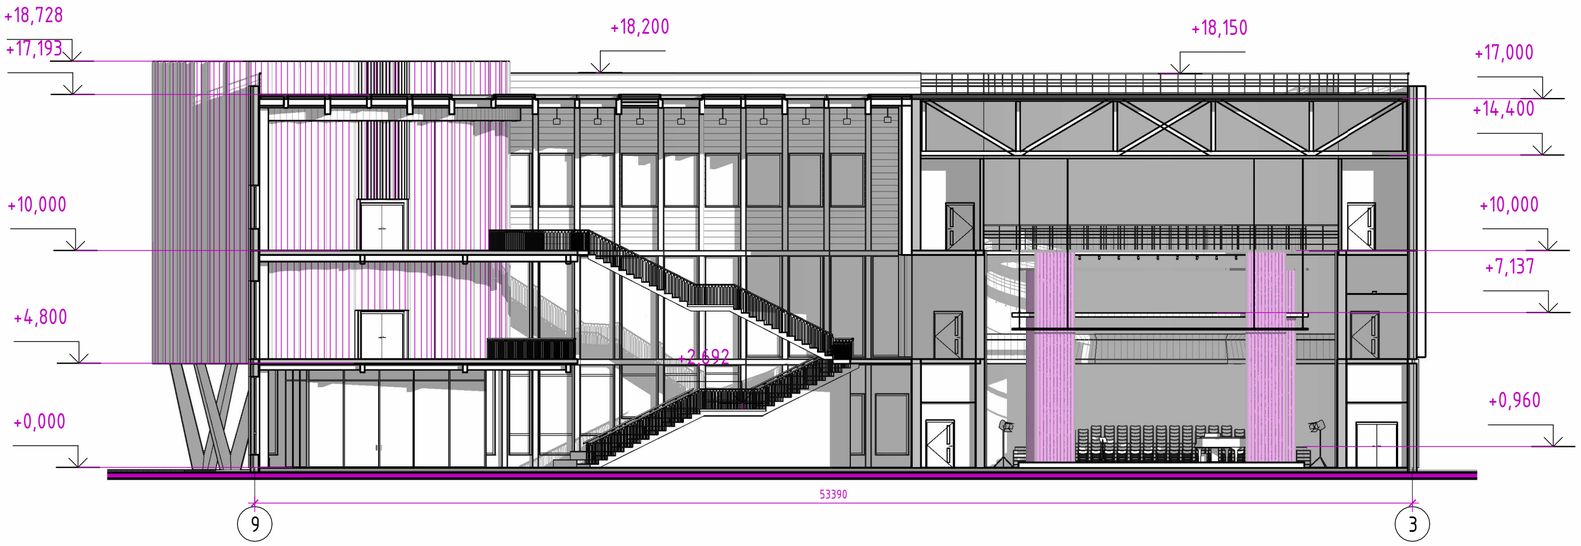

Согласовано

Согласовано

Взам. инв. №

Подп. и дата

Инв. № подл.

Изм.	Кол.уч.	Лист	№док.	Подп.	Дата	АР		
Разработал						Фасад-1, Разрез 9-3	Стадия	Лист	Листов
Проверил							П	12	

Формат А2А

Фасады - 2,3,4

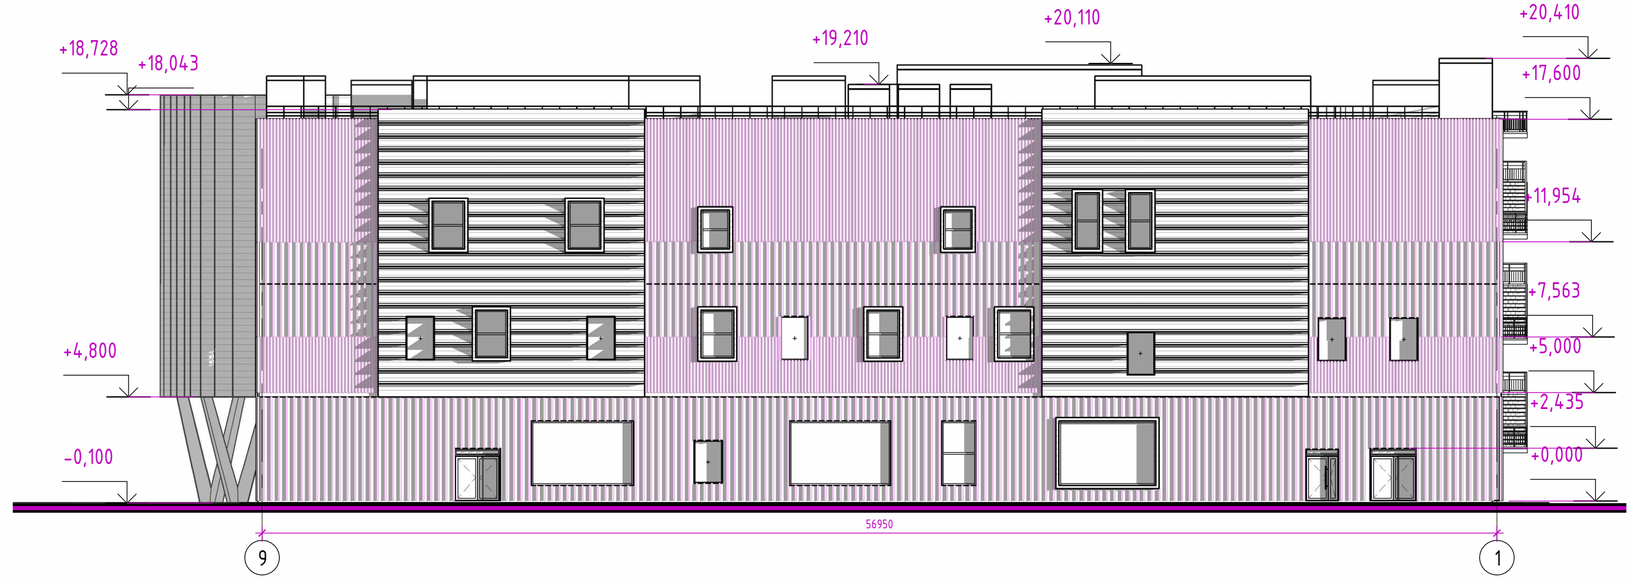

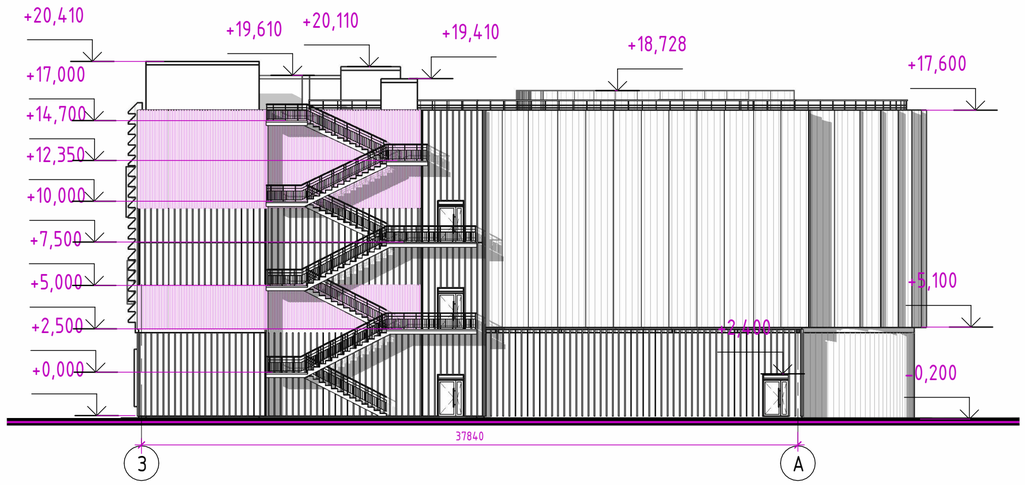

Согласовано

Согласовано

Взам. инв. №

Подп. и дата

Инв. № подл.

Изм.	Кол.уч.	Лист	№док.	Подп.	Дата	АР		
Разработал						Фасады-2,3,4	Стадия	Лист	Листов
Проверил							П	13	

Формат А2А

3д-разрезы, Вид-1

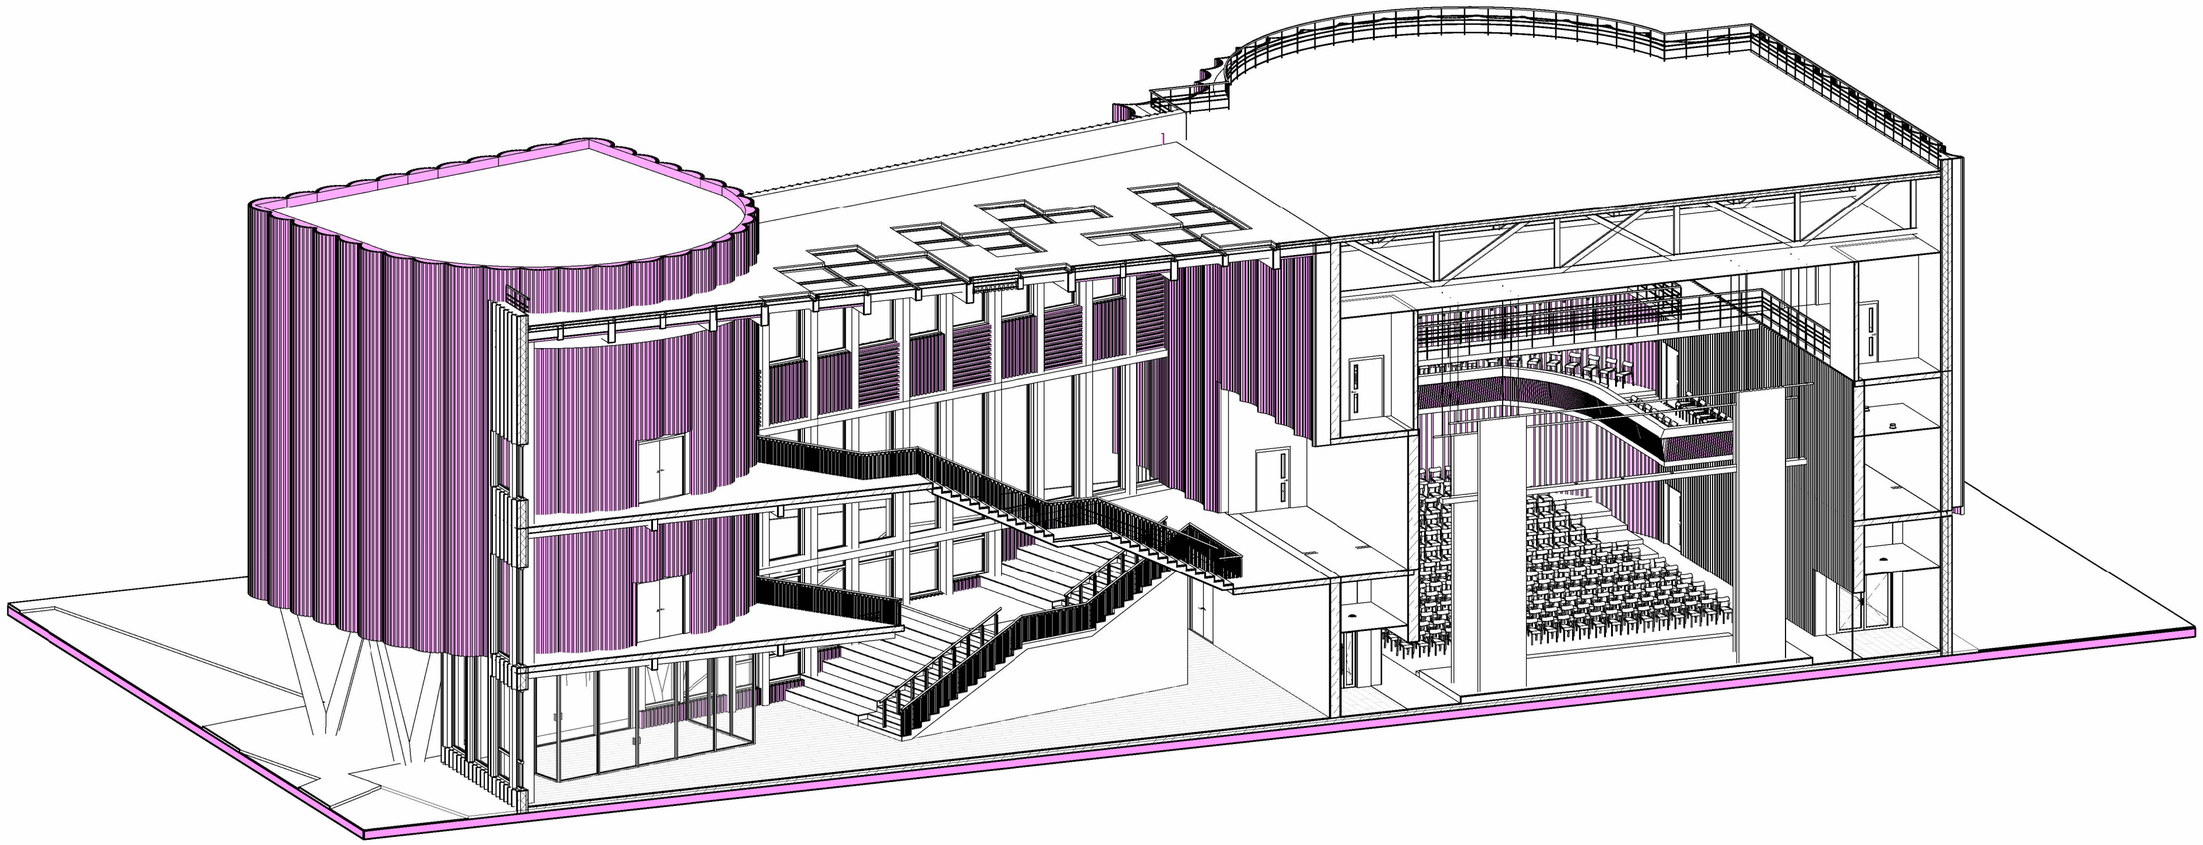

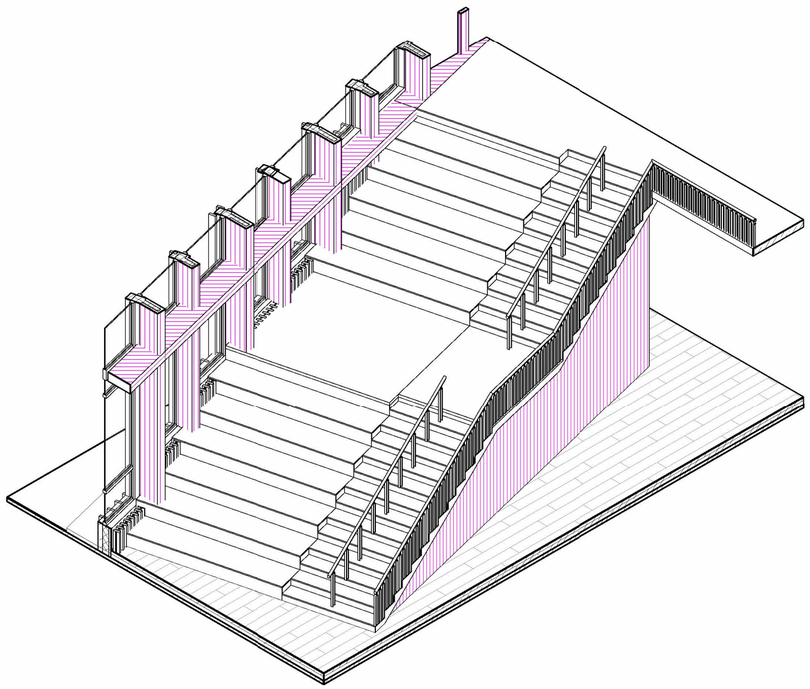

Согласовано

Согласовано

Взам. инв. №

Подп. и дата

Инв. № подл.

Изм.	Кол.уч.	Лист	№док.	Подп.	Дата	АР			
Разработал						3д-разрезы, Вид-1	Стадия	Лист	Листов
Проверил							П	14	

Формат А2А

Перспективные виды-2,3,4

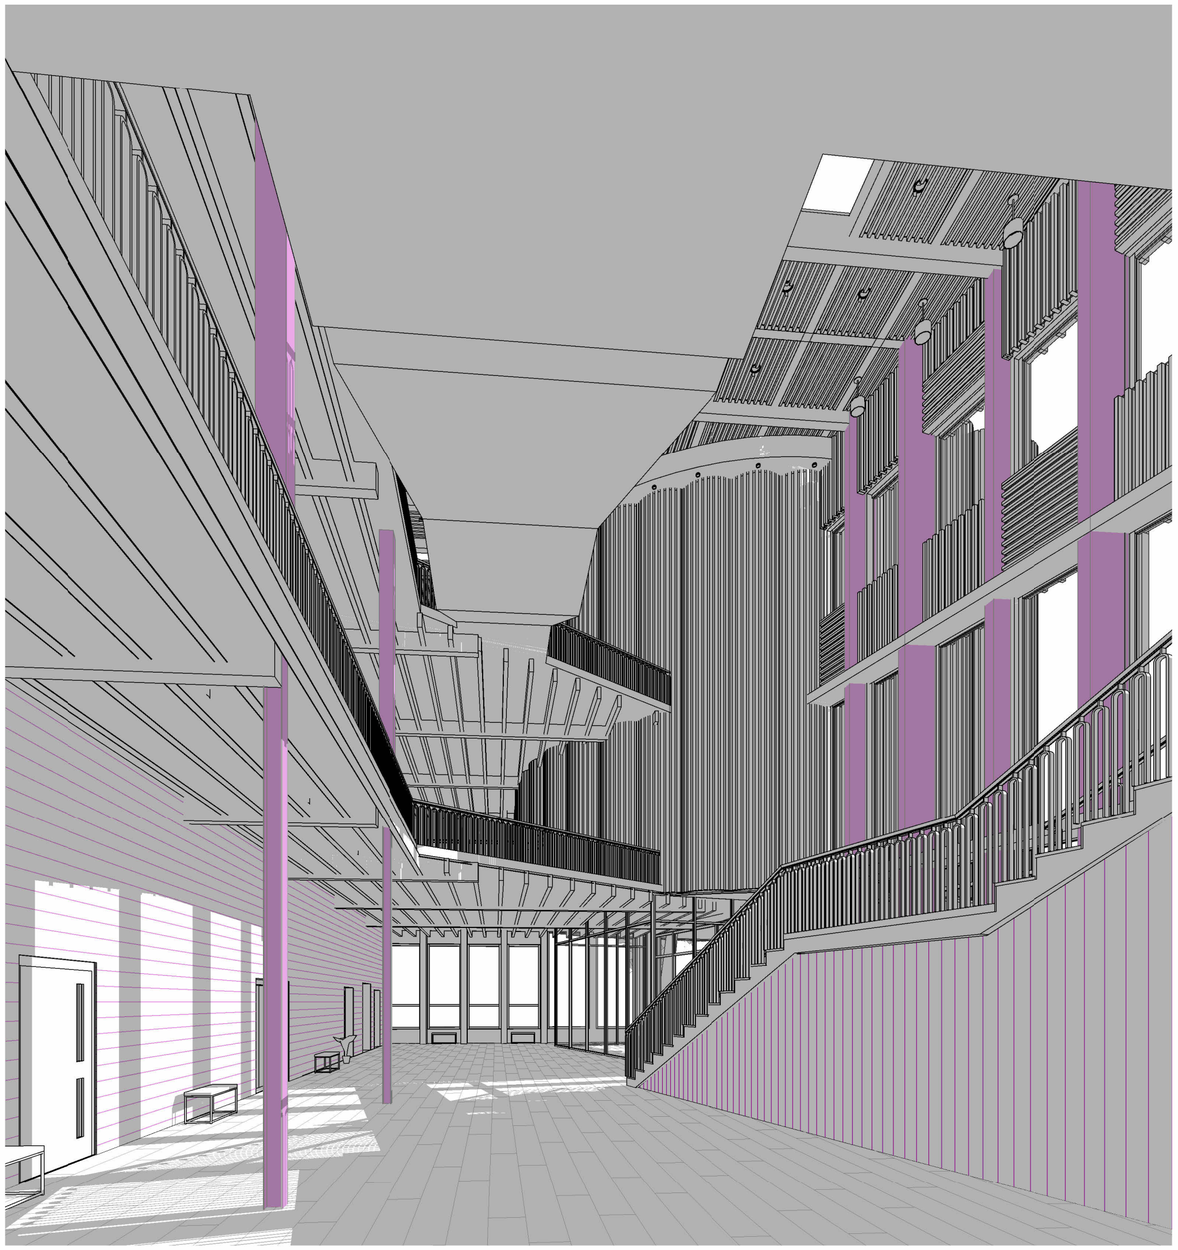

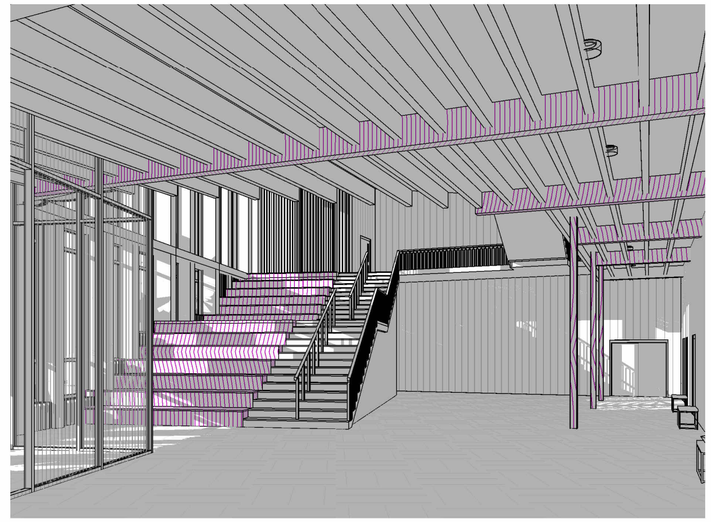

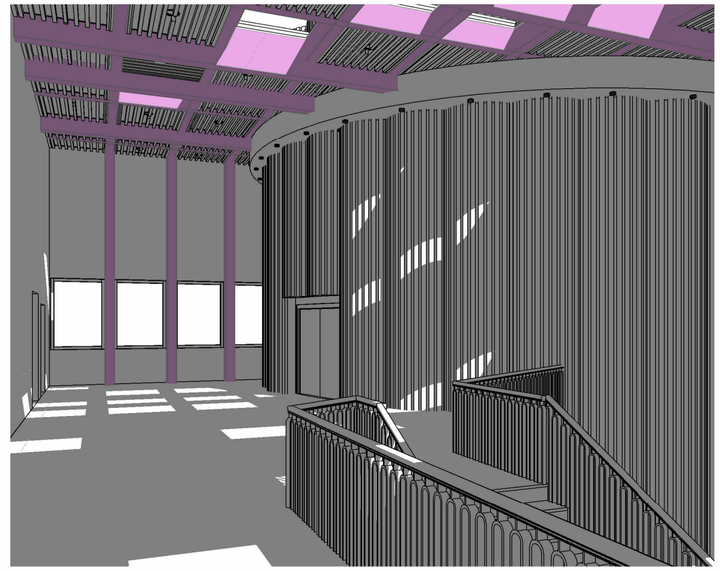

Согласовано

Согласовано

Взам. инв. №

Подп. и дата

Инв. № подл.

Изм.	Кол.уч.	Лист	№док.	Подп.	Дата	АР			
Разработал						Виды-2,3,4	Стадия	Лист	Листов
Проверил							П	15	

Формат А2А