Creative Center at York St John University



Самотстоятельная работа в рамках курса REVIT+ENSCAPE+PHOTOSHOP
Продвинутый курс от команды ArtBrodsky
Референс: Creative Center at York St John University

Автор и преподаватель курса: Дарья Климчук
Выполнил: Шамсиддинов Умид

Изм.	Кол.уч.	Лист	№док.	Подп.	Дата	Creative Center at York St John University - AP	Лист 01

Взам. инв. №
Подп. и дата
Инв. № подл.

Формат А2А

Ведомость рабочих чертежей основного комплекта

Лист	Наименование	Примечание
02	Общие данные	
03	Кладочный план 1-го этажа на отм. +0,000	
04	План эргономики 1-го этажа	
05	План отделки стен 1-го этажа	
06	План напольных покрытий на отм. +0,000	
07	Планы размещения сантехнического оборудования 1-го этажа	
08	План расстановки осветительного оборудования 1-го этажа	
09	План маркировки дверных проёмов 1-го этажа	
10	Аксонометрия актового зала, развёртки по актовому залу	
11	Разрез 1-1, Аксонометрия разреза, аксонометрия лестницы	
12	Фасад 1-11 М 1 к 200, фасад 11-1 М 1 к 200	
13	Фасад А-И М 1 к 200, фасад И-А М 1 к 200	
14	Аксонометрия здания, взрыв-схема	
15	Перспективные виды	

Согласовано

Согласовано

Взам. инв. №

Подп. и дата

Инв. № подл.


Изм.	Кол.уч.	Лист	№док.	Подп.	Дата	Creative Center at York St John University - AP			
Разработал		Шамсиддинов. У				Общие данные	Стадия	Лист	Листов
Проверил		Art Brodsky					АР	02	

Формат А2А

Кладочный план на отм. +0.000
М 1:200

Экспликация помещений 1-го этажа

№	Наименование	Площадь	Примечание
1	Тамбур	22,52	
2	Главный холл	354,38	
3	Коридор	78,36	
4	Коридор	9,91	
5	Коридор	9,91	
6	Коридор	9,88	
7	Кладовая	13,78	
8	Тамбур	10,39	
9	Техническое помещение	6,56	
10	Актовый зал	409,88	
11	Коридор	9,35	
12	Помещение для хранения	30,72	
13	С/у	9,30	
14	С/у	5,52	
15	Кладовая	12,36	
16	Лекторий	121,85	
17	Кафе	109,25	
18	Помещение тех. обслуживания	82,52	
19	Зона отдыха	50,38	
20	Коридор	11,15	
21	Тамбур	28,53	
22	Коридор	12,78	
23	Техническое помещение	3,55	
24	С/у	2,58	
25	С/у	11,65	
26	С/у	4,08	
27	Помещение	135,99	
28	Помещение тех. обслуживания	13,70	
29	Кладовая	49,98	
30	Техническое помещение	33,96	
31	Помещение тех. обслуживания	14,80	
32	Техническое помещение	4,16	
33	Техническое помещение	7,46	
34	Техническое помещение	13,74	
35	Техническое помещение	3,75	
Общий итог		1708,69	

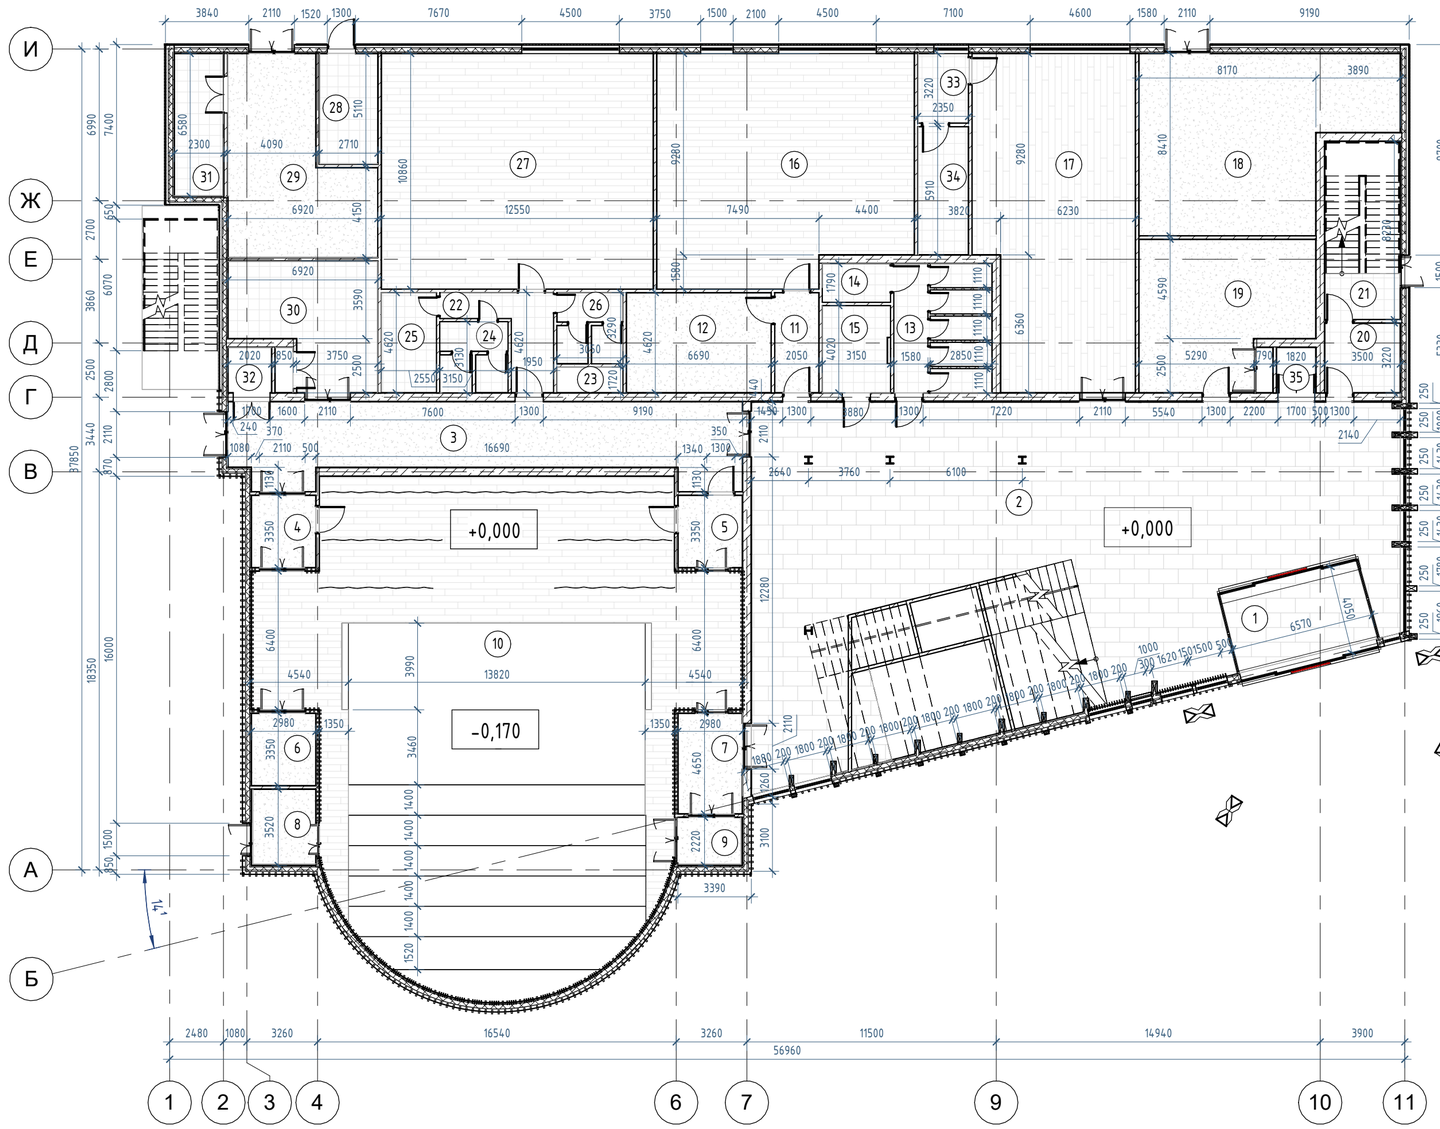

Условные обозначения

(1) Номер помещения

+0,000 Высотная отметка чистового пола

Размеры

Примечания

1. Комплект рабочих чертежей разработани на основании обмеров.
2. Обмерные работы выполнялись по существующей предчистовой отделке.
3. Оконные проёмы обмерены по откосу в плоскости стены.
4. Материалы стен показаны условно.
5. Размеры стен и площадей по обмерам могут отличаться не более, чем на 2% (в случае больших расхождений связаться с проектировщиком для принятия решения).
6. Высота помещений первого этажа 5000 мм.

Согласовано

Согласовано

Взам. инв. №

Подп. и дата

Инв. № подл.

Изм.	Кол.уч.	Лист	№док.	Подп.	Дата	Creative Center at York St John University - AP			
Разработал		Шамсиддинов. У				Кладочный план 1-го этажа на отм. +0,000	Стадия	Лист	Листов
Проверил		Art Brodsky					АР	03	

Формат А2А

План эргономики на отм. +0.000
М 1:200

Экспликация помещений 1-го этажа


№	Наименование	Площадь	Примечание
1	Тамбур	22,52	
2	Главный холл	354,38	
3	Коридор	78,36	
4	Коридор	9,91	
5	Коридор	9,91	
6	Коридор	9,88	
7	Кладовая	13,78	
8	Тамбур	10,39	
9	Техническое помещение	6,56	
10	Актовый зал	409,88	
11	Коридор	9,35	
12	Помещение для хранения	30,72	
13	С/у	9,30	
14	С/у	5,52	
15	Кладовая	12,36	
16	Лекторий	121,85	
17	Кафе	109,25	
18	Помещение тех. обслуживания	82,52	
19	Зона отдыха	50,38	
20	Коридор	11,15	
21	Тамбур	28,53	
22	Коридор	12,78	
23	Техническое помещение	3,55	
24	С/у	2,58	
25	С/у	11,65	
26	С/у	4,08	
27	Помещение	135,99	
28	Помещение тех. обслуживания	13,70	
29	Кладовая	49,98	
30	Техническое помещение	33,96	
31	Помещение тех. обслуживания	14,80	
32	Техническое помещение	4,16	
33	Техническое помещение	7,46	
34	Техническое помещение	13,74	
35	Техническое помещение	3,75	
Общий итог		1708,69	

Условные обозначения

(1) Номер помещения

+0,000 Высотная отметка чистового пола

Размеры

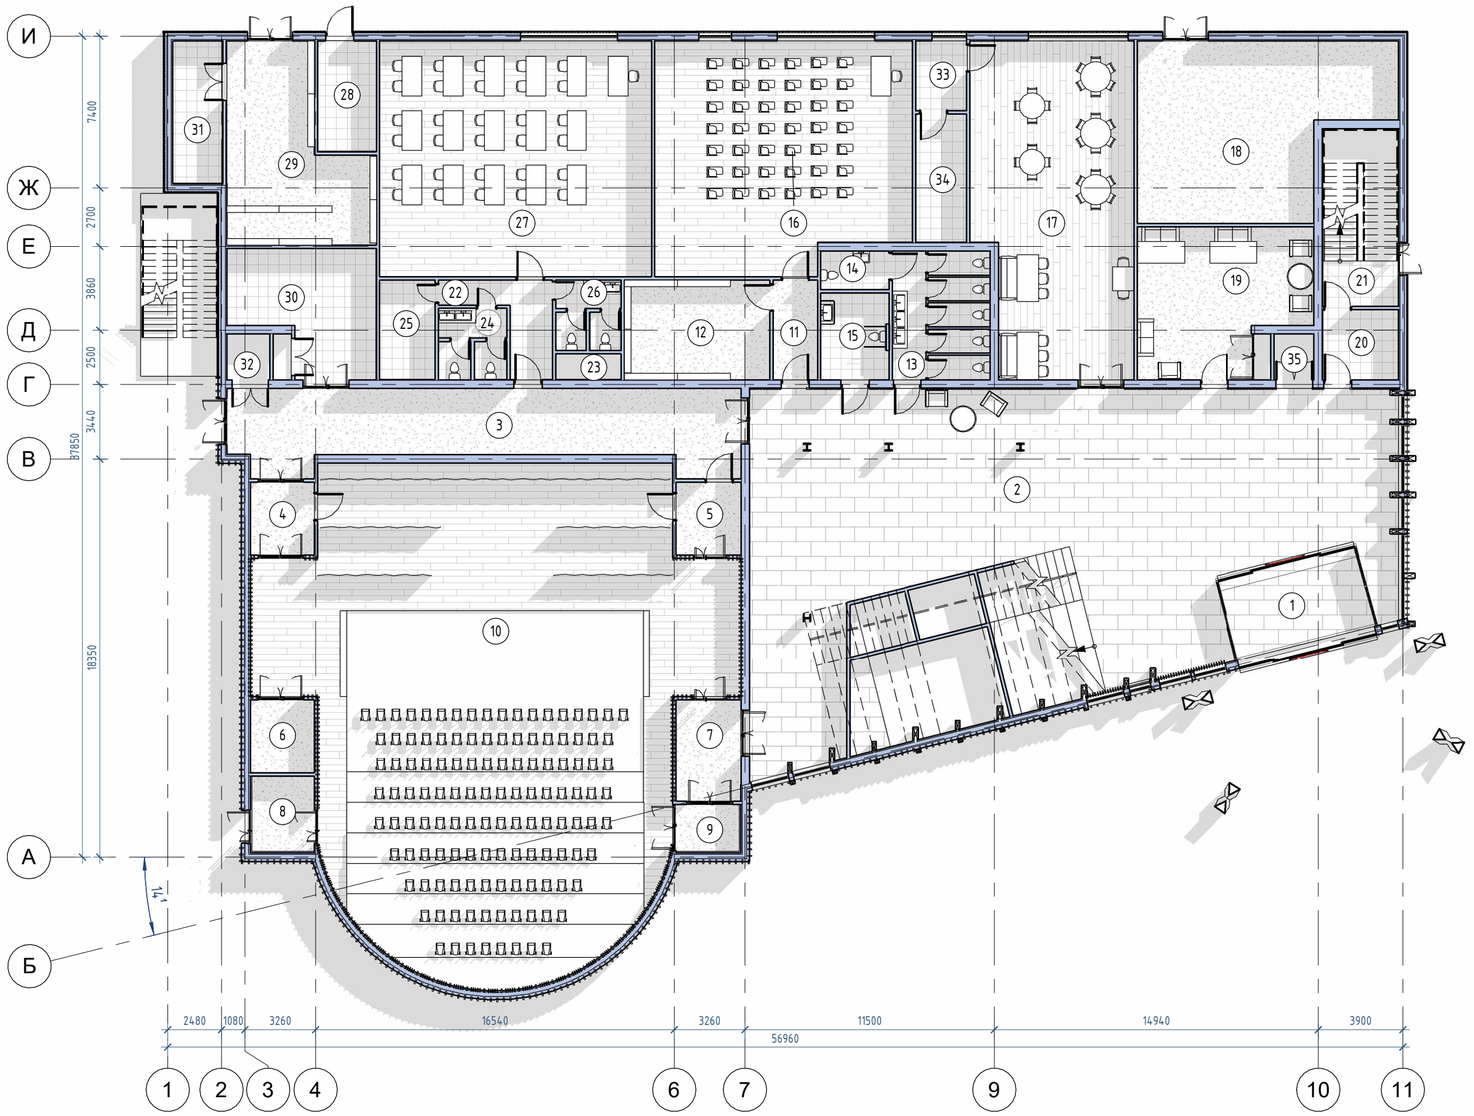




Легенда зонирования

- Зона входной группы
- Общественная зона
- Зона пищевого блока
- Зона актового зала
- Учебная зона
- Санитарно-гигиеническая зона
- Зона тех. обслуживания
- Зона хранения



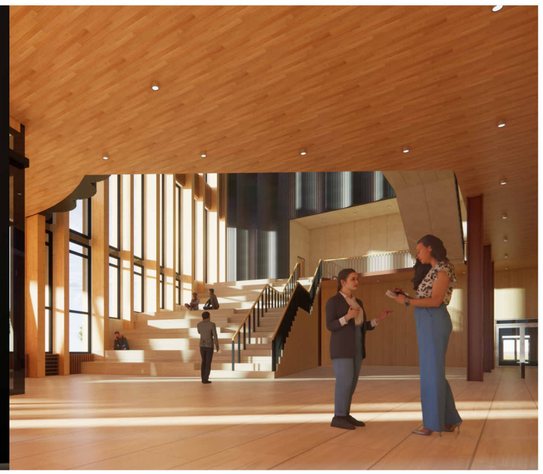

Изм.	Кол.уч.	Лист	№док.	Подп.	Дата	Creative Center at York St John University - AP		
Разработал		Шамсиддинов. У				План эргономики 1-го этажа	Стадия	Лист	Листов
Проверил		Art Brodsky					АР	04	

Согласовано

Согласовано

Взам. инв. №

Подп. и дата


Инв. № подл.


Формат А2А

План отделки стен 1-го этажа
М 1:200

Экспликация помещений 1-го этажа

№	Наименование	Площадь	Примечание
1	Тамбур	22,52	
2	Главный холл	354,38	
3	Коридор	78,36	
4	Коридор	9,91	
5	Коридор	9,91	
6	Коридор	9,88	
7	Кладовая	13,78	
8	Тамбур	10,39	
9	Техническое помещение	6,56	
10	Актовый зал	409,88	
11	Коридор	9,35	
12	Помещение для хранения	30,72	
13	С/у	9,30	
14	С/у	5,52	
15	Кладовая	12,36	
16	Лекторий	121,85	
17	Кафе	109,25	
18	Помещение тех. обслуживания	82,52	
19	Зона отдыха	50,38	
20	Коридор	11,15	
21	Тамбур	28,53	
22	Коридор	12,78	
23	Техническое помещение	3,55	
24	С/у	2,58	
25	С/у	11,65	
26	С/у	4,08	
27	Помещение	135,99	
28	Помещение тех. обслуживания	13,70	
29	Кладовая	49,98	
30	Техническое помещение	33,96	
31	Помещение тех. обслуживания	14,80	
32	Техническое помещение	4,16	
33	Техническое помещение	7,46	
34	Техническое помещение	13,74	
35	Техническое помещение	3,75	
Общий итог		1708,69	

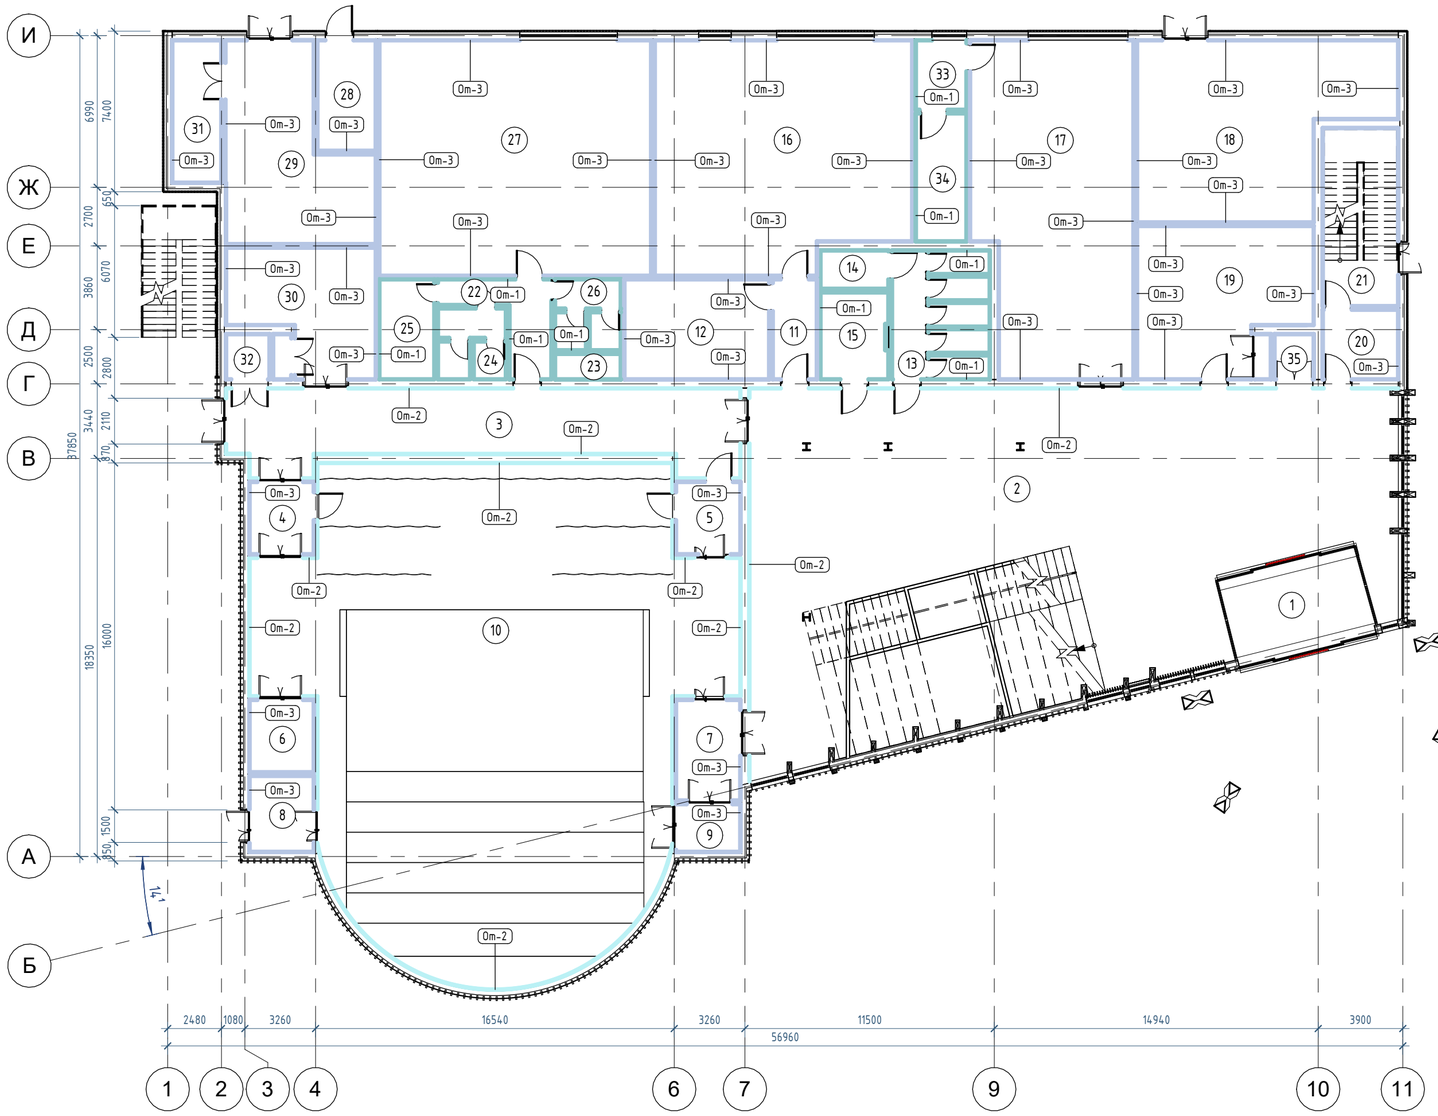

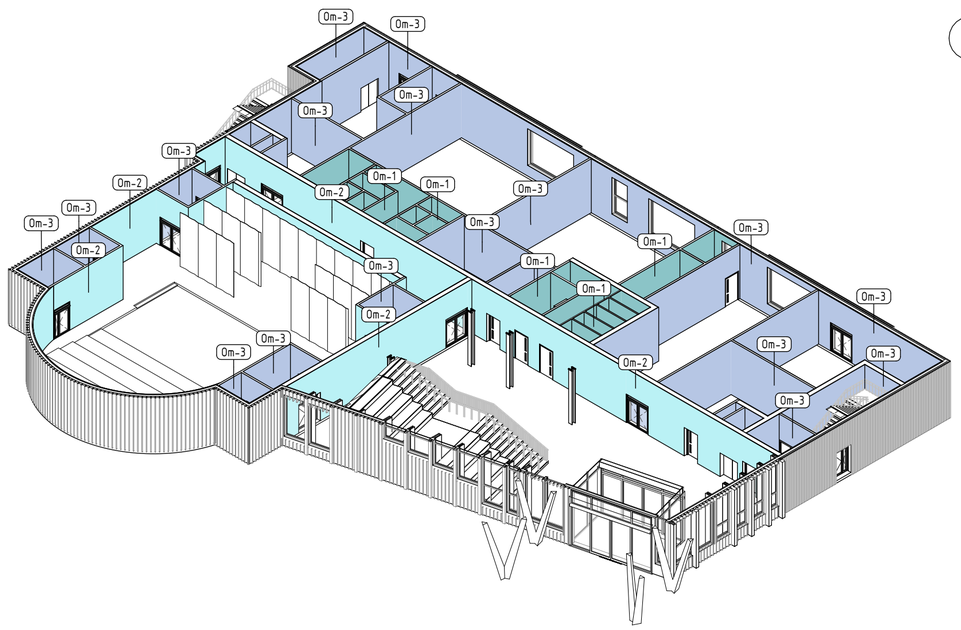

Спецификация отделки стен 1-го этажа

Марка	УО	Описание	S, м2	Примечание
От-1		Плитка керамическая, 250х250	871,90	
От-2		Вагонка хвоя, Штиль 10 мм	869,48	
От-3		Штукатурка белая 10 мм	2199,72	

Условные обозначения

(1) Номер помещения

+0,000 Высотная отметка чистового пола

(От-1) Марка отделки стены

Размеры

Изм.	Кол.уч.	Лист	№док.	Подп.	Дата	Creative Center at York St John University - AP			
Разработал		Шамсиддинов. У				План отделки стен 1-го этажа	Стадия	Лист	Листов
Проверил		Art Brodsky					АР	05	

Формат А2А

Согласовано

Согласовано


Взам. инв. №

Подп. и дата

Инв. № подл.

План напольных покрытий на отм. +0.000
М 1:200

Экспликация помещений 1-го этажа			
№	Наименование	Площадь	Примечание
1	Тамбур	22,52	
2	Главный холл	354,38	
3	Коридор	78,36	
4	Коридор	9,91	
5	Коридор	9,91	
6	Коридор	9,88	
7	Кладовая	13,78	
8	Тамбур	10,39	
9	Техническое помещение	6,56	
10	Актовый зал	409,88	
11	Коридор	9,35	
12	Помещение для хранения	30,72	
13	С/у	9,30	
14	С/у	5,52	
15	Кладовая	12,36	
16	Лекторий	121,85	
17	Кафе	109,25	
18	Помещение тех. обслуживания	82,52	
19	Зона отдыха	50,38	
20	Коридор	11,15	
21	Тамбур	28,53	
22	Коридор	12,78	
23	Техническое помещение	3,55	
24	С/у	2,58	
25	С/у	11,65	
26	С/у	4,08	
27	Помещение	135,99	
28	Помещение тех. обслуживания	13,70	
29	Кладовая	49,98	
30	Техническое помещение	33,96	
31	Помещение тех. обслуживания	14,80	
32	Техническое помещение	4,16	
33	Техническое помещение	7,46	
34	Техническое помещение	13,74	
35	Техническое помещение	3,75	
Общий итог		1708,69	

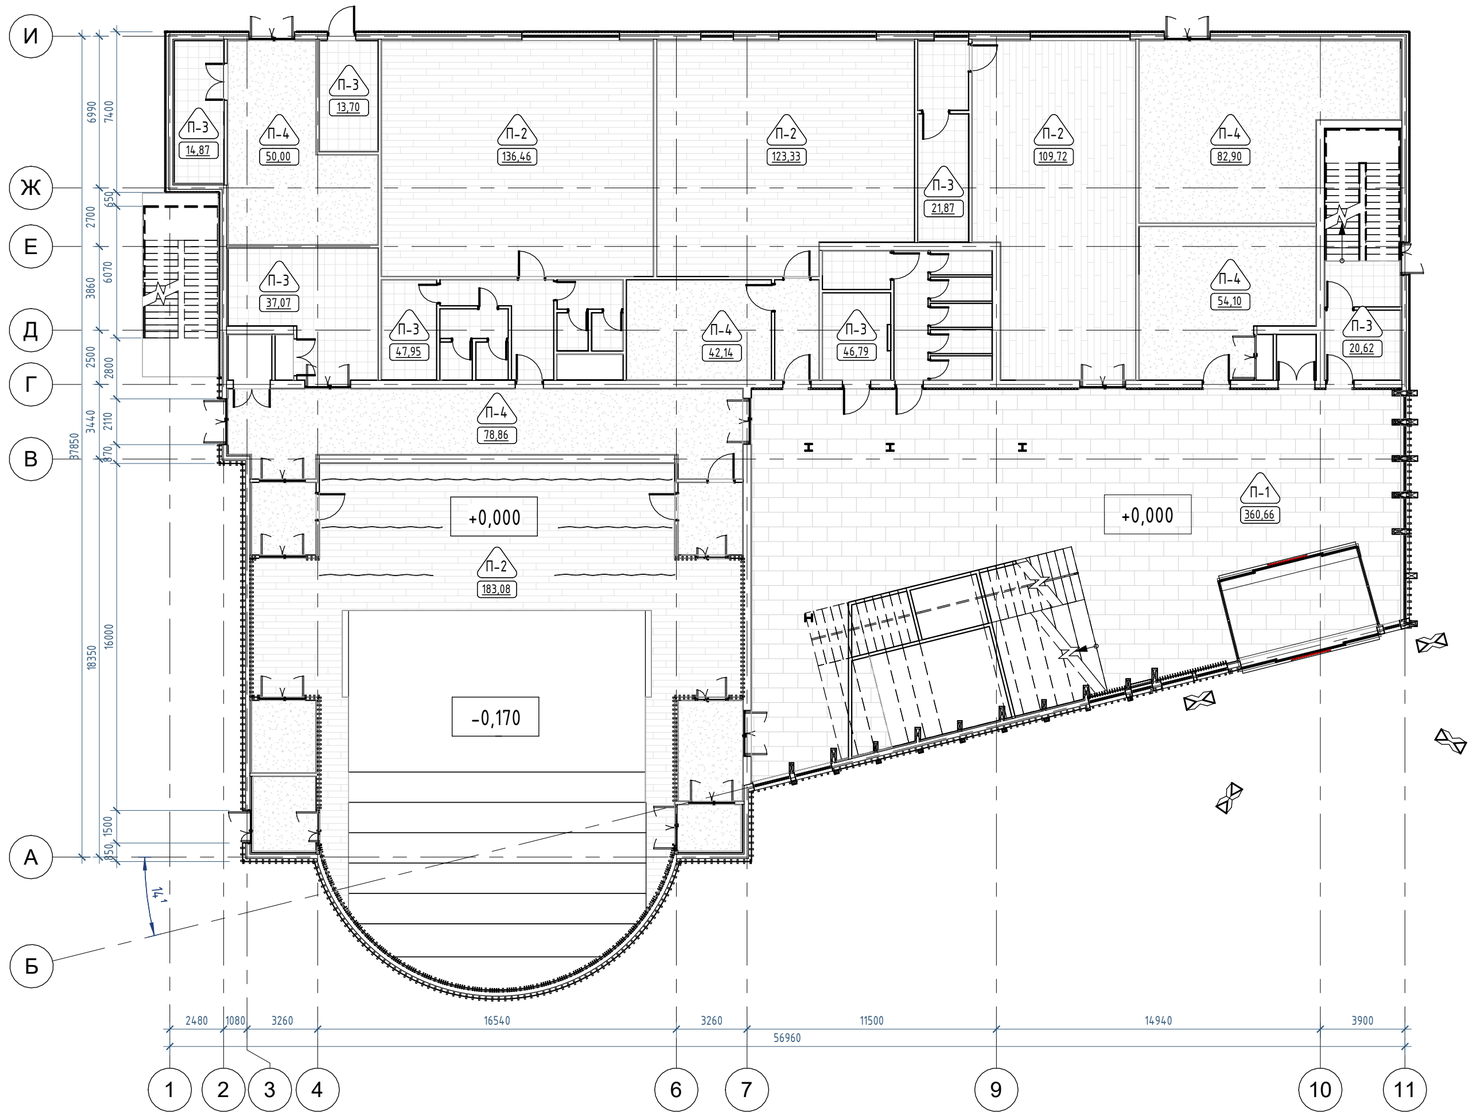

Спецификация перекрытий

УО	Марка	Описание	S, м2	Примечание
	П-1	Паркетная доска, 700х1400 мм	796,03	
	П-2	Паркетная доска, 300х2400 мм	552,59	
	П-3	Керамическая плитка, 500х500 мм	202,87	
	П-4	Эпоксидный наливной пол	368,49	

Примечания

1. Комплект рабочих чертежей разработани на основании обмеров.
2. Обмерные работы выполнялись по существующей предчистовой отделке.
3. Оконные проёмы обмерены по откосу в плоскости стены.
4. Материалы стен показаны условно.
5. Размеры стен и площадей по обмерам могут отличаться не более, чем на 2% (в случае больших расхождений связаться с проектировщиком для принятия решения).
6. Высота помещений первого этажа 5000 мм.

Условные обозначения

П-1 / 344,21 — Марка напольных покрытий

+0,000 — Высотная отметка чистового пола

Размеры

Изм.	Кол.уч.	Лист	№док.	Подп.	Дата	Creative Center at York St John University - AP			
Разработал		Шамсиддинов. У				План напольных покрытий на отм. +0,000	Стадия	Лист	Листов
Проверил		Art Brodsky					АР	06	

Формат А2А

Согласовано

Согласовано


Взам. инв. №

Подп. и дата

Инв. № подл.


Планы размещения сантехнического оборудования 1-го этажа

Экспликация помещений 1-го этажа			
№	Наименование	Площадь	Примечание
1	Тамбур	22,52	
2	Главный холл	354,38	
3	Коридор	78,36	
4	Коридор	9,91	
5	Коридор	9,91	
6	Коридор	9,88	
7	Кладовая	13,78	
8	Тамбур	10,39	
9	Техническое помещение	6,56	
10	Актовый зал	409,88	
11	Коридор	9,35	
12	Помещение для хранения	30,72	
13	С/у	9,30	
14	С/у	5,52	
15	Кладовая	12,36	
16	Лекторий	121,85	
17	Кафе	109,25	
18	Помещение тех. обслуживания	82,52	
19	Зона отдыха	50,38	
20	Коридор	11,15	
21	Тамбур	28,53	
22	Коридор	12,78	
23	Техническое помещение	3,55	
24	С/у	2,58	
25	С/у	11,65	
26	С/у	4,08	
27	Помещение	135,99	
28	Помещение тех. обслуживания	13,70	
29	Кладовая	49,98	
30	Техническое помещение	33,96	
31	Помещение тех. обслуживания	14,80	
32	Техническое помещение	4,16	
33	Техническое помещение	7,46	
34	Техническое помещение	13,74	
35	Техническое помещение	3,75	
Общий итог		1708,69	

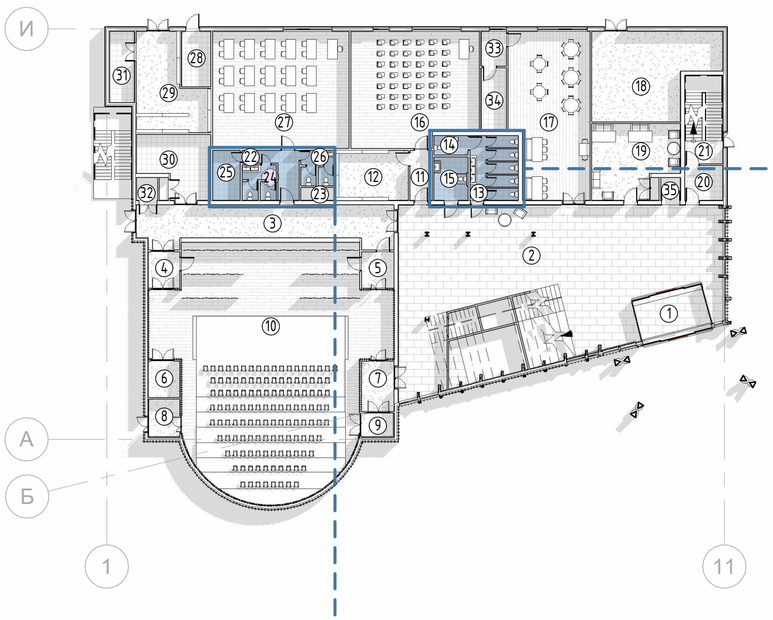


План размещения сантехнического оборудования 1 на отм. +0,000

М 1:50

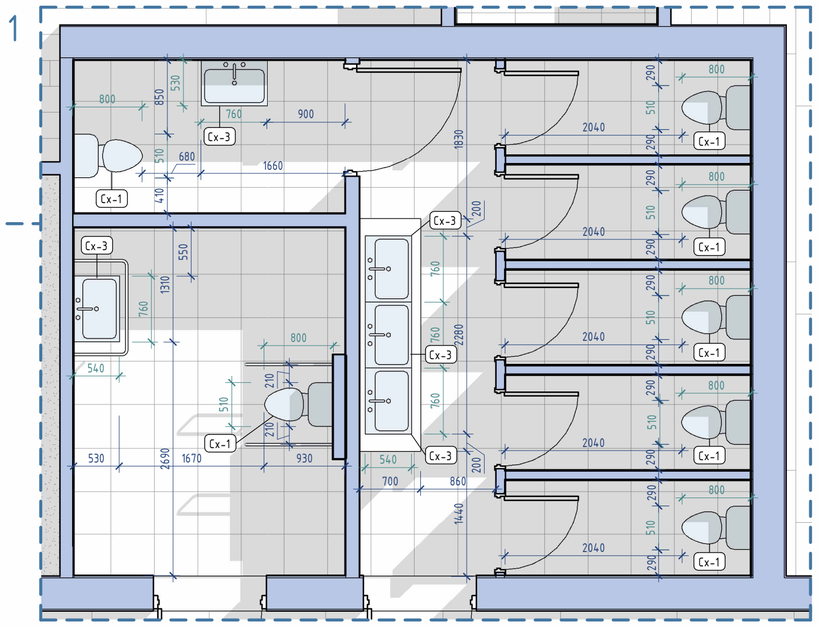

План размещения сантехнического оборудования 2 на отм. +0,000

М 1:50

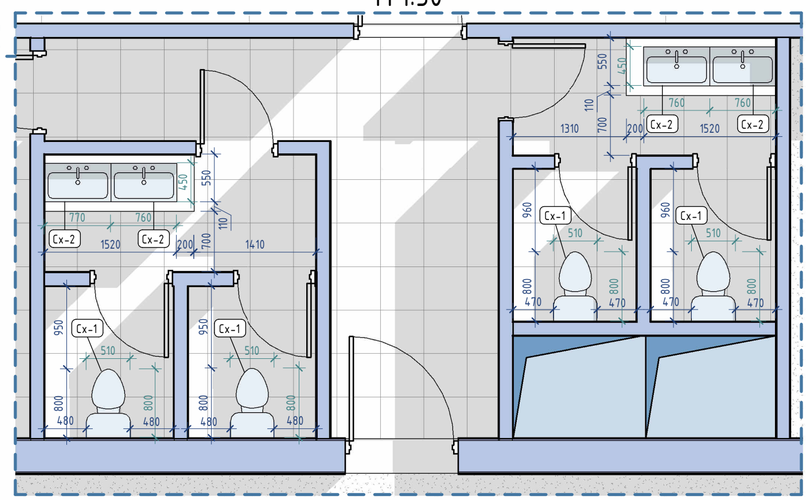


Условные обозначения


(1) Номер помещения

Сх-1 Марка сантехнических приборов

Размеры сантехнических приборов

Расположение сантехнических приборов

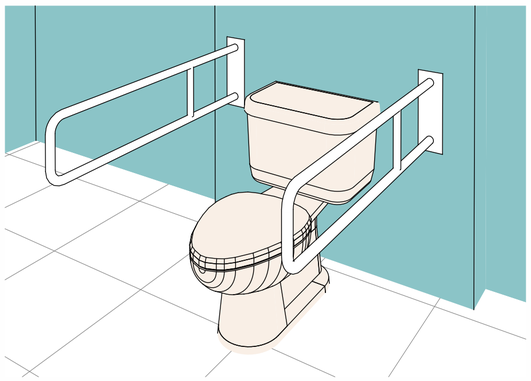

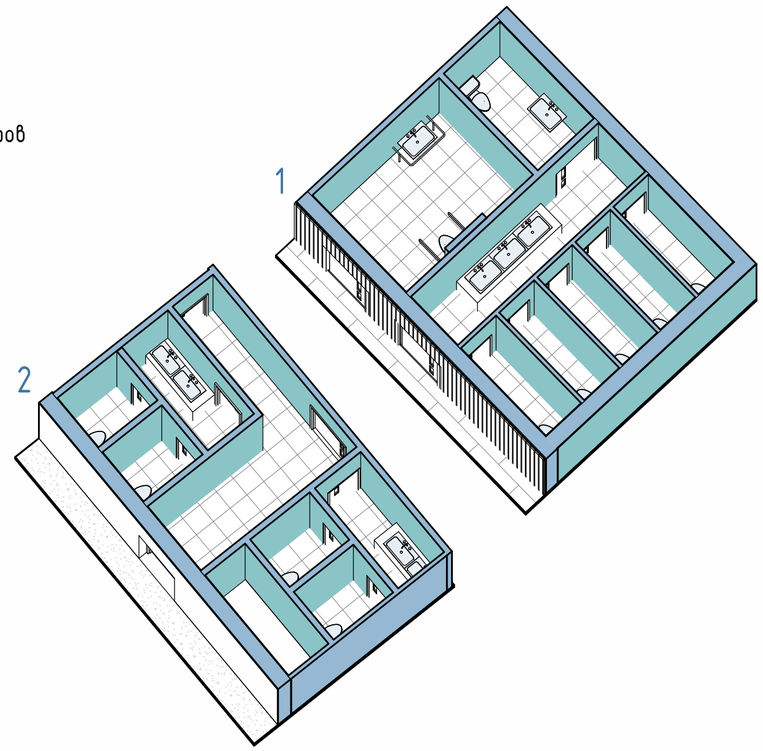

Спецификация сантехнических приборов

Марка	Описание	Количество
Сх-1	Унитаз	11
Сх-2	Раковина 760х450 мм	4
Сх-3	Раковина 760х540 мм	5

Изм.	Кол.уч.	Лист	№док.	Подп.	Дата	Creative Center at York St John University - AP			
Разработал		Шамсиддинов. У				Планы размещения сантехнического оборудования 1-го этажа	Стадия	Лист	Листов
Проверил		Art Brodsky					АР	07	

Формат А2А

Согласовано

Согласовано

Взам. инв. №

Подп. и дата

Инв. № подл.


План расстановки осветительного оборудования 1-го этажа
М 1:200

Экспликация помещений 1-го этажа

№	Наименование	Площадь	Примечание
1	Тамбур	22,52	
2	Главный холл	354,38	
3	Коридор	78,36	
4	Коридор	9,91	
5	Коридор	9,91	
6	Коридор	9,88	
7	Кладовая	13,78	
8	Тамбур	10,39	
9	Техническое помещение	6,56	
10	Актовый зал	409,88	
11	Коридор	9,35	
12	Помещение для хранения	30,72	
13	С/у	9,30	
14	С/у	5,52	
15	Кладовая	12,36	
16	Лекторий	121,85	
17	Кафе	109,25	
18	Помещение тех. обслуживания	82,52	
19	Зона отдыха	50,38	
20	Коридор	11,15	
21	Тамбур	28,53	
22	Коридор	12,78	
23	Техническое помещение	3,55	
24	С/у	2,58	
25	С/у	11,65	
26	С/у	4,08	
27	Помещение	135,99	
28	Помещение тех. обслуживания	13,70	
29	Кладовая	49,98	
30	Техническое помещение	33,96	
31	Помещение тех. обслуживания	14,80	
32	Техническое помещение	4,16	
33	Техническое помещение	7,46	
34	Техническое помещение	13,74	
35	Техническое помещение	3,75	
Общий итог		1708,69	

Спецификация осветительных приборов

Марка	Изображение	Описание	Количество
Ос-1		Светильник потолочный, круглый	161
Ос-2		Светильник студийный	76
Ос-3		Подвесной светильник на 3 лампы	39
Ос-4		Светильник потолочный, прямоугольный	25

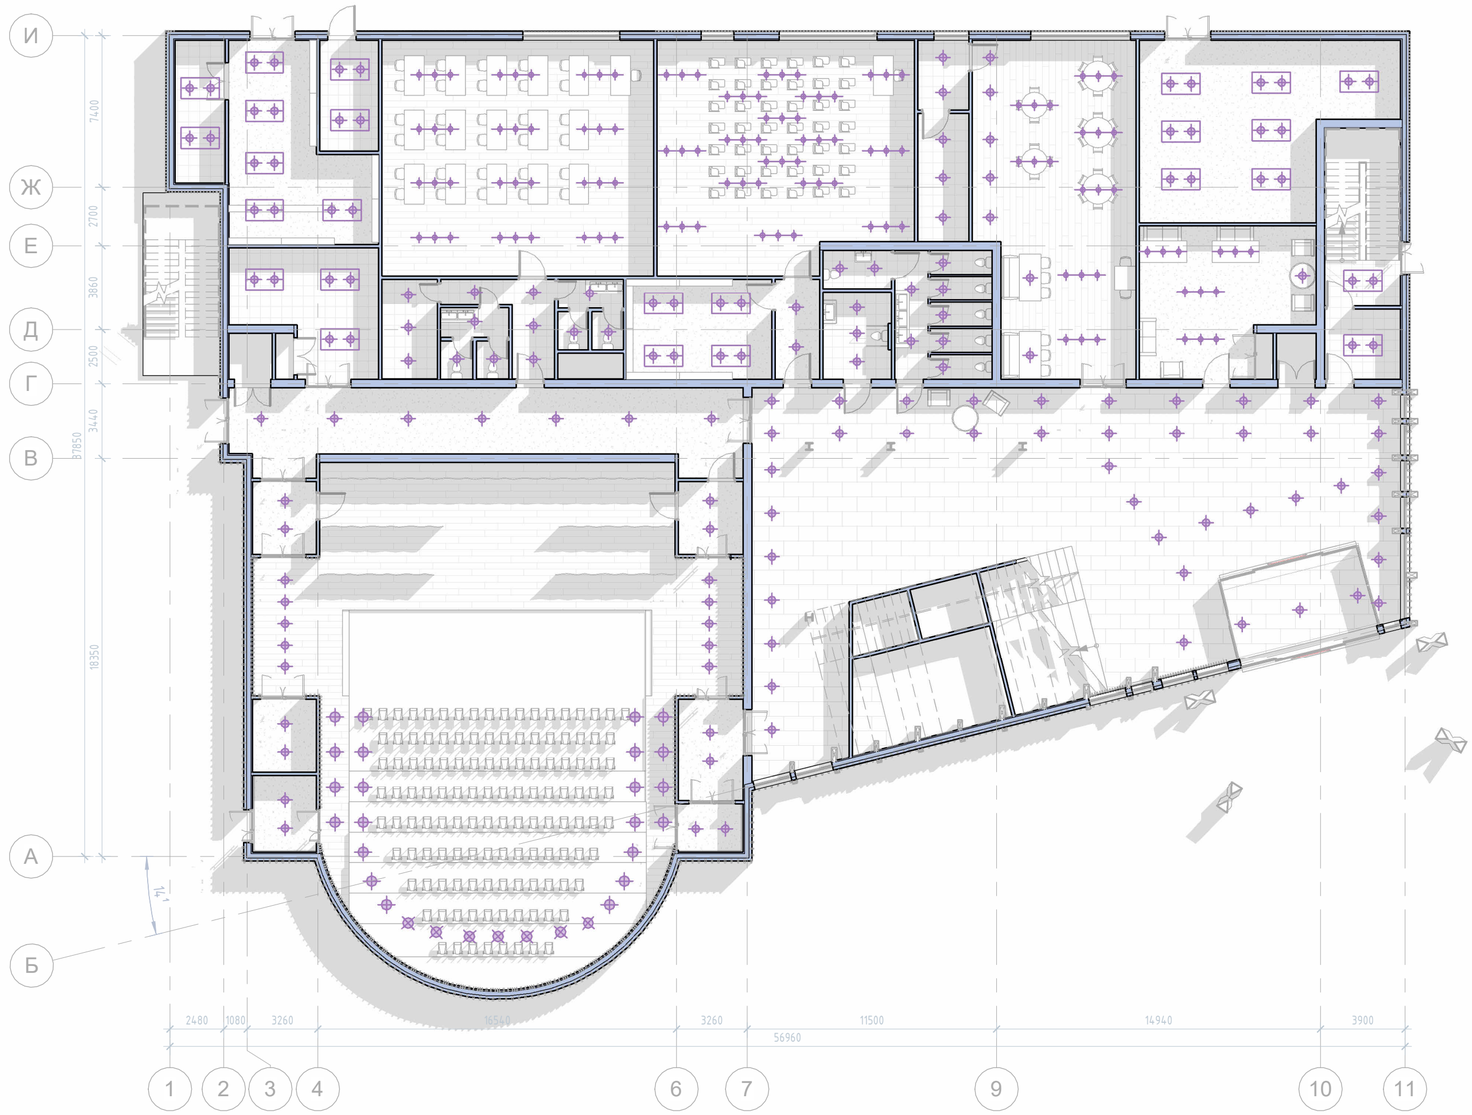

Примечания

1. Комплект рабочих чертежей разработани на основании обмеров.
2. Обмерные работы выполнялись по существующей предчистовой отделке.
3. Оконные проёмы обмерены по откосу в плоскости стены.
4. Материалы стен показаны условно.
5. Размеры стен и площадей по обмерам могут отличаться не более, чем на 2% (в случае больших расхождений связаться с проектировщиком для принятия решения).
6. Высота помещений первого этажа 5000 мм.

Условные обозначения

Осветительный прибор

Размеры

Изм.	Кол.уч.	Лист	№док.	Подп.	Дата	Creative Center at York St John University - AP			
Разработал		Шамсиддинов. У				План расстановки осветительного оборудования 1-го этажа	Стадия	Лист	Листов
Проверил		Art Brodsky					АР	08	

Формат А2А

Согласовано

Согласовано

Взам. инв. №

Подп. и дата


Инв. № подл.

План маркировки дверных проёмов 1-го этажа


М 1:200





Экспликация помещений 1-го этажа

№	Наименование	Площадь	Примечание
1	Тамбур	22,52	
2	Главный холл	354,38	
3	Коридор	78,36	
4	Коридор	9,91	
5	Коридор	9,91	
6	Коридор	9,88	
7	Кладовая	13,78	
8	Тамбур	10,39	
9	Техническое помещение	6,56	
10	Актовый зал	409,88	
11	Коридор	9,35	
12	Помещение для хранения	30,72	
13	С/у	9,30	
14	С/у	5,52	
15	Кладовая	12,36	
16	Лекторий	121,85	
17	Кафе	109,25	
18	Помещение тех. обслуживания	82,52	
19	Зона отдыха	50,38	
20	Коридор	11,15	
21	Тамбур	28,53	
22	Коридор	12,78	
23	Техническое помещение	3,55	
24	С/у	2,58	
25	С/у	11,65	
26	С/у	4,08	
27	Помещение	135,99	
28	Помещение тех. обслуживания	13,70	
29	Кладовая	49,98	
30	Техническое помещение	33,96	
31	Помещение тех. обслуживания	14,80	
32	Техническое помещение	4,16	
33	Техническое помещение	7,46	
34	Техническое помещение	13,74	
35	Техническое помещение	3,75	
Общий итог		1708,69	

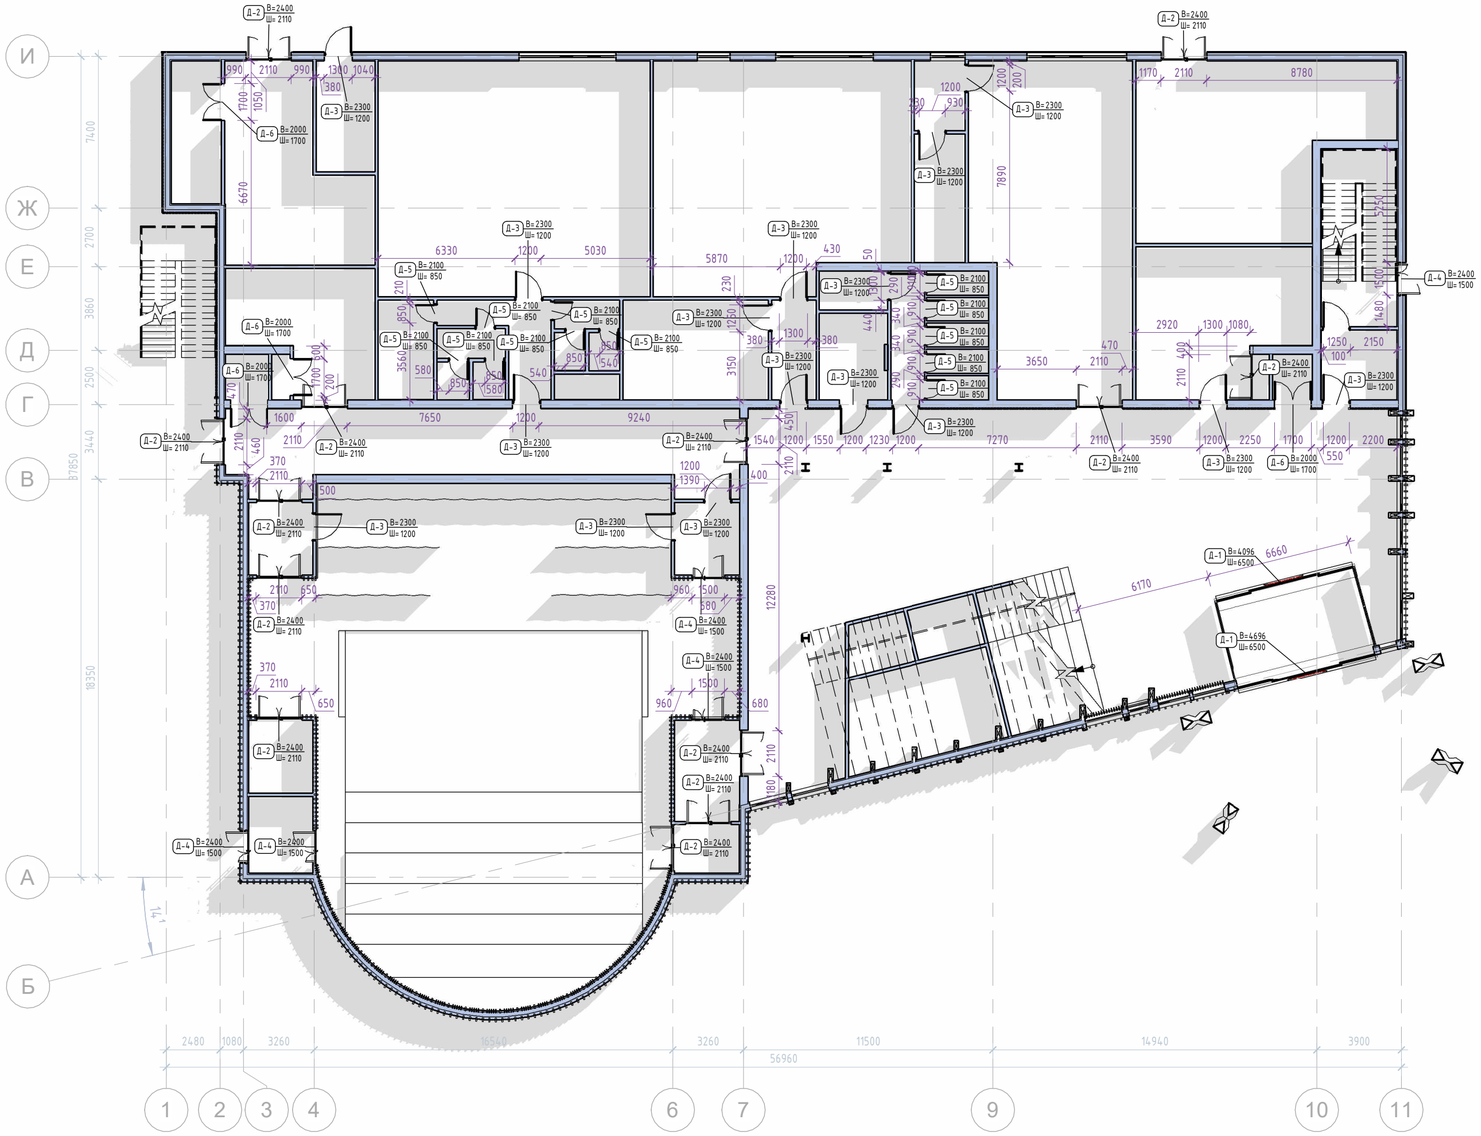

Условные обозначения

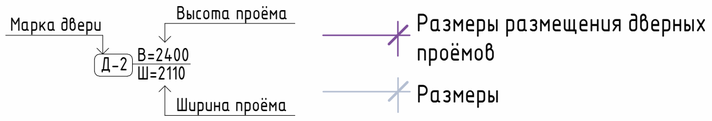

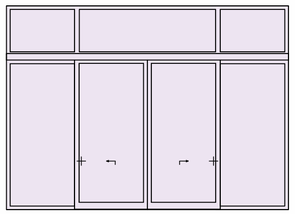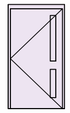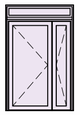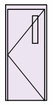Марка	Д-1	Д-2	Д-3	Д-4	Д-5	Д-6
Описание	Дверь входная остеклённая	Дверь двойная	Дверь маятниковая одинарная, с двумя окошками	Дверь полуторная	Дверь маятниковая, с одним окошком	Дверь двойная, щитовая
Схема фасада						
Схема на плане						

Спецификация дверных проёмов 1-го этажа

Марка	Описание	Габариты		Количество
		Высота	Ширина	
Д-1	Дверь входная остеклённая	<варианты>	6500	2
Д-2	Дверь двойная	2400	2110	18
Д-3	Дверь маятниковая одинарная, с двумя окошками	2300	1200	54
Д-4	Дверь полуторная	2400	1500	7
Д-5	Дверь маятниковая, с одним окошком	2100	850	27
Д-6	Дверь двойная, щитовая	2000	1700	10
Д-7		2100	1200	2

Изм.	Кол.уч.	Лист	№док.	Подп.	Дата	Creative Center at York St John University - AP			
Разработал		Шамсиддинов. У				План маркировки дверных проёмов 1-го этажа	Стадия	Лист	Листов
Проверил		Art Brodsky					AP	09	

Формат А2А

Согласовано


Согласовано


Взам. инв. №

Подп. и дата

Инв. № подл.

Аксонометрия актового зала, развёртки по актовому залу

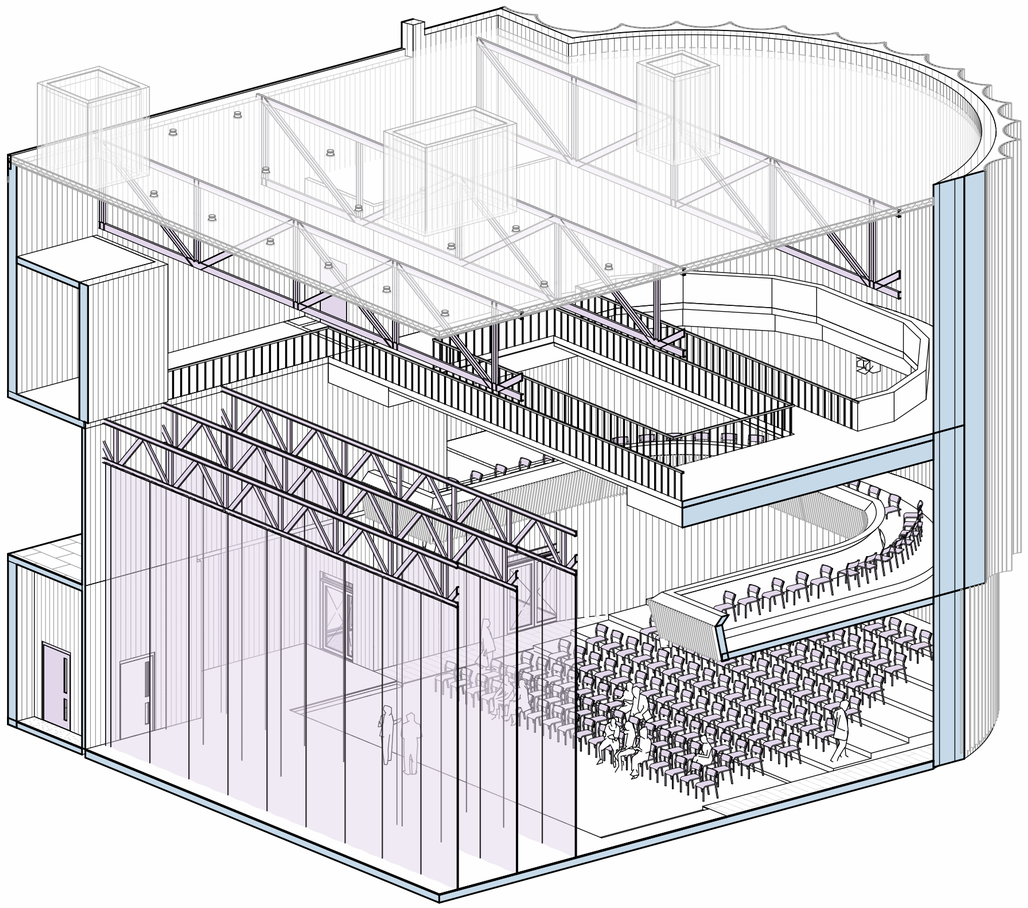

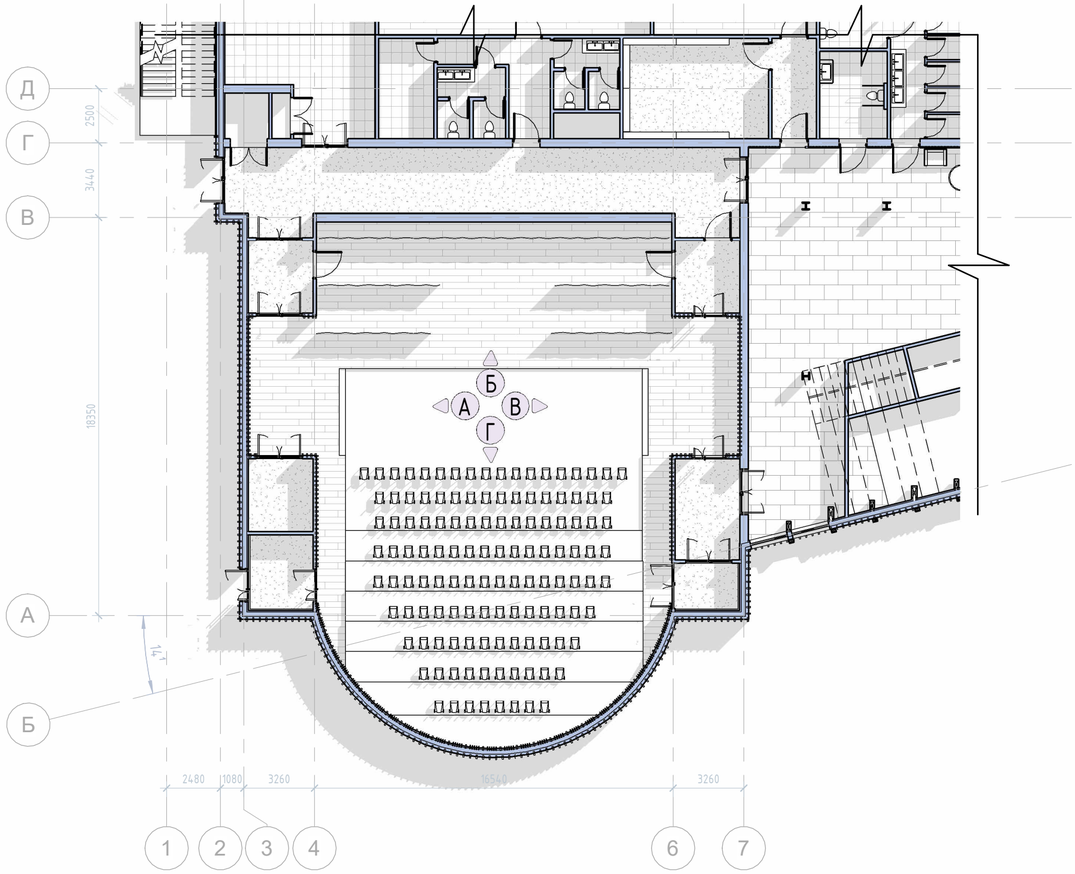


Условные обозначения


Марка двери — Д-2 — Высота проёма В=2400 / Ширина проёма Ш=2110

Размеры в интерьере

Размеры

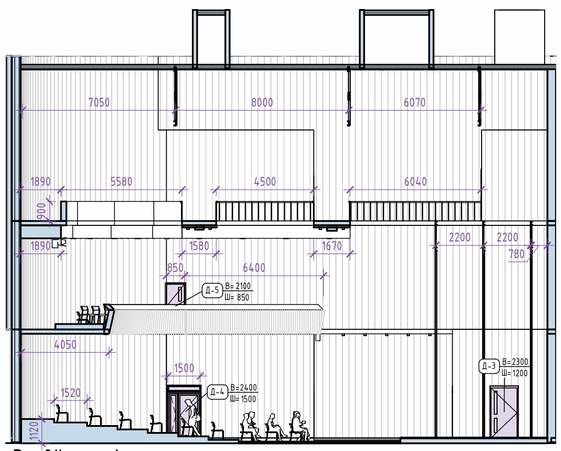


Развёртка А
М 1:200

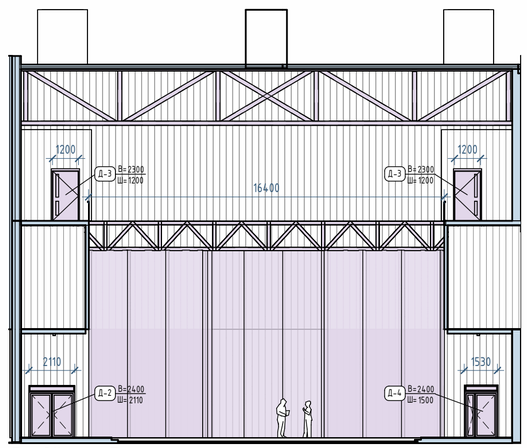

Развёртка Б
М 1:200



Развёртка В
М 1:200

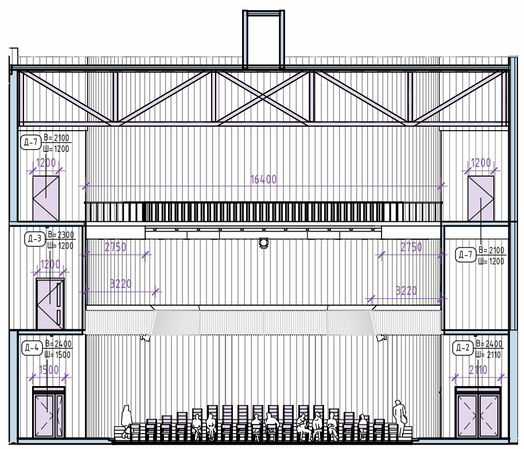

Развёртка Г
М 1:200

Изм.	Кол.уч.	Лист	№док.	Подп.	Дата	Creative Center at York St John University - AP		
Разработал		Шамсиддинов. У				Аксонометрия актового зала, развёртки по актовому залу	Стадия	Лист	Листов
Проверил		Art Brodsky					AP	10	

Формат А2А

Согласовано


Согласовано

Взам. инв. №


Подп. и дата

Инв. № подл.


Аксонометрия разреза

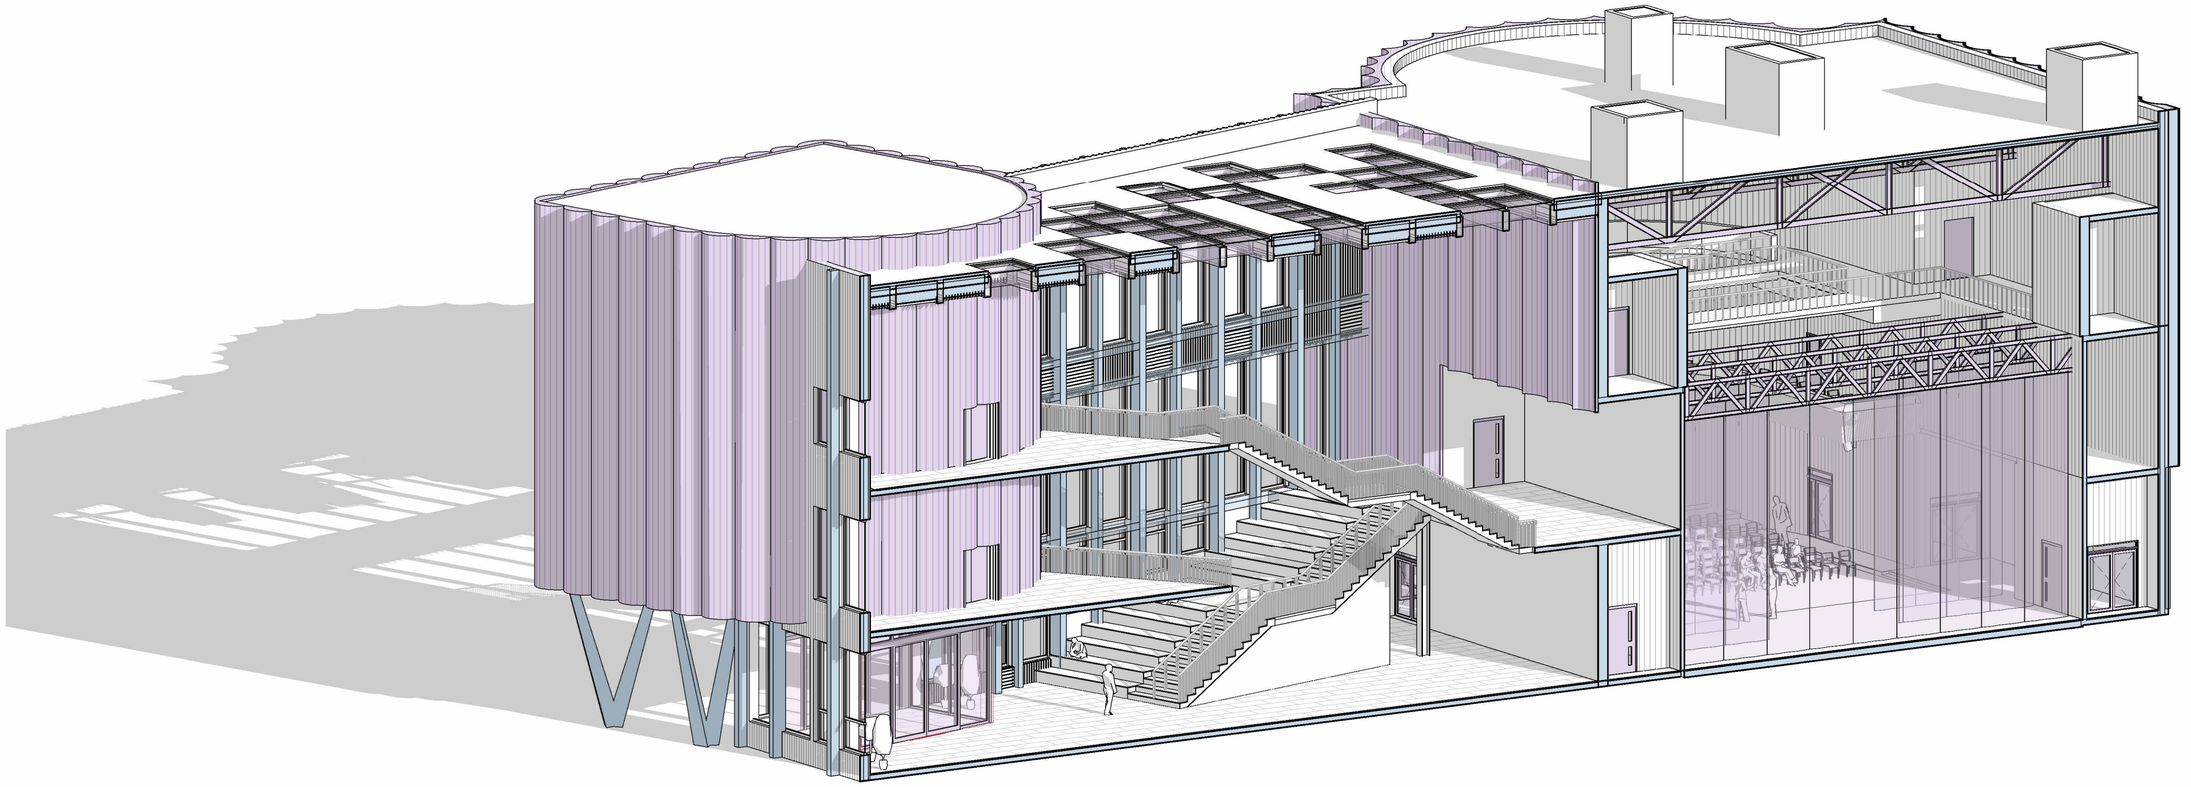

Разрез 1-1

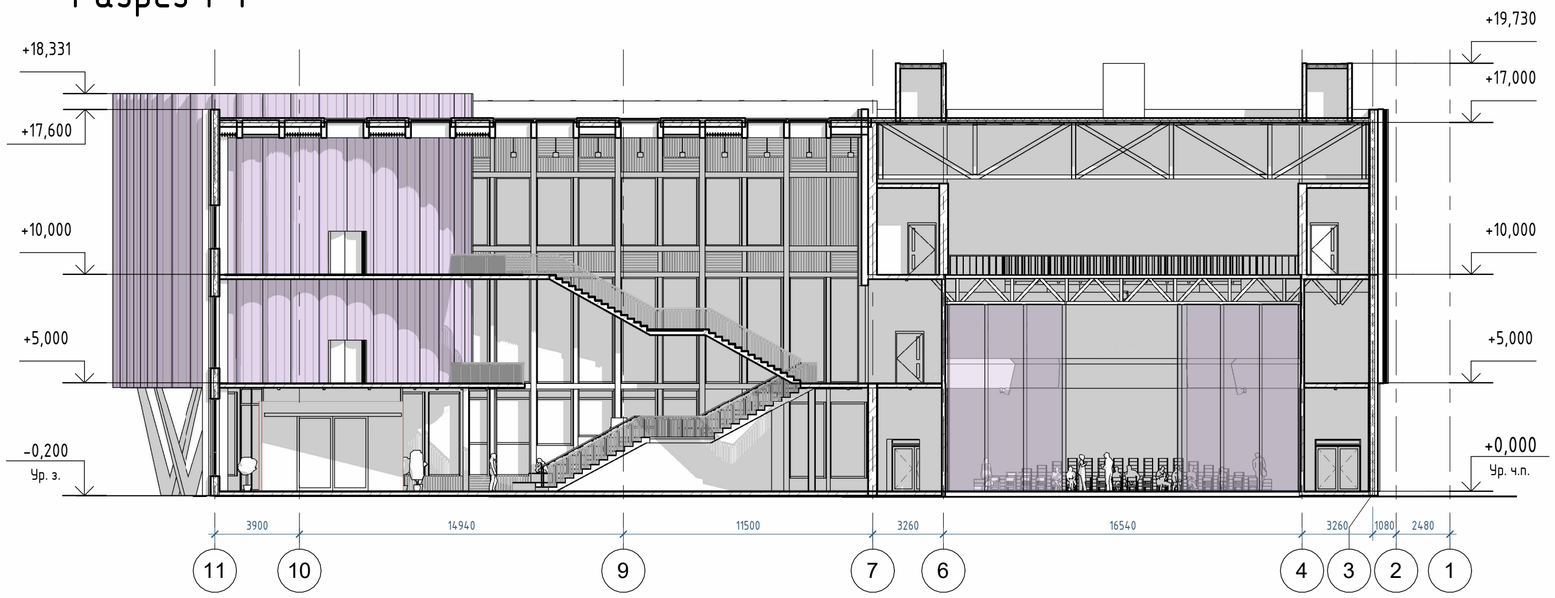

Аксонометрия лестницы

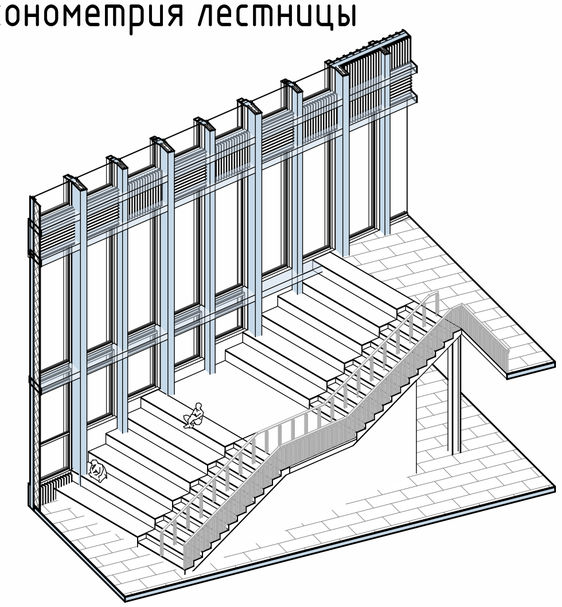

Изм.	Кол.уч.	Лист	№док.	Подп.	Дата	Creative Center at York St John University - AP			
Разработал		Шамсиддинов. У				Разрез 1-1, Аксонометрия разреза, аксонометрия лестницы	Стадия	Лист	Листов
Проверил		Art Brodsky					АР	11	

Формат А2А

Согласовано


Согласовано

Взам. инв. №

Подп. и дата

Инв. № подл.

Фасад 1-11
М 1:200

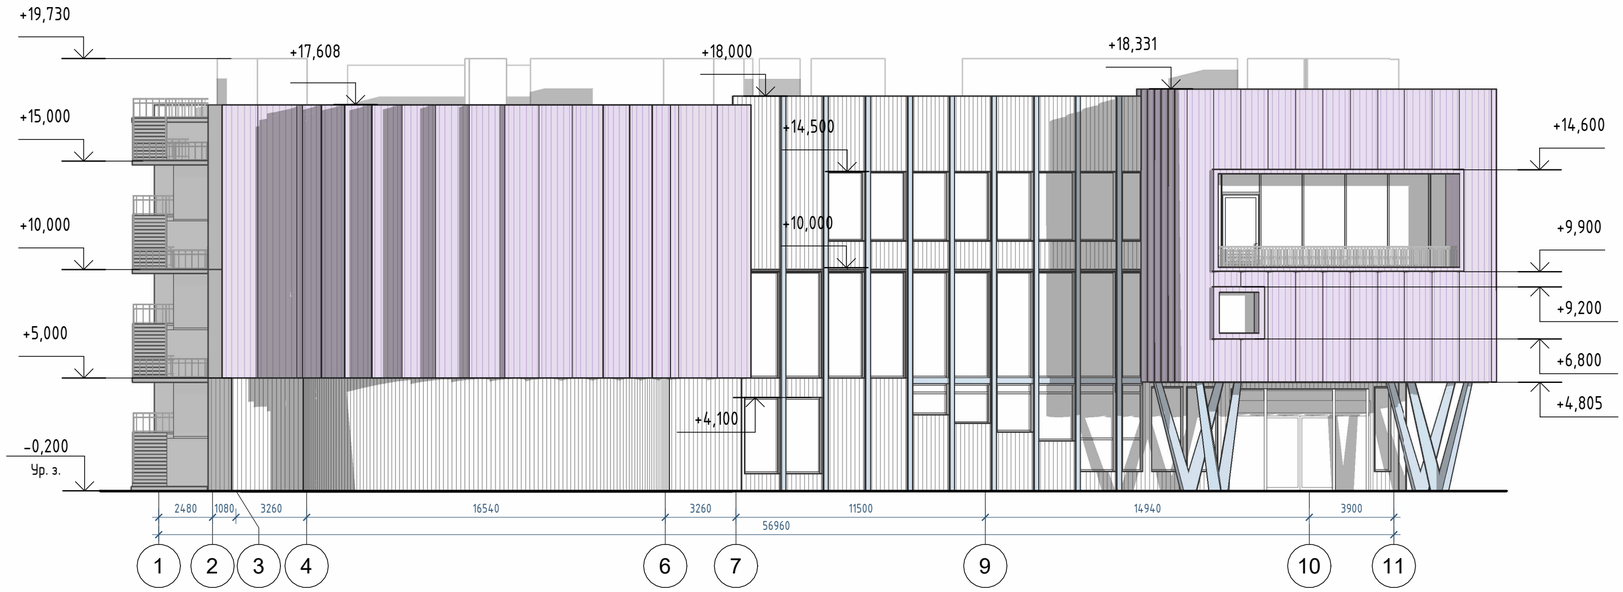

Фасад 11-1
м 1:200



Изм.	Кол.уч.	Лист	№док.	Подп.	Дата	Creative Center at York St John University - AP			
Разработал		Шамсиддинов. У				Фасад 1-11 М 1 к 200, фасад 11-1 М 1 к 200	Стадия	Лист	Листов
Проверил		Art Brodsky					AP	12	

Формат А2А

Согласовано


Согласовано

Взам. инв. №

Подп. и дата

Инв. № подл.

Фасад А-И
М 1:200

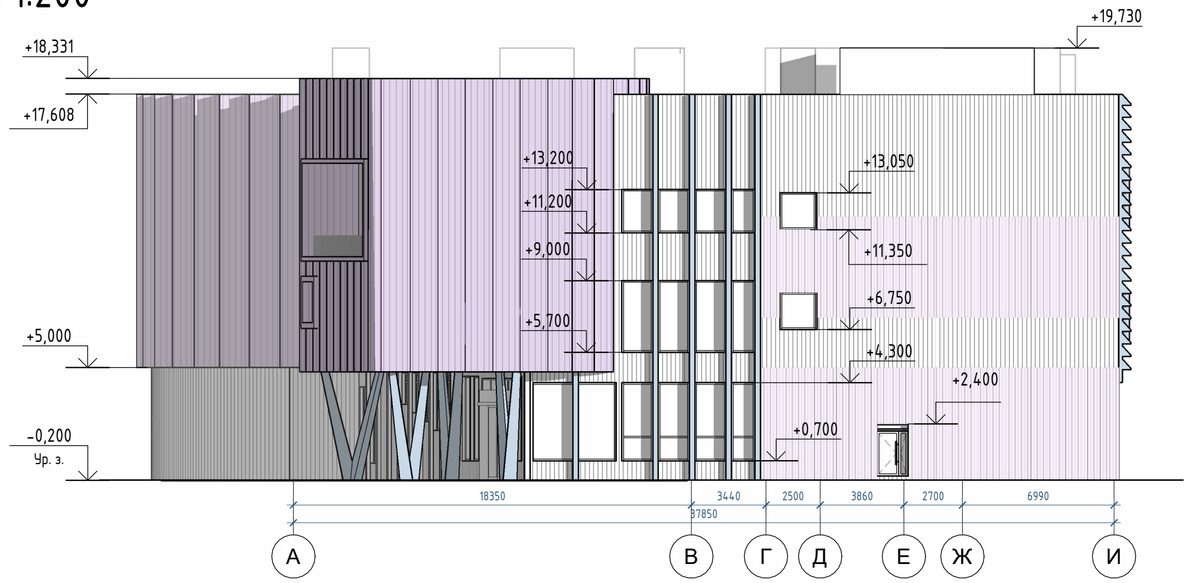

Фасад И-А
М 1:200



Согласовано

Согласовано

Взам. инв. №

Подп. и дата

Инв. № подл.

Изм.	Кол.уч.	Лист	№док.	Подп.	Дата	Creative Center at York St John University - AP			
Разработал		Шамсиддинов. У				Фасад А-И М 1 к 200, фасад И-А М 1 к 200	Стадия	Лист	Листов
Проверил		Art Brodsky					АР	13	


Формат А2А

Аксонометрия здания
М 1:500





Взрыв-схема
М 1:400

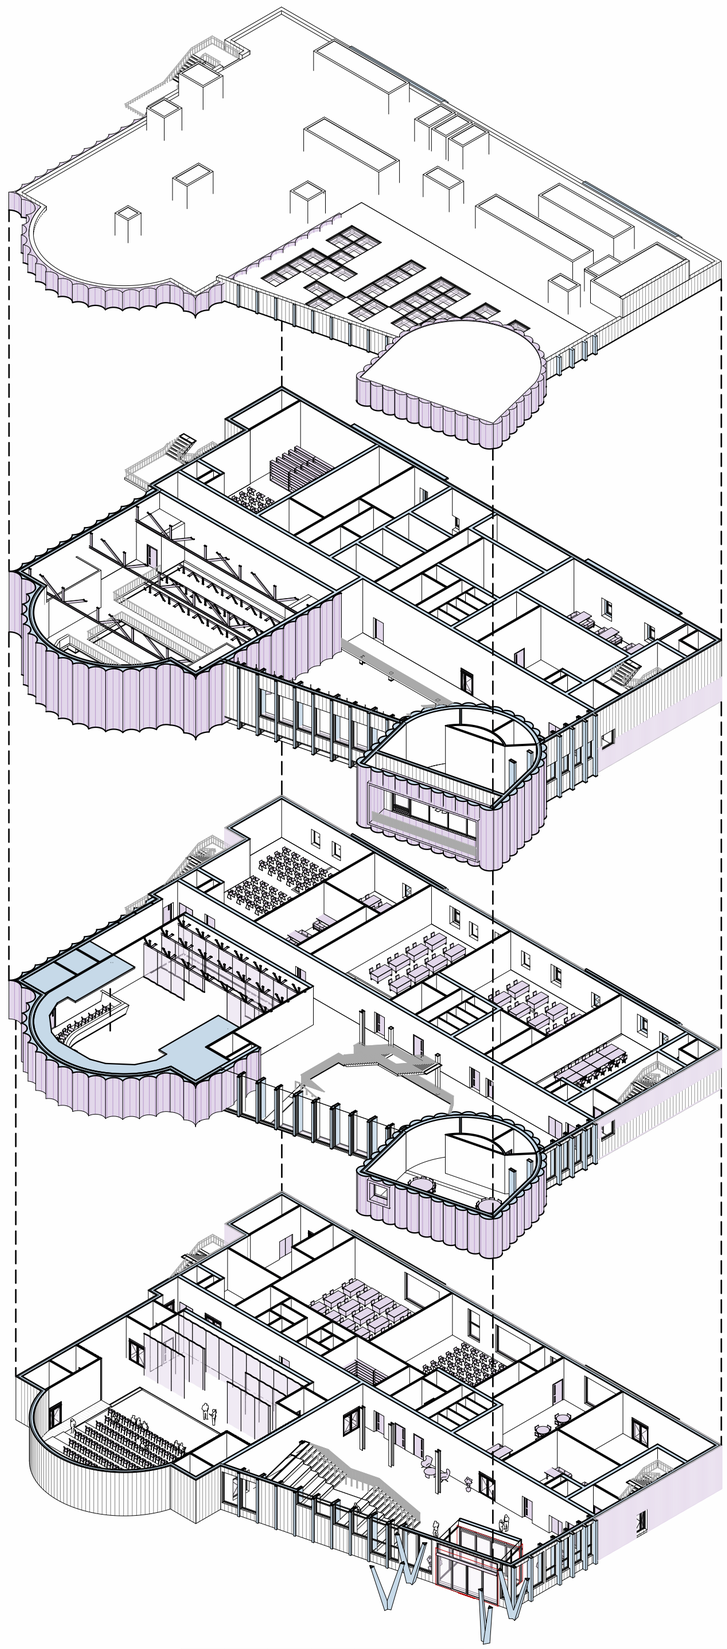

Согласовано

Согласовано

Взам. инв. №


Подп. и дата

Инв. № подл.


Изм.	Кол.уч.	Лист	№док.	Подп.	Дата	Creative Center at York St John University - AP		
Разработал		Шамсиддинов. У				Аксонометрия здания, взрыв-схема	Стадия	Лист	Листов
Проверил		Art Brodsky					АР	14	

Формат А2А

Перспективные виды

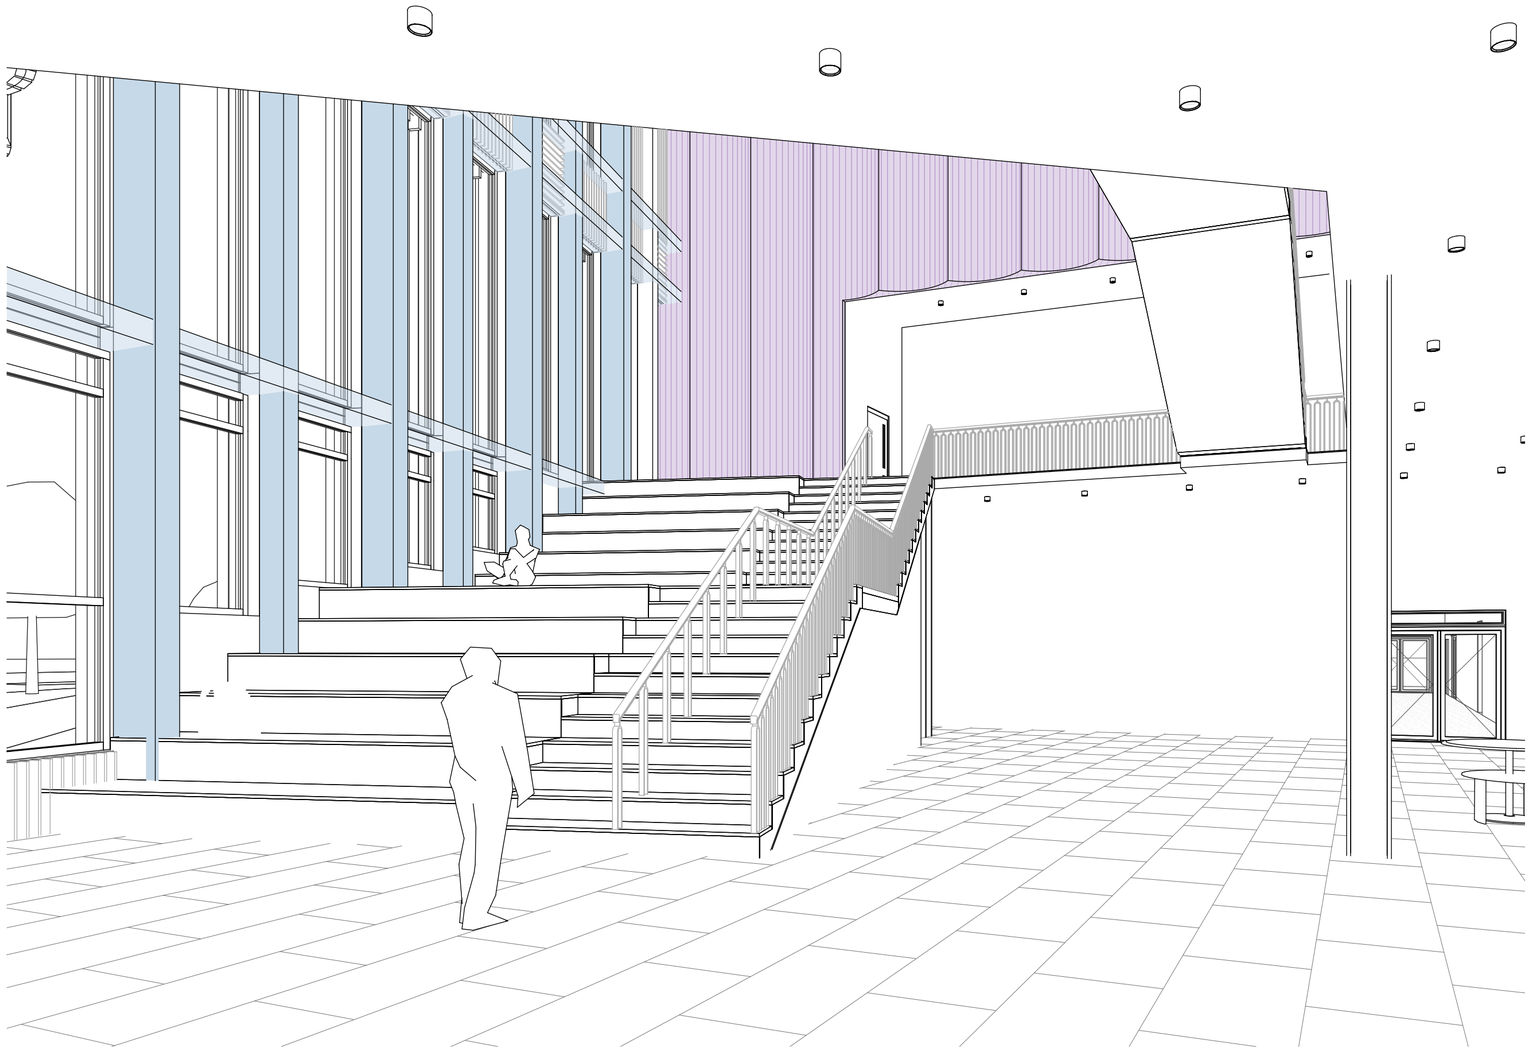



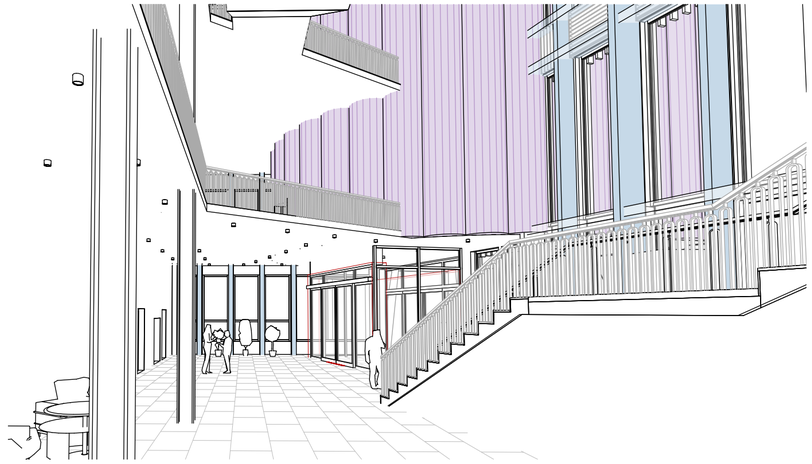

Согласовано

Согласовано

Взам. инв. №

Подп. и дата

Инв. № подл.

Изм.	Кол.уч.	Лист	№док.	Подп.	Дата	Creative Center at York St John University - AP		
Разработал		Шамсиддинов. У				Перспективные виды	Стадия	Лист	Листов
Проверил		Art Brodsky					AP	15	

Формат A2A