Ведомость рабочих чертежей основного комплекта

Лист	Наименование	Примечание
1	ОБЩИЕ ДАННЫЕ	
2	ПОЯСНИТЕЛЬНАЯ ЗАПИСКА	
3	ОБМЕРНЫЙ ПЛАН	
4	ПЛАН ДЕМОНТАЖА	
5	ПЛАН МОНТАЖА ПЕРЕГОРОДОК, 1 этап	
6	ПЛАН МОНТАЖА ГК-конструкций. 2 этап	
7	ОБМЕРНЫЙ ПЛАН ПОСЛЕ МОНТАЖА	
8	ПЛАН РАССТАНОВКИ МЕБЕЛИ С РАЗМЕРАМИ	
9	ПЛАН РАССТАНОВКИ МЕБЕЛИ	
10	ПЛАН ЗАПОЛНЕНИЯ ПРОЕМОВ	
11	ПЛАН ПОДВОДА КОММУНИКАЦИЙ	
12	ПЛАН РАДИАТОРОВ	
13	ПЛАН НАПОЛЬНЫХ ПОКРЫТИЙ	
14	ПЛАН РАСПОЛОЖЕНИЯ ПЛИНТУСА	
15	ПЛАН ТЕПЛОГО ПОЛА	
16	ПЛАН ПОТОЛКА	
17	ПЛАН РАСПОЛОЖЕНИЯ ТЕНЕВОГО ЗАЗОРА	
18	ПЛАН РАССТАНОВКИ ОСВЕТИТЕЛЬНОГО ОБОРУДОВАНИЯ	
19	ПЛАН МАРКИРОВКА ОСВЕТИТЕzЛЬНОГО ОБОРУДОВАНИЯ	
20	СПЕЦИФИКАЦИЯ ОСВЕТИТЕЛЬНОГО ОБОРУДОВАНИЯ	
21	ПЛАН ВЕНТИЛЯЦИИ	
22	ПЛАН УПРАВЛЕНИЯ СВЕТОМ	
23	ПЛАН РОЗЕТОК	
24	ПЛАН ОТДЕЛКИ СТЕН	
25	ПЛАН РАЗВЕРТОК	
26	РАЗВЕРТКИ пом. № 1, Прихожая	
27	РАЗВЕРТКИ пом. № 2, Гостиная	

Ведомость рабочих чертежей основного комплекта

Лист	Наименование	Примечание
28	РАЗВЕРТКИ пом. № 2, Кухня	
29	РАЗВЕРТКИ пом. № 3, Сальня	
30	РАЗВЕРТКИ пом. № 4, Санузел	


ОБЩИЕ ДАННЫЕ

№ проекта	Раздел	Стадия	Лист	Листов
	АИ	РП	1	

1. В проекте заложены монтажные стены из ГК-конструкций. Строительной бригадой, при необходимости, могут быть заменены на другие с согласованием заказчика.
2. Опуски потолков зависят от минимальной высоты, необходимой для монтажа светильников и системы вытяжной вентиляции. При возможности нужно максимально поднять высоту помещений.
3. В проекте заложены межкомнатные двери СО СКРЫТЫМ КОРОБОМ.
4. Систему канализации нужно пересмотреть со специалистом на соответствие необходимым уклонам к канализационным стоякам.
5. В проекте заложен стык пола и стен по скрытому плинтусу с покраской в черный цвет.
6. В проекте заложен стык потолка и стен по алюминиевому профилю 12х12 мм, монтируемому в стену.
7. Выводы под кухню уточнить после заказа кухни и получения ТЗ.
8. Система кондиционирования – приточно-вытяжная система с центральным блоком. Вентиляцию зоны спален уточнить согласно проекту кондиционирования.
9. Предусмотреть размещение системы фильтрации.
10. Плитку в санузлах на углах нужно укладывать без уголков, с подрезкой под 45 градусов.
11. Точную высоту стяжки пола согласовать после подбора и утверждения напольных покрытий.

ПОЯСНИТЕЛЬНАЯ ЗАПИСКА

№ проекта	Раздел	Стадия	Лист	Листов
	АИ	РП	2	

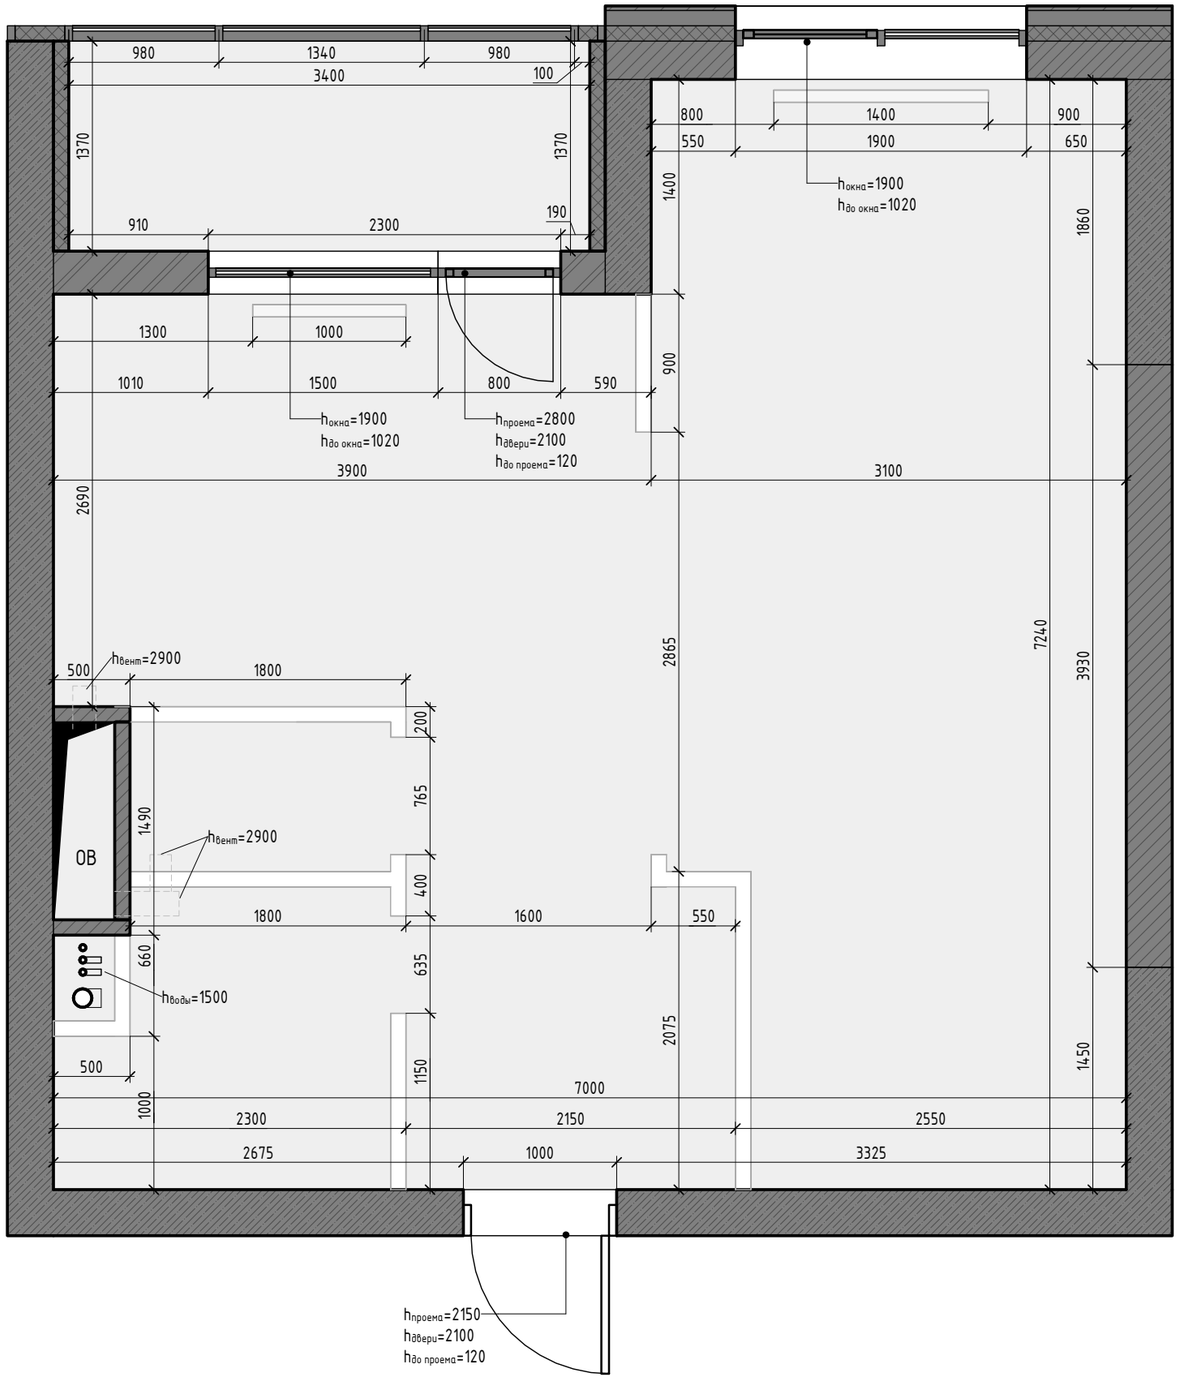

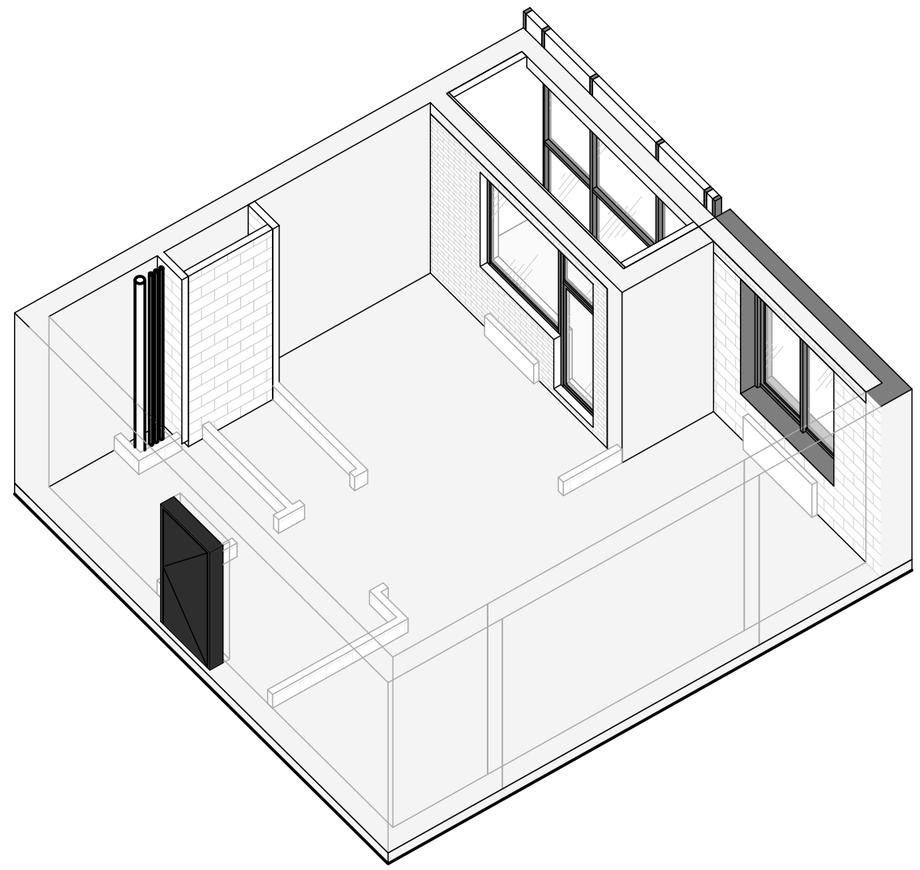


Схема существующей ситуации

Условные обозначения:

- Монолитный Ж/Б
- Пеноблок
- ОВ — Шахта обменной вентиляции
- Существующие радиаторы

Примечания:

1. Высота потолков 3204-3220 мм, усредненная равна 3210мм.
2. Размеры и высоты указаны в мм.
3. Допустимая погрешность 10-50 мм, в зависимости от кривизны стен и измерений лазерной рулетки.

ОБМЕРНЫЙ ПЛАН

№ проекта	Раздел	Стадия	Лист	Листов
	АИ	РП	3	


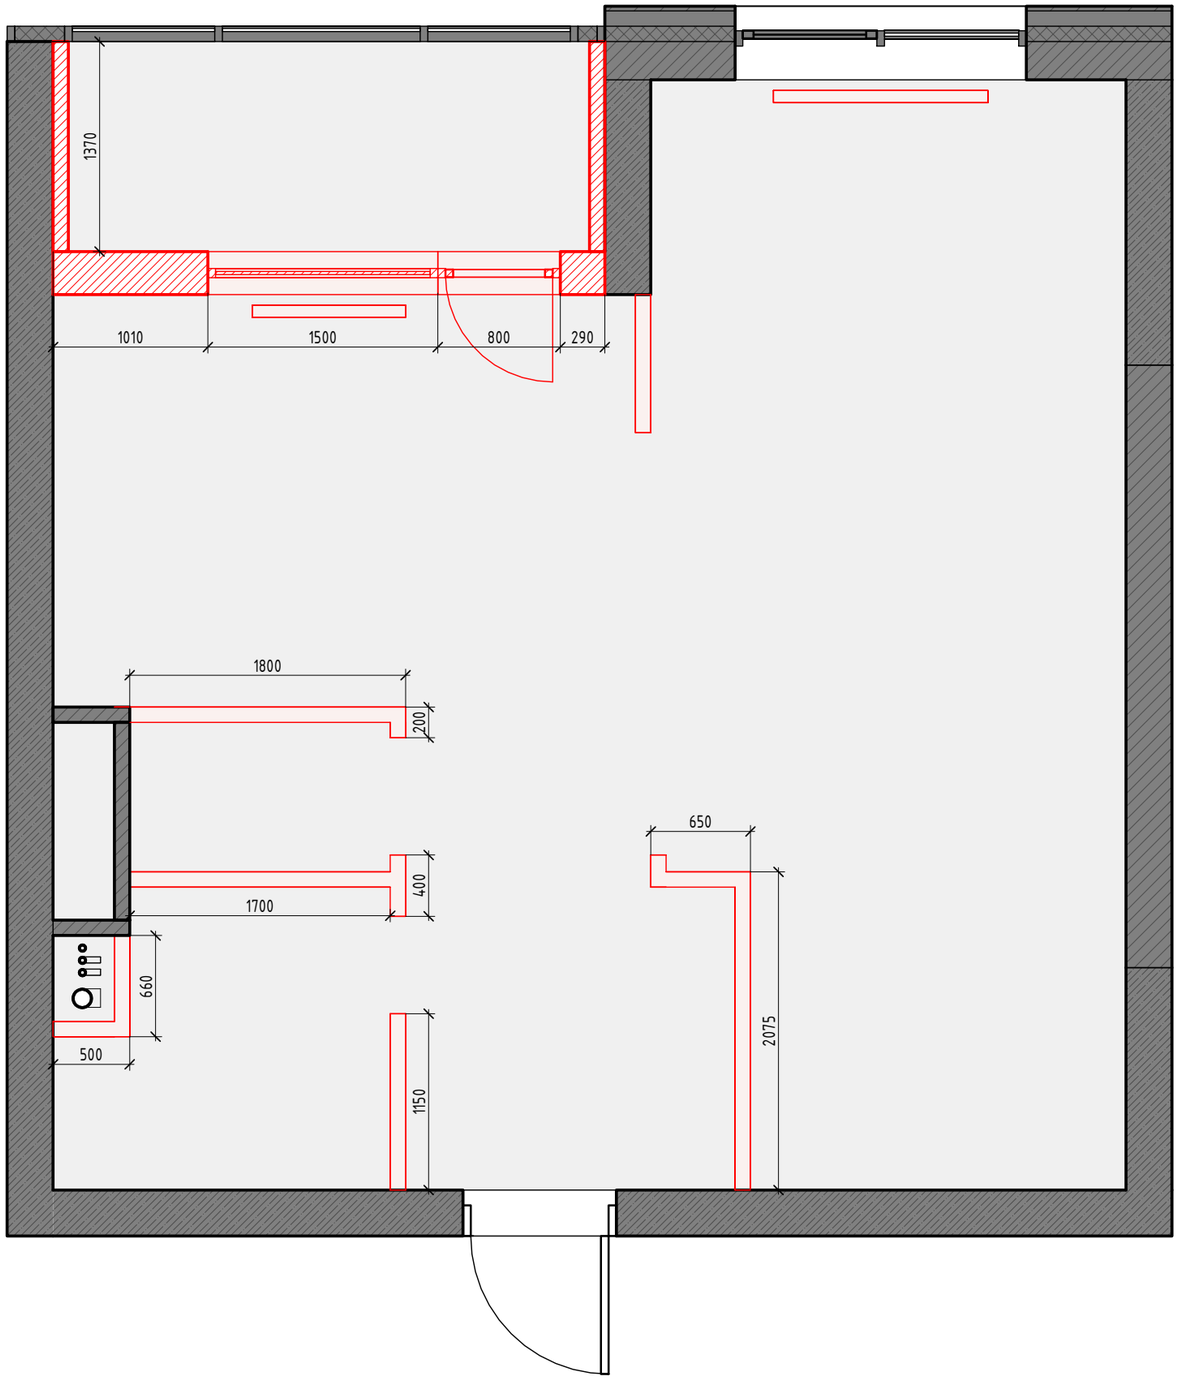


Схема существующей ситуации

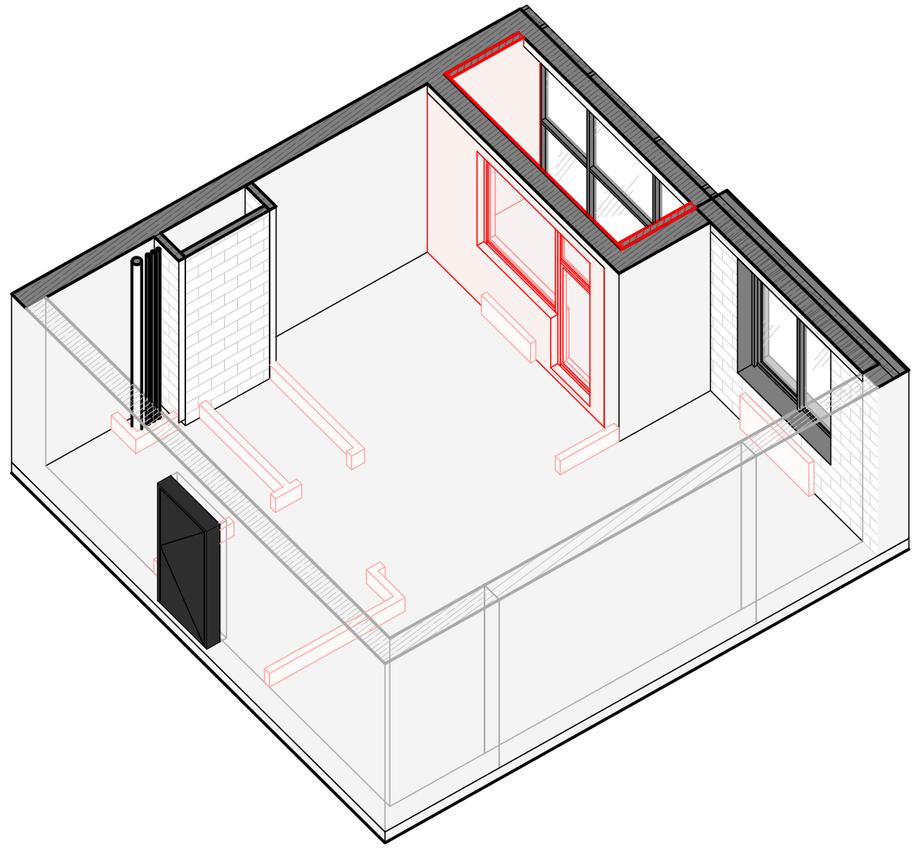

Условные обозначения:


- Демонтируемые стены
- Демонтируемые радиаторы отопления

Примечания:

1. Демонтировать все радиаторы.
2. Заменить входную дверь.
3. Заменить стояковую канализацию.
4. Переварить стояки воды.
1. 5. Шумоизолировать вент шаты.

ПЛАН ДЕМОНТАЖА

№ проекта	Раздел	Стадия	Лист	Листов
	АИ	РП	4	

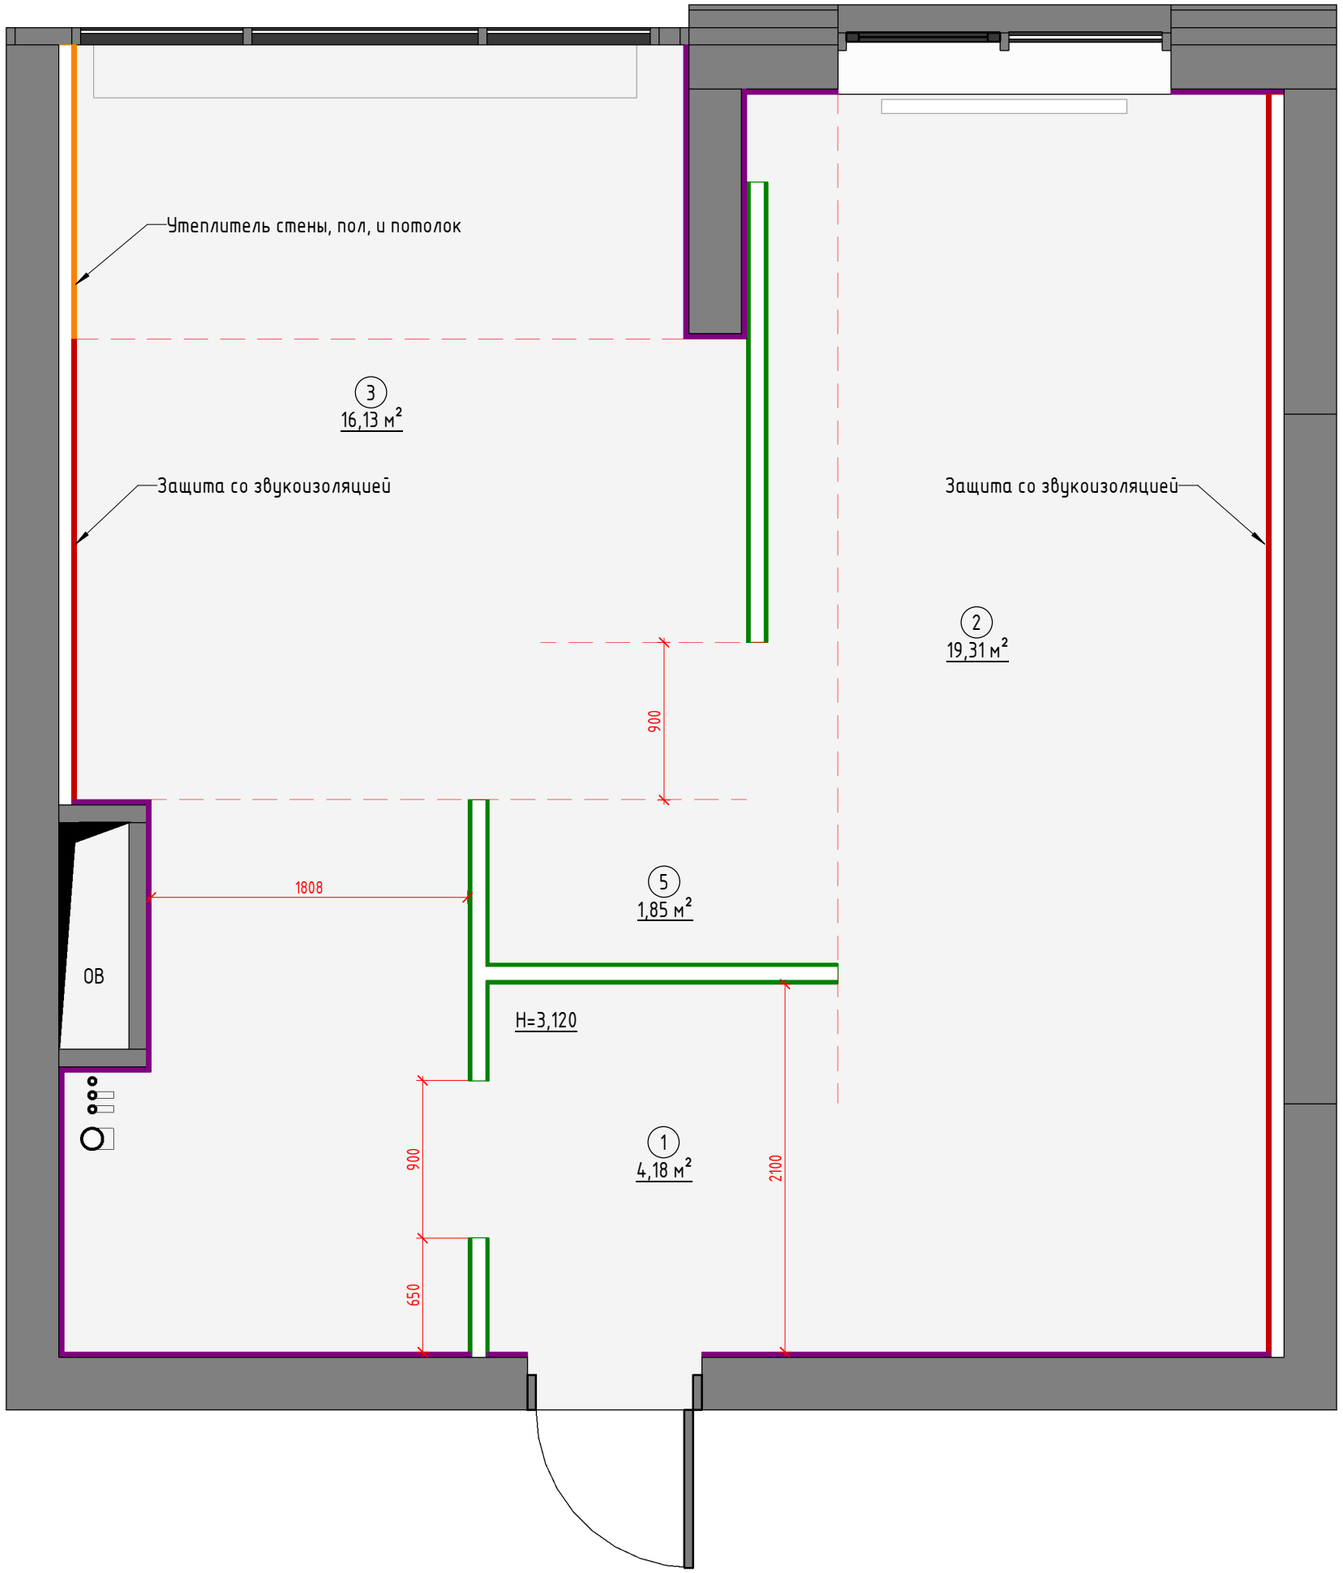

Экспликация помещений		
Номер	Наименование	Площадь, кв.м.
1	Прихожая	4,18
2	Кухня-гостинная	19,31
3	Спальня	16,13
4	Санузел	5,65
5	Гардероб	1,85
		47,12

Условные обозначения:

101 / 10 м² – Марка обозначения помещений

– Выравнивающая штукатурка

– Монтируемые перегородки из пеноблока, 120 мм

– Теплоизоляционные стены из ГКЛ, 100 мм

– Звукоизоляционные стены из ГКЛ, 100 мм

–Линии построения


Примечание:


1. За отметку 0.000 принята отметка чистого пола этажа.
2. Все высоты указаны от чистого пола.
3. Размеры на плане монтажа даны без учета чистовой отделки. На последующих планах чистовая отделка учтена.
4. Все стены выровнять, монтажные углы строго вывести под 90 градусов.
5. В санузлах выполнить обмазочную гидроизоляцию пола в 2 слоя с заводом на стены не менее 200мм от чистого пола. В душевой гидроизоляция по всей высоте стен.
6. В местах крепления сантехнического оборудования предусмотреть усиление перегородок из ГКЛВ.
7. Место установки, тип подключения и габариты конвекторов уточнить с поставщиками и Заказчиком.
8. Чертежи разработаны по черновым размерам помещения. Учесть корректировку размеров после возведения перегородок.
9. Размеры дверных проемов уточнить после утверждения модели и поставщика дверей.
10. Размеры со знаком * уточнить по месту.

ПЛАН МОНТАЖА ПЕРЕГОРОДОК, 1 этаж


№ проекта	Раздел	Стадия	Лист	Листов
	АИ	РП	5	


Вид 1

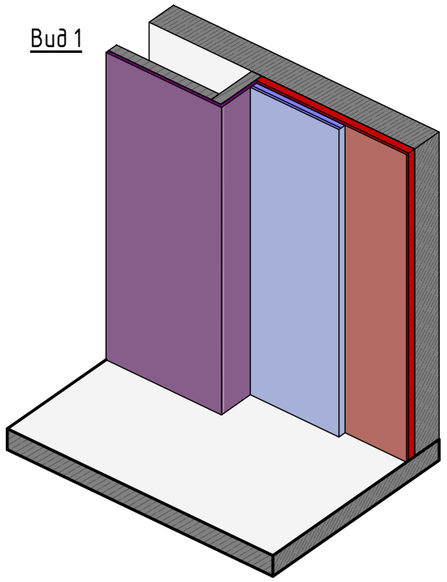

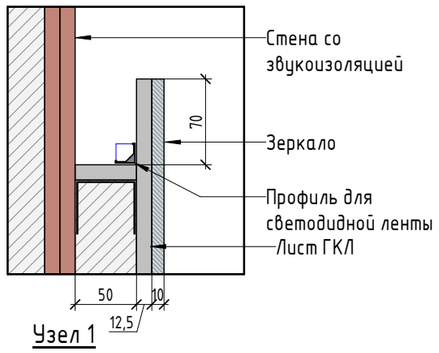

Узел 1

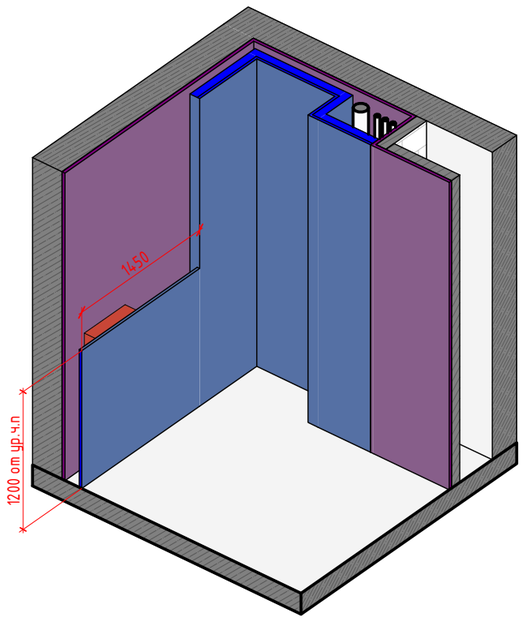

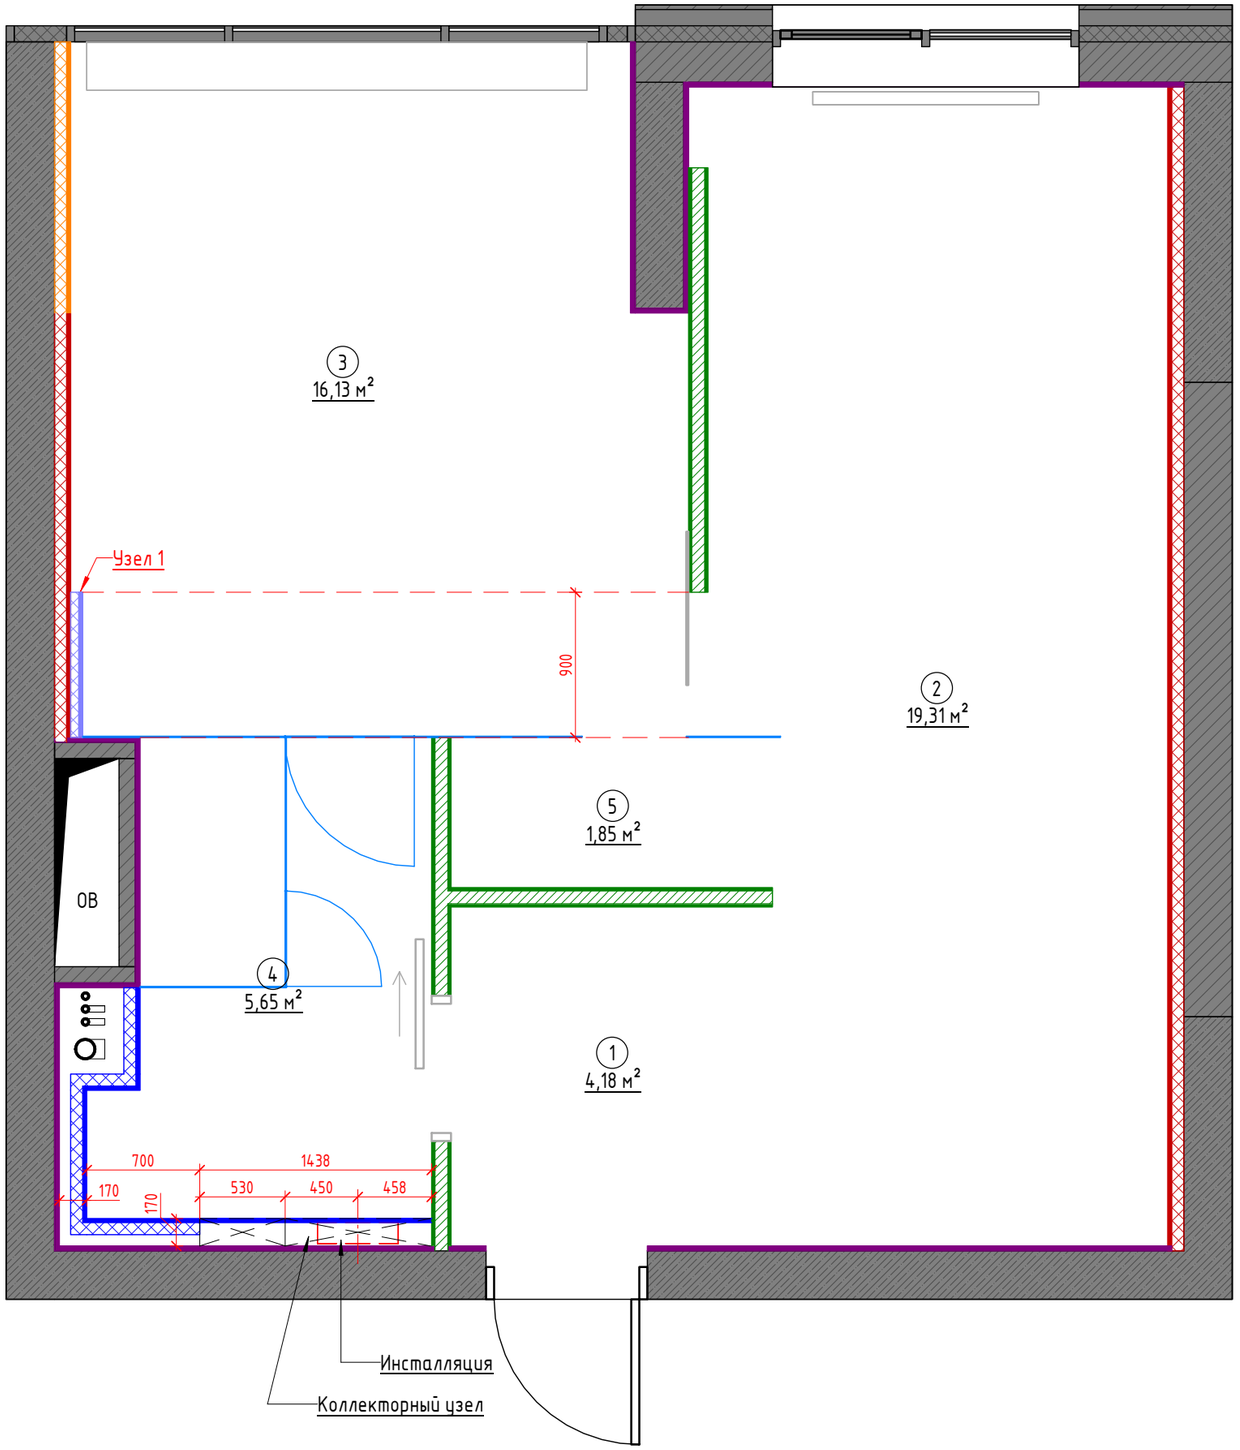

Экспликация помещений

Номер	Наименование	Площадь, кв.м.
1	Прихожая	4,18
2	Кухня-гостинная	19,31
3	Спальня	16,13
4	Санузел	5,65
5	Гардероб	1,85
		47,12

Условные обозначения:

101 / 10 м² – Марка обозначения помещений


- Выравнивающая штукатурка
- Монтируемые перегородки из пеноблока, 120 мм
- Теплоизоляционные стены из ГКЛ, 100 мм
- Звукоизоляционные стены из ГКЛ, 100 мм
- Стены из ГКЛ, 125 мм
- Стены из ГКЛВ, 125 мм
- Линии построения

Примечание:

1. За отметку 0.000 принята отметка чистого пола этажа.
2. Вторым этапом возводить ГК-конструкции в санузле
3. Все высоты указаны от чистого пола.
4. Размеры на плане монтажа даны без учета чистовой отделки. На последующих планах чистовая отделка учтена.
5. Все стены выровнять, монтажные углы строго вывести под 90 градусов (кроме обозначенных на чертеже)
6. В санузлах выполнить обмазочную гидроизоляцию пола в 2 слоя с заводом на стены не менее 200мм от чистого пола. В душевой гидроизоляция по всей высоте стен.
7. В местах крепления сантехнического оборудования предусмотреть усиление перегородок из ГКЛВ.
8. Размеры со знаком * уточнить по месту.

ПЛАН МОНТАЖА ГК-конструкций. 2 этап

№ проекта	Раздел	Стадия	Лист	Листов
	АИ	РП	6	

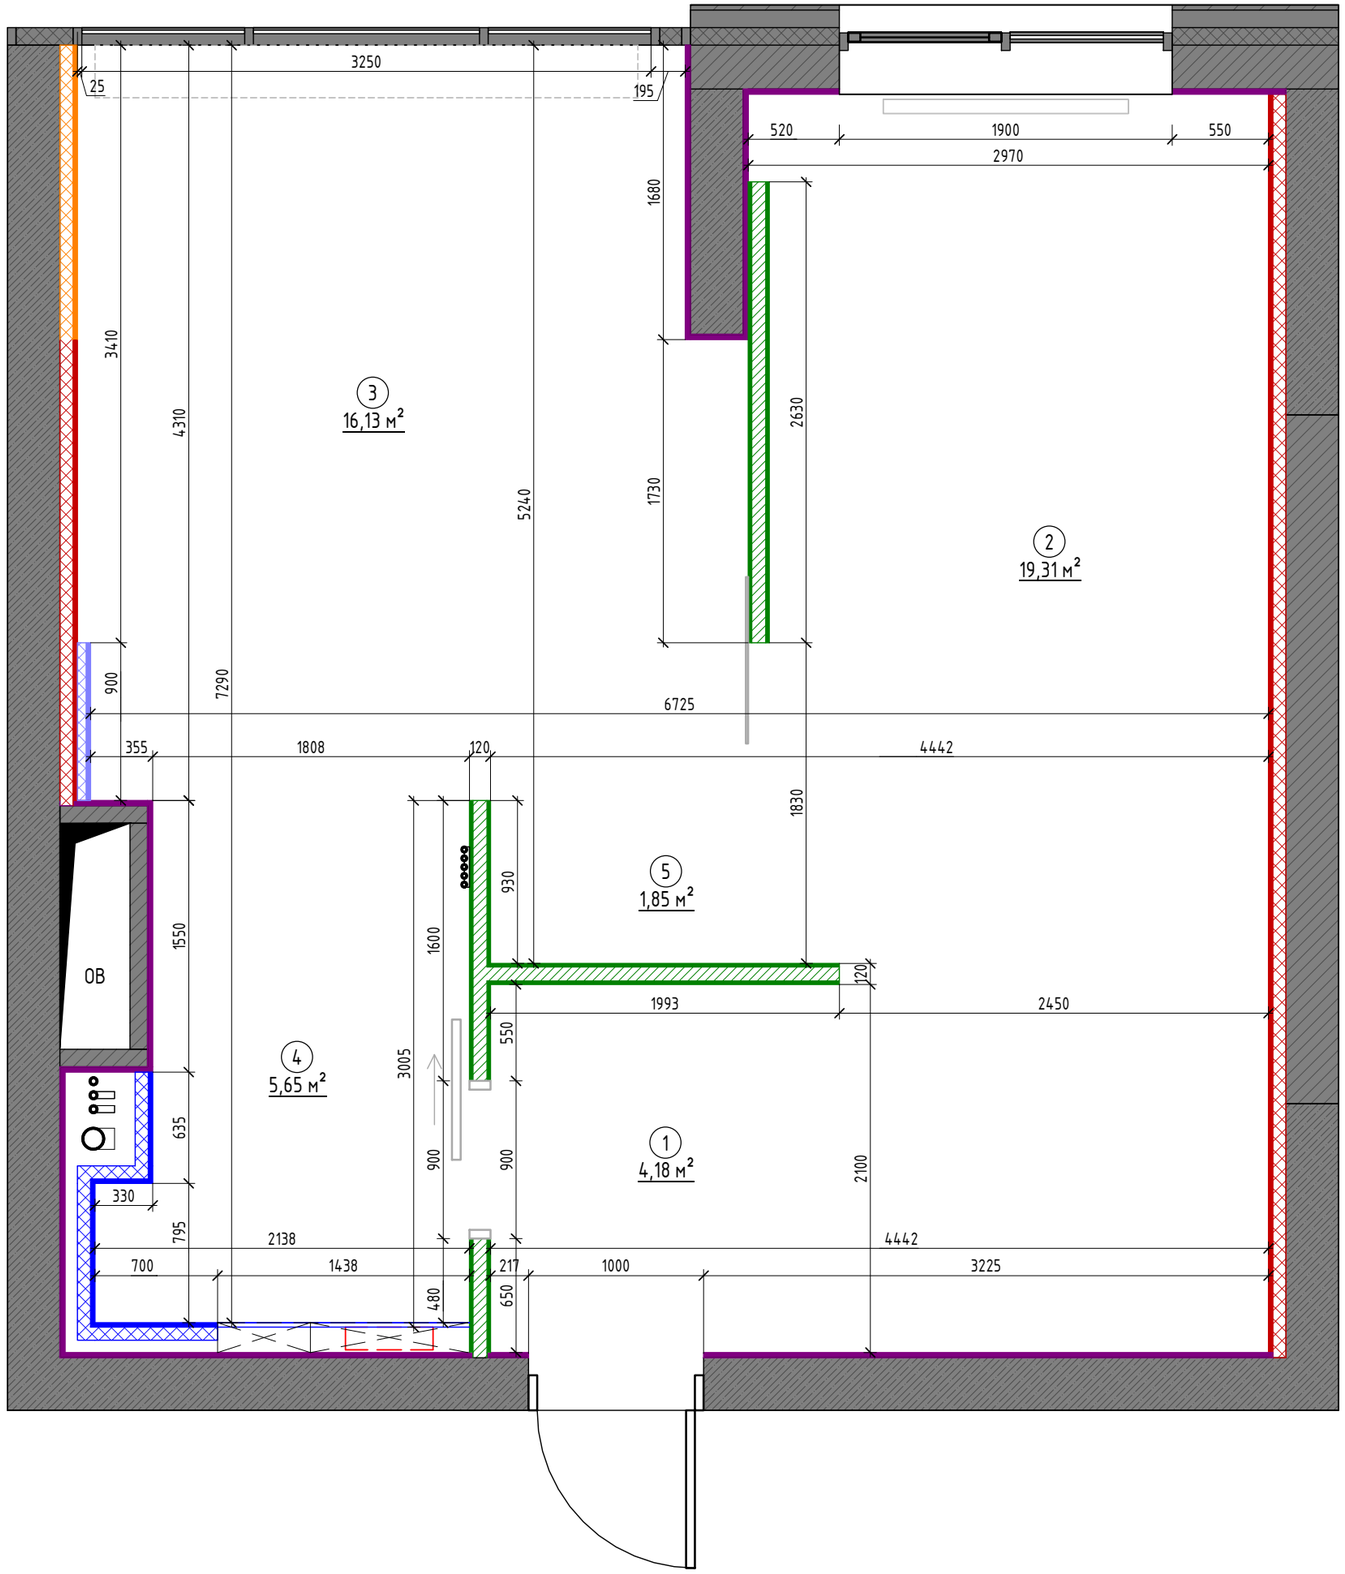

Экспликация помещений		
Номер	Наименование	Площадь, кв.м.
1	Прихожая	4,18
2	Кухня-гостинная	19,31
3	Спальня	16,13
4	Санузел	5,65
5	Гардероб	1,85
		47,12


Примечание:

1. Все размеры уточнить по месту.

ОБМЕРНЫЙ ПЛАН ПОСЛЕ МОНТАЖА

№ проекта	Раздел	Стадия	Лист	Листов
	АИ	РП	7	

Экспликация помещений		
Номер	Наименование	Площадь, кв.м.
1	Прихожая	4,18
2	Кухня-гостинная	19,31
3	Спальня	16,13
4	Санузел	5,65
5	Гардероб	1,85
		47,12

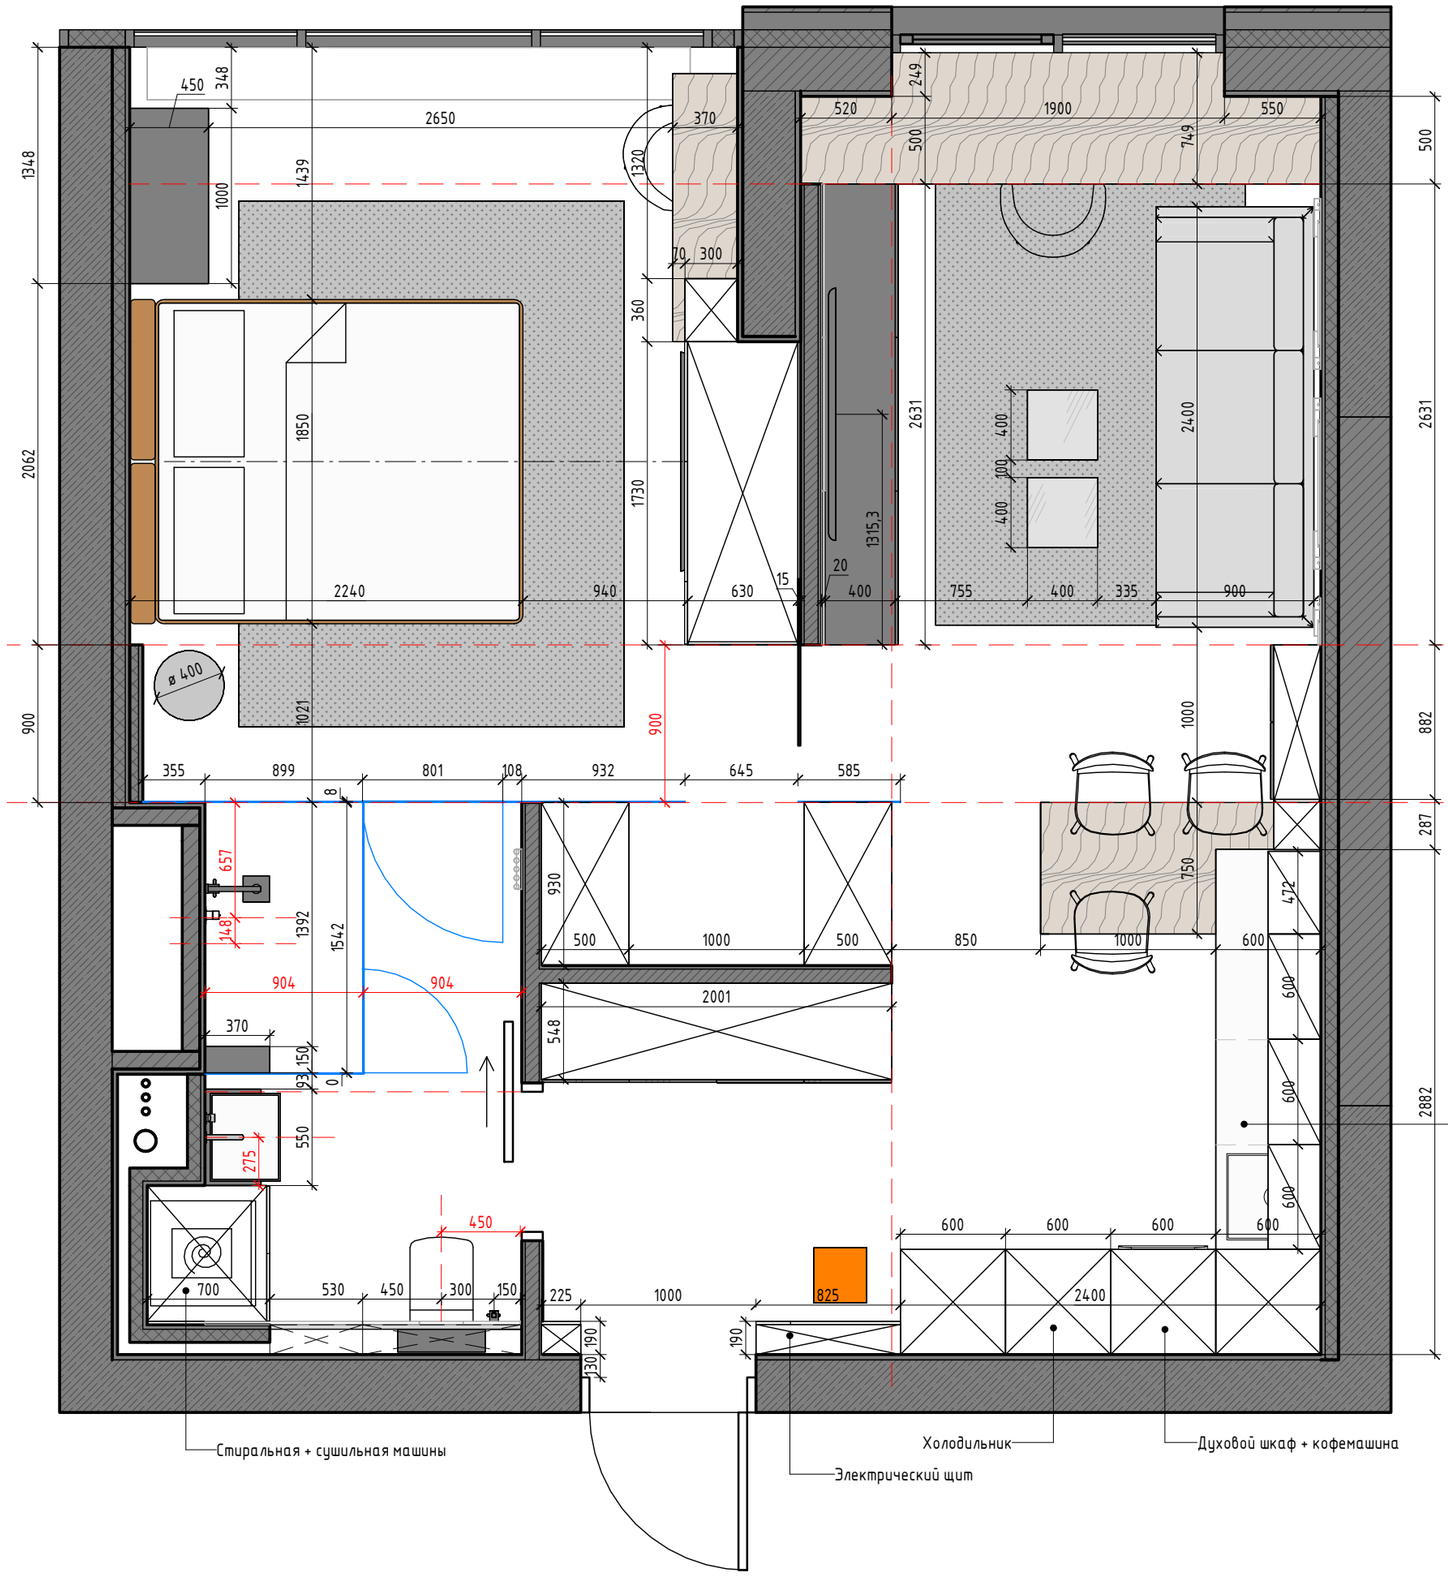


Примечание:

1. Все размеры уточнить по месту.
2. Размеры корпусной мебели уточнить по месту при заказе.
3. СМОТРЕТЬ СОВМЕСТНО С РАЗВЕРТКАМИ ПОМЕЩЕНИЙ

ПЛАН РАССТАНОВКИ МЕБЕЛИ С РАЗМЕРАМИ


№ проекта	Раздел	Стадия	Лист	Листов
	АИ	РП	8	

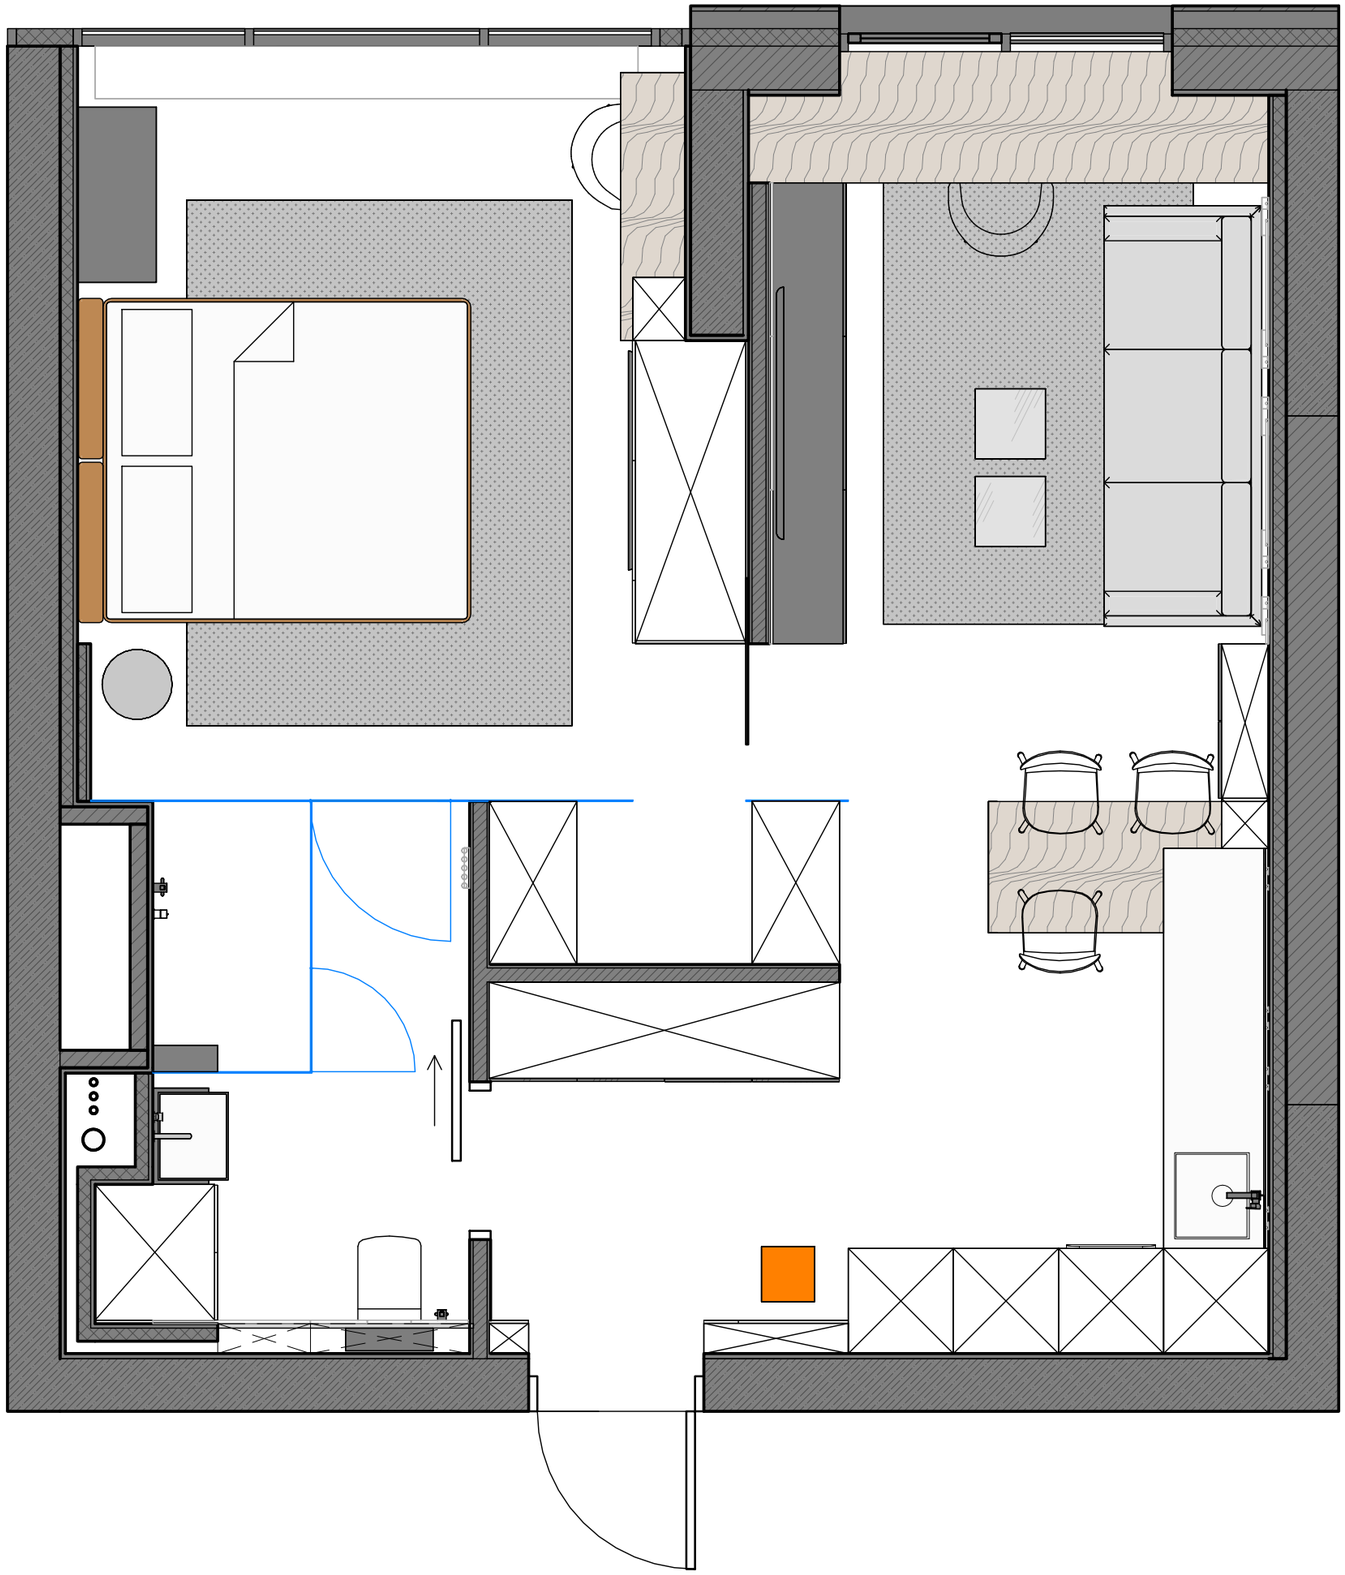

Экспликация помещений		
Номер	Наименование	Площадь, кв.м.
1	Прихожая	4,18
2	Кухня-гостинная	19,31
3	Спальня	16,13
4	Санузел	5,65
5	Гардероб	1,85
		47,12

ПЛАН РАССТАНОВКИ МЕБЕЛИ

№ проекта	Раздел	Стадия	Лист	Листов
	АИ	РП	9	

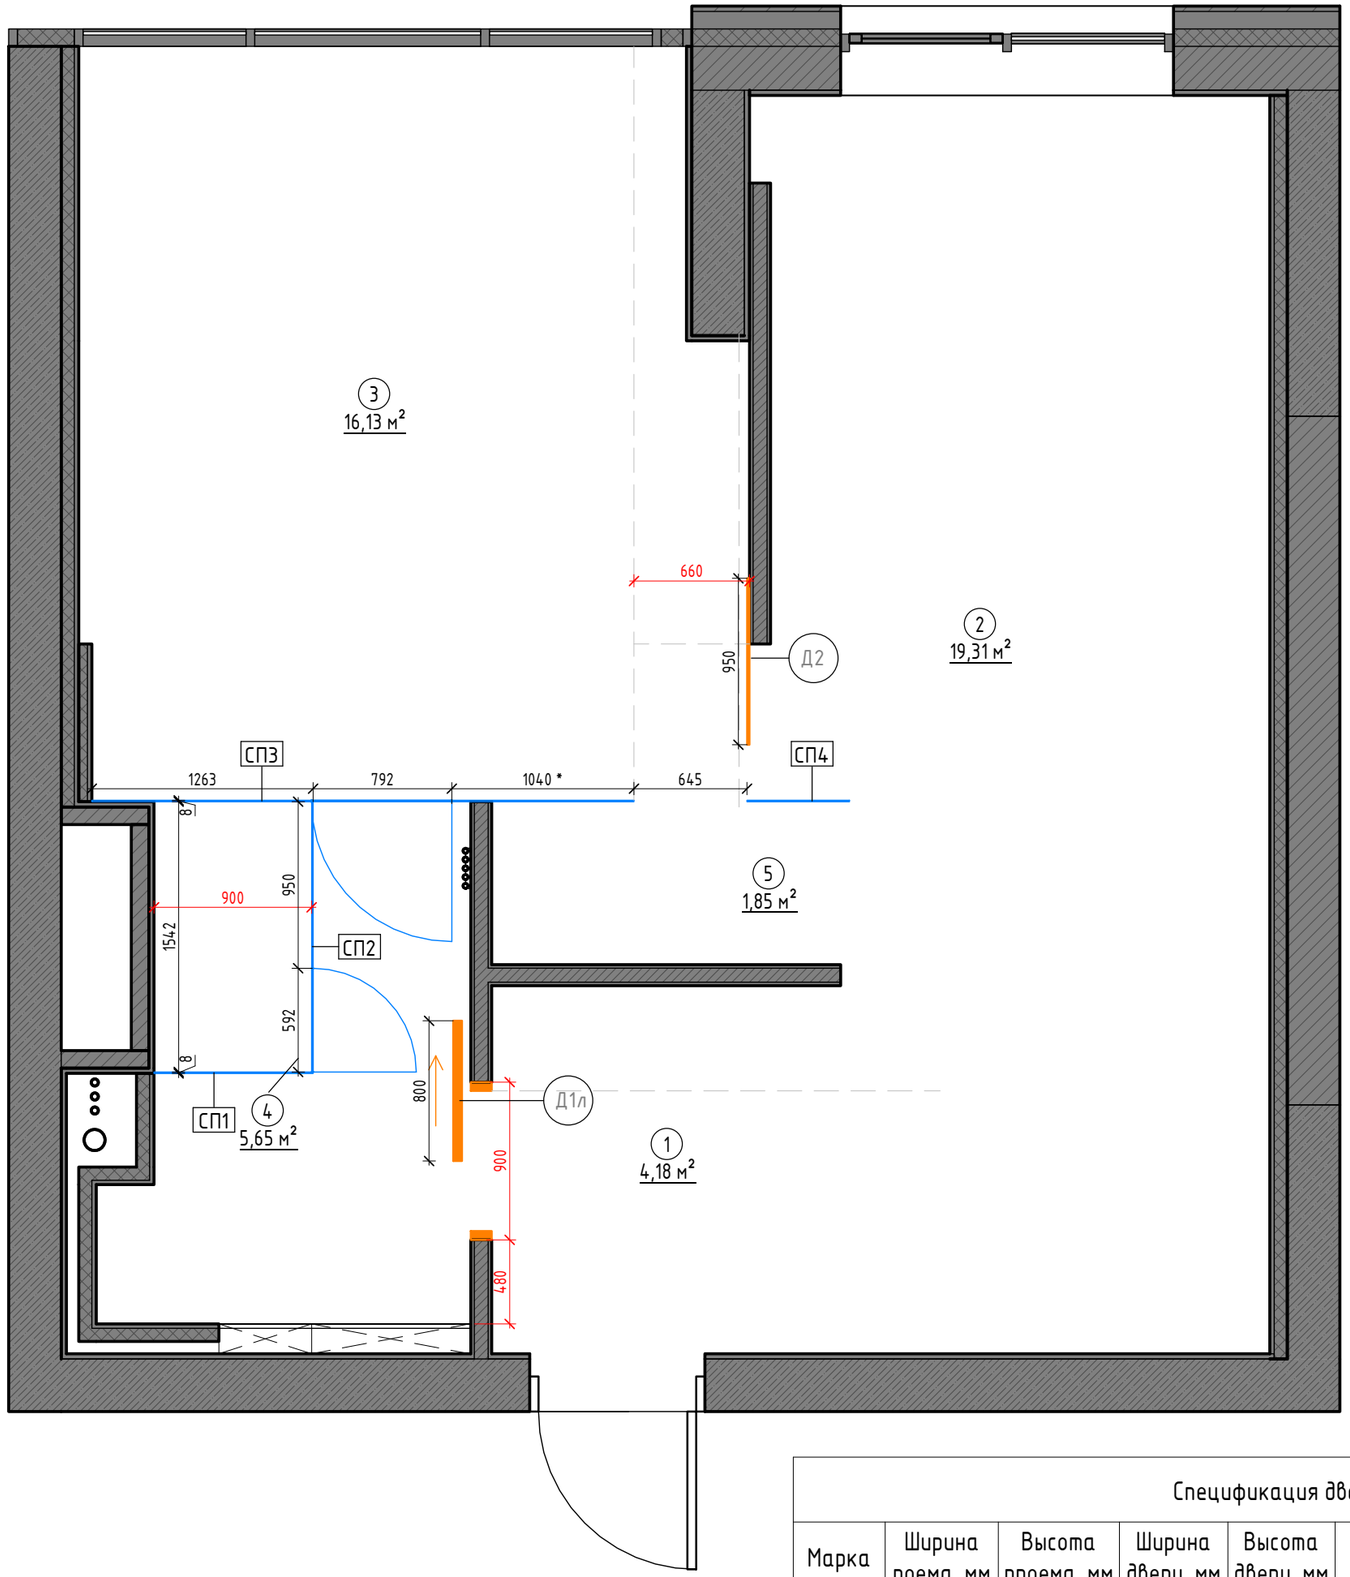

Экспликация помещений		
Номер	Наименование	Площадь, кв.м.
1	Прихожая	4,18
2	Кухня-гостинная	19,31
3	Спальня	16,13
4	Санузел	5,65
5	Гардероб	1,85
		47,12

Спецификация стеклянных перегородок			
Марка	Ширина, мм	Высота, мм	Описание
СП1	910	2500	Стеклянная перегородка, черное стекло
СП2	1540	2500	Стеклянная перегородка, черное стекло
СП3	3090	2500	Стеклянная перегородка, черное стекло
СП4	580	2500	Стеклянная перегородка, черное стекло

Условные обозначения:

- Монтируемая дверь
- Стеклянная перегородка
- Д3 – Марка двери
- СП1 – Марка стеклянной перегородки


Примечание:

1. Все размеры уточнить по месту.
2. Все высоты указаны от чистого пола.
3. В проекте заложены межкомнатные двери со скрытой коробкой монтажа.
4. Входную дверь при необходимости заменить, чтобы соответствовала существующей со стороны общего коридора.
5. Размеры со знаком * уточнить по месту.

Спецификация дверей						
Марка	Ширина поема, мм	Высота проема, мм	Ширина двери, мм	Высота двери, мм	Описание	Кол-во, шт
Д1л	900		800	2100	Дверь откатная	1
Д2	13		950	2600	Передвижная перегородка	1


ПЛАН ЗАПОЛНЕНИЯ ПРОЕМОВ

№ проекта	Раздел	Стадия	Лист	Листов
	АИ	РП	10	

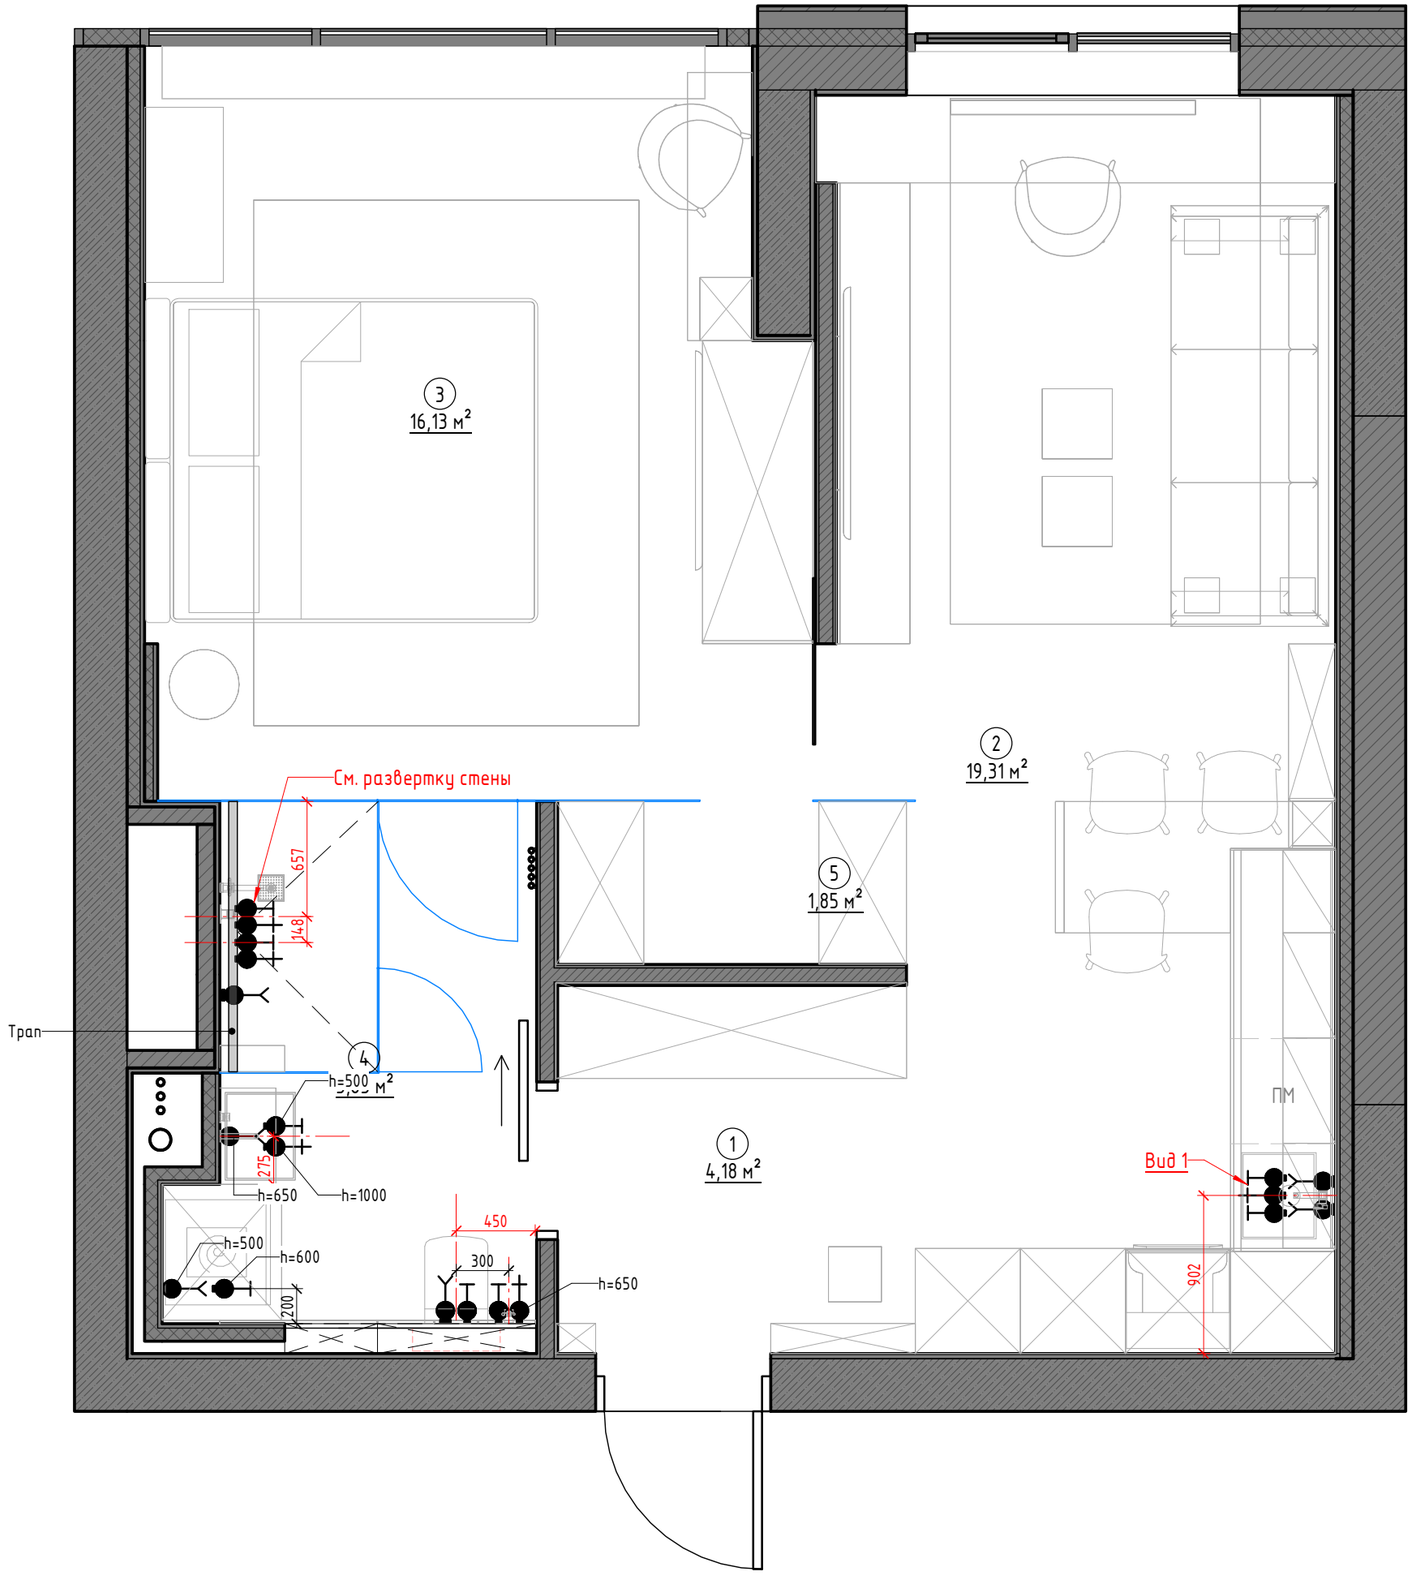

Экспликация помещений		
Номер	Наименование	Площадь, кв.м.
1	Прихожая	4,18
2	Кухня-гостинная	19,31
3	Спальня	16,13
4	Санузел	5,65
5	Гардероб	1,85
		47,12

Вид 1

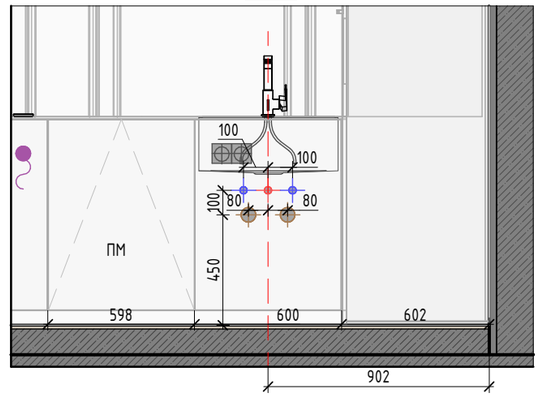

Условные обозначения:


- Вывод горячей воды
- Вывод холодной воды
- Вывод канализации

Примечание:

1. Все размеры уточнить по месту.
2. Высоты сантехнического оборудования привязаны на развертках помещений.
3. Уточнить привязку сантехнического оборудования после закупки.
4. СМОТРЕТЬ СОВМЕСТНО С РАЗВЕРТКАМИ ПОМЕЩЕНИЙ.

ПЛАН ПОДВОДА КОММУНИКАЦИЙ

№ проекта	Раздел	Стадия	Лист	Листов
	АИ	РП	11	

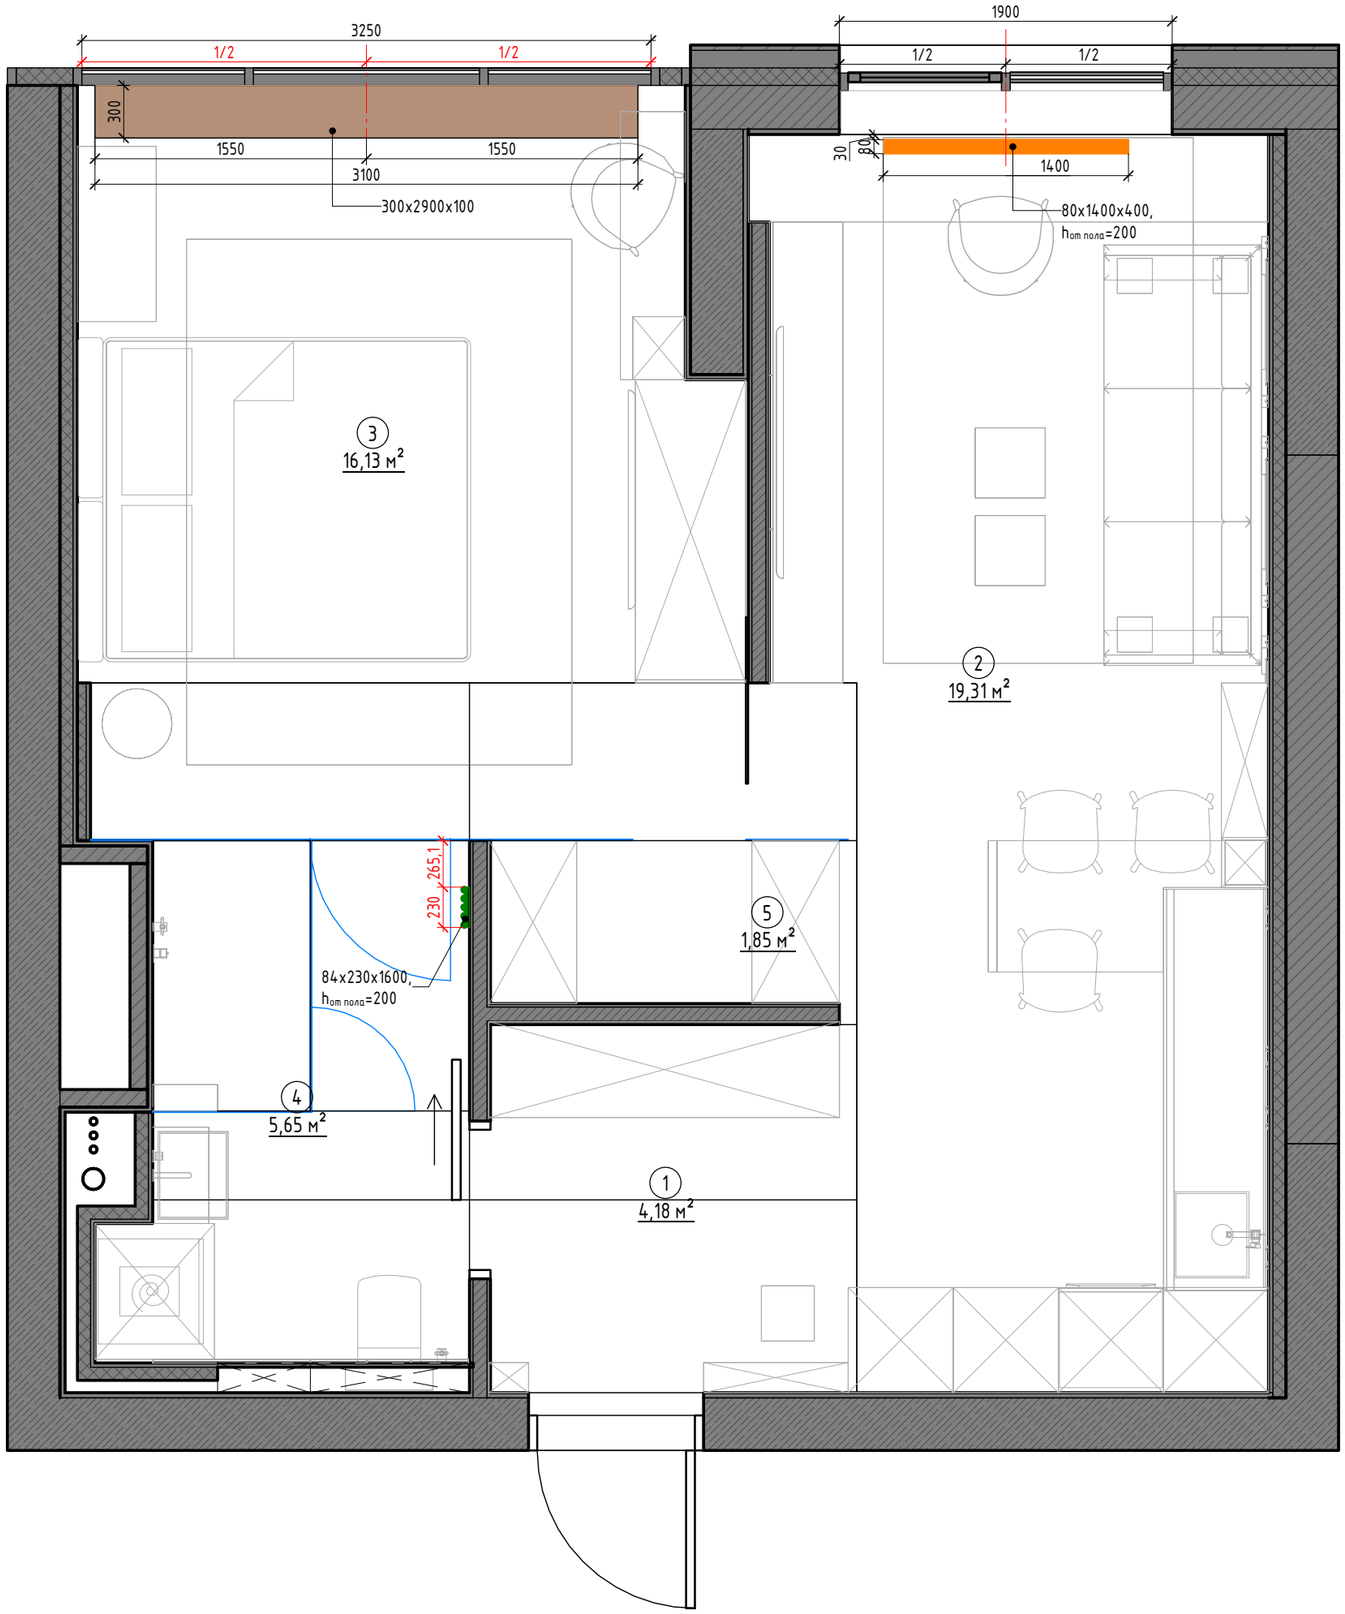

Экспликация помещений		
Номер	Наименование	Площадь, кв.м.
1	Прихожая	4,18
2	Кухня-гостинная	19,31
3	Спальня	16,13
4	Санузел	5,65
5	Гардероб	1,85
		47,12

Условные обозначения:


- Встроенный конвектор (водяной)
- Радиатор отопления (водяной)
- Полотенцесушитель (электрический)

Примечание:

1. Привязки по высоте и от стен уточнить после заказа радиаторов.
2. Выводы радиаторов делать из стены по тех. карте радиаторов.
3. СМОТРЕТЬ СОВМЕСТНО С РАЗВЕРТКАМИ ПОМЕЩЕНИЙ.

ПЛАН РАДИАТОРОВ

№ проекта	Раздел	Стадия	Лист	Листов
	АИ	РП	12	

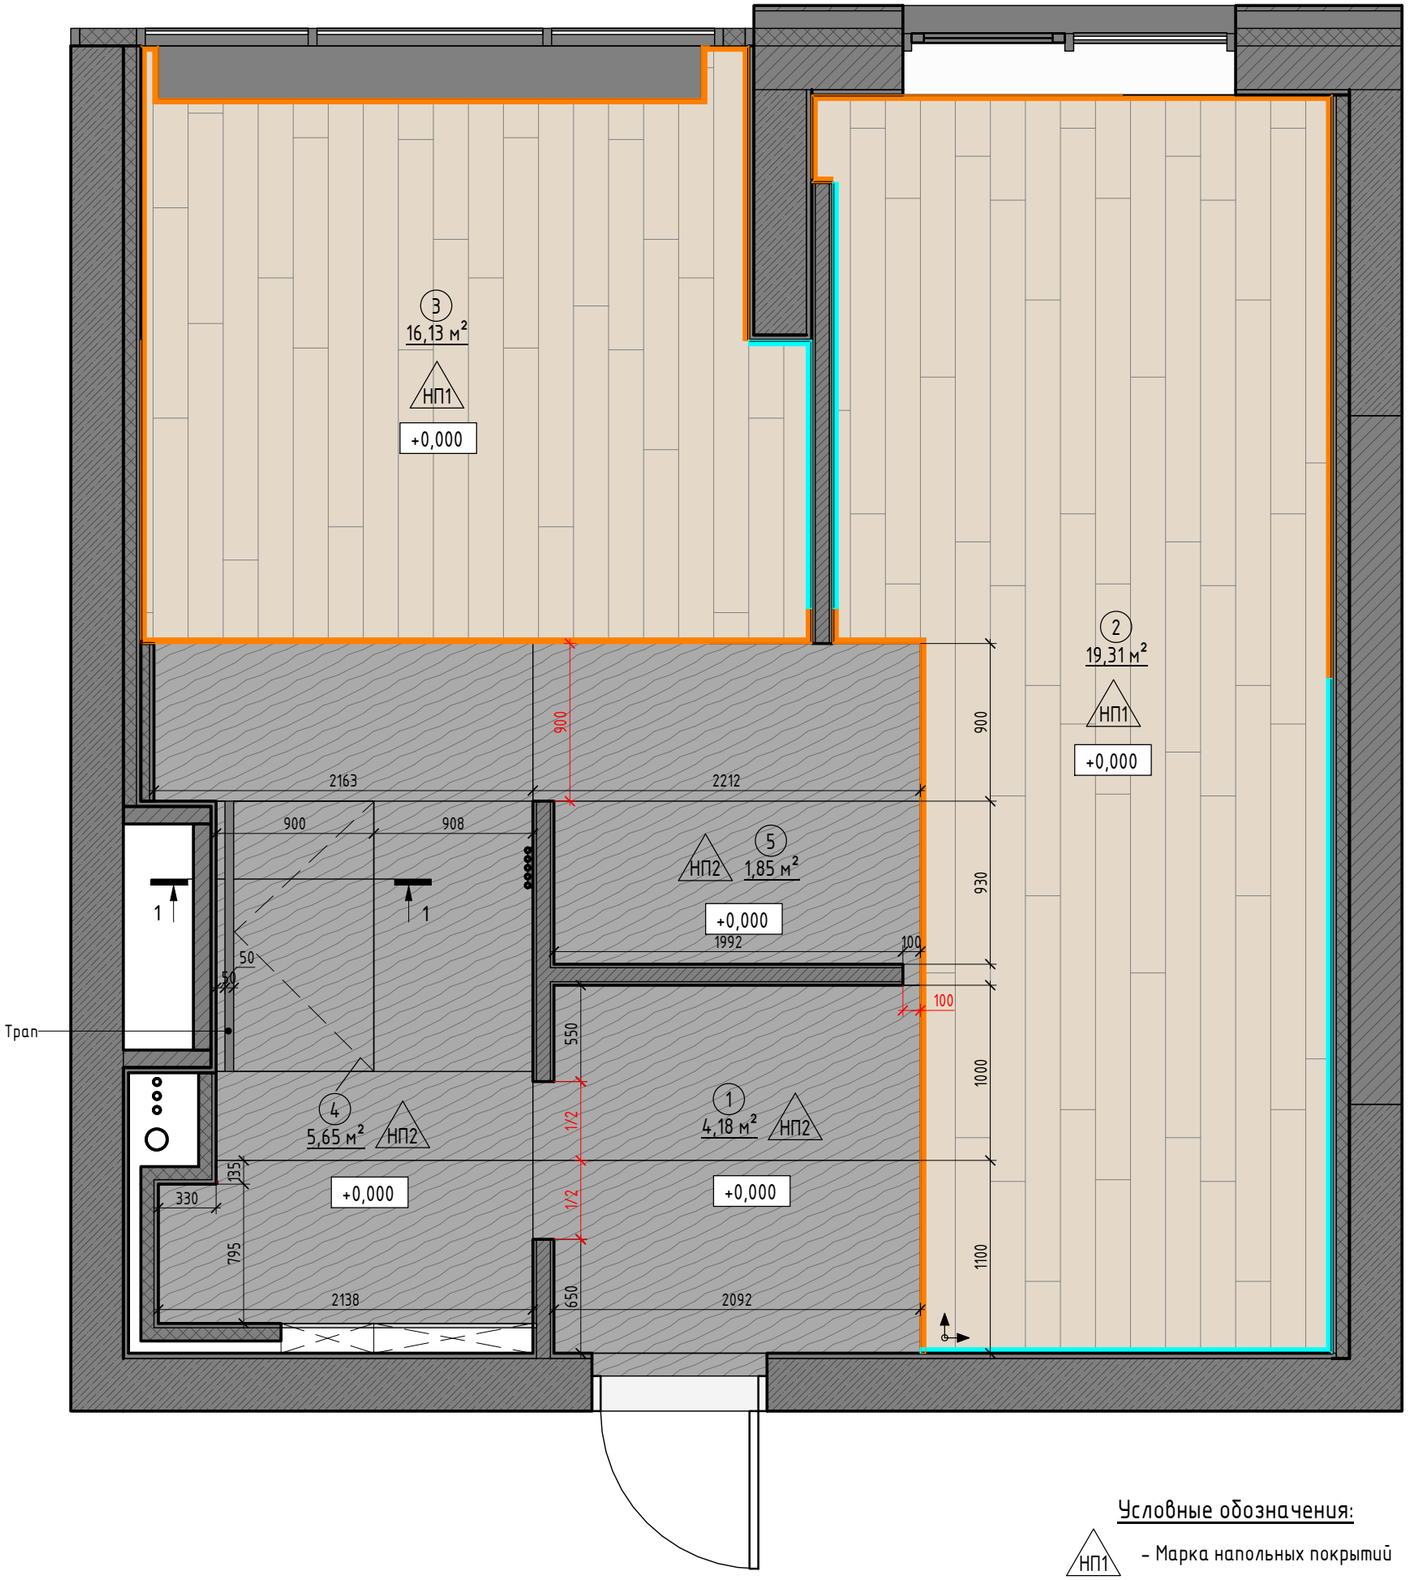

Экспликация помещений

Номер	Наименование	Площадь, кв.м.
1	Прихожая	4,18
2	Кухня-гостинная	19,31
3	Спальня	16,13
4	Санузел	5,65
5	Гардероб	1,85
		47,12


Спецификация напольных покрытий

Тип	Изображение	Описание	Площадь, кв.м
НП1		Инженерная доска разноширокая. предполагаемая толщина 16 мм	30,02
НП2		Плитка PORCELANOSA SAVAGE DARK NATURE, 1200x2500x6 мм	16,18

Периметр реза инженерной доски

Изображение	Описание	Длина, пог.м
	Чистовой рез	26,8
	Черновой рез	12,4

Сечение 1-1

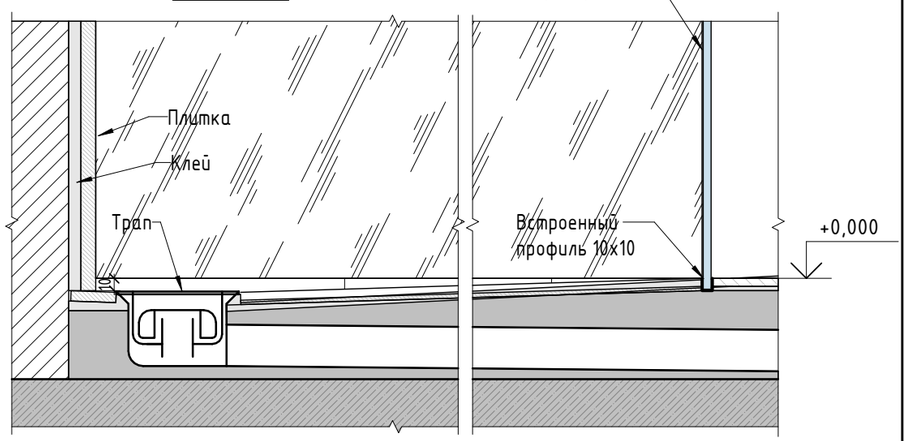

Условные обозначения:

НП1 – Марка напольных покрытий

+0,000 – Отметка уровня пола


– Начало раскладки

Примечание:

1. Все размеры уточнить по месту.
2. Укладка инженерной доски производится хаотичной раскладкой.
3. Количество материалов указано без запаса.

ПЛАН НАПОЛЬНЫХ ПОКРЫТИЙ


№ проекта	Раздел	Стадия	Лист	Листов
	АИ	РП	14	

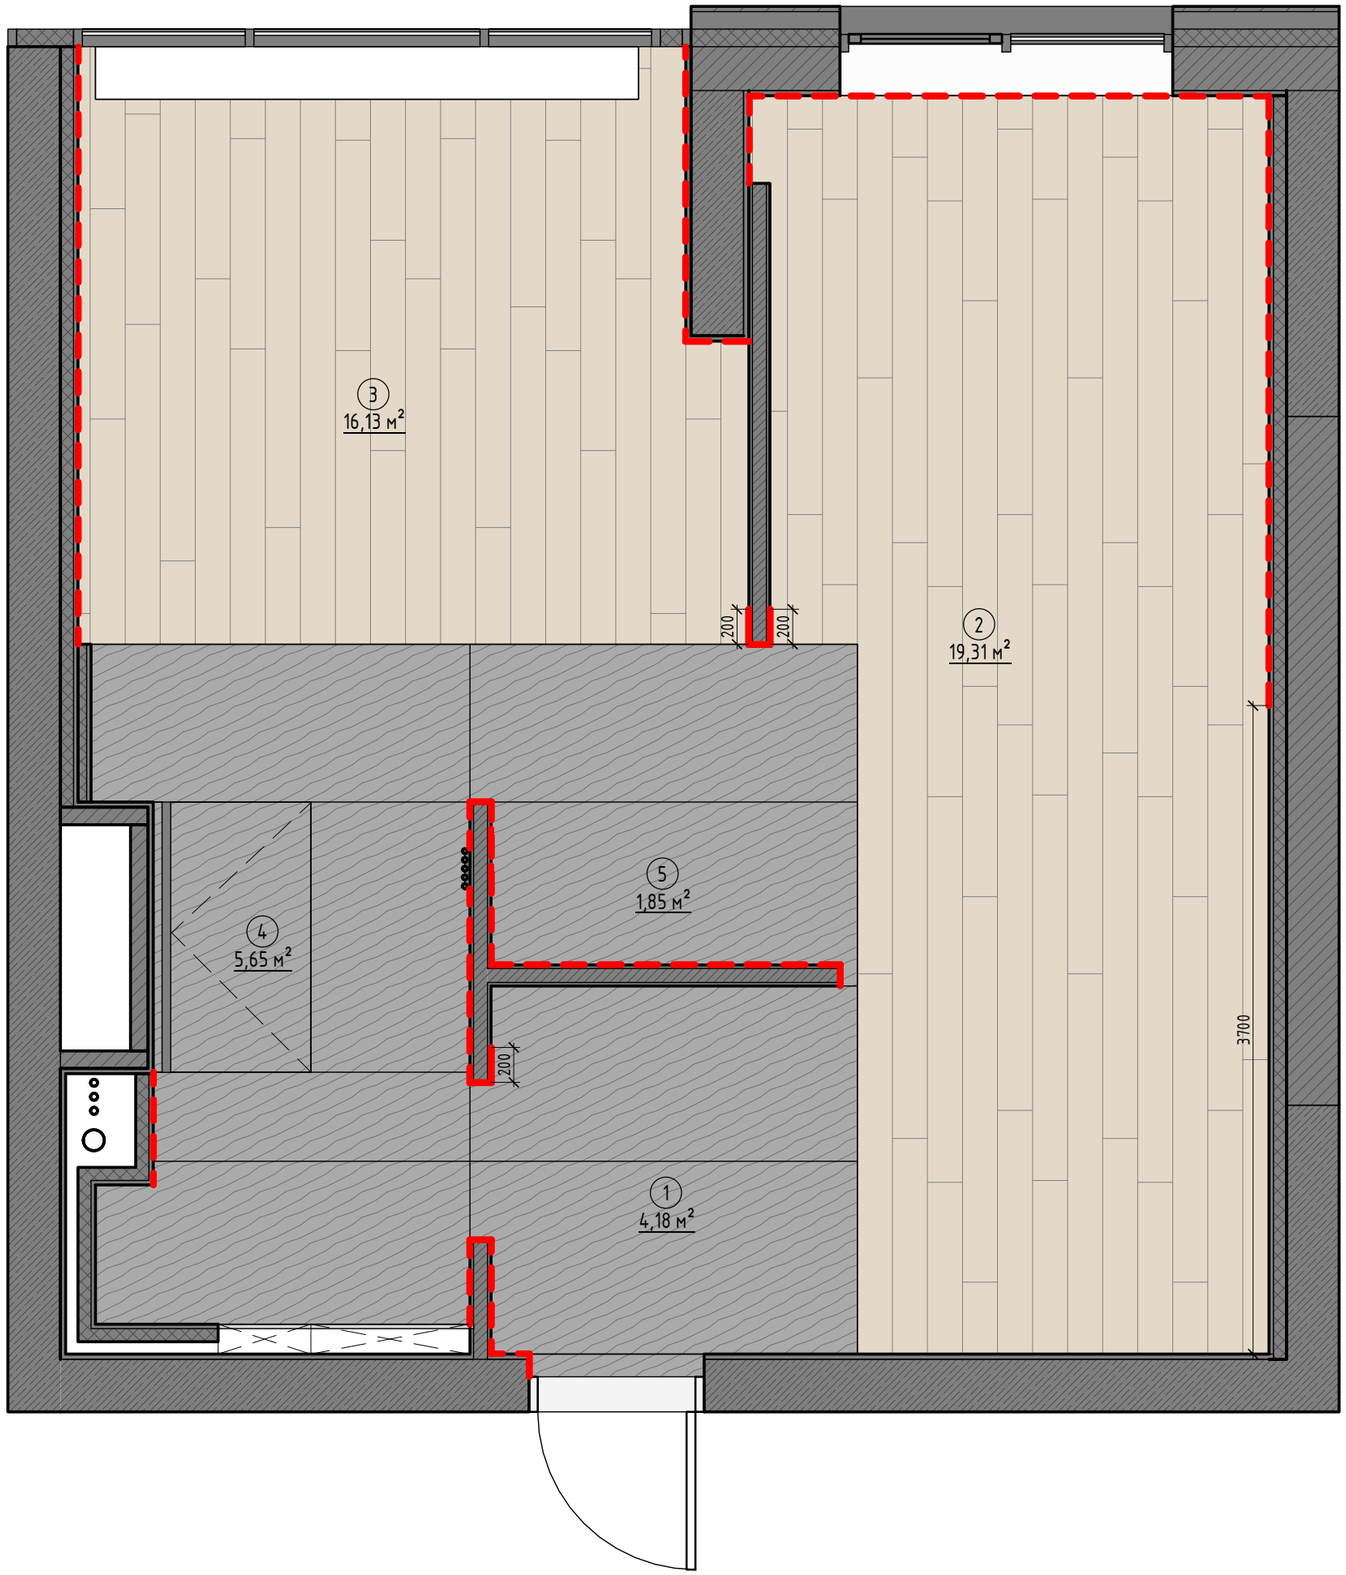

Экспликация помещений		
Номер	Наименование	Площадь, кв.м.
1	Прихожая	4,18
2	Кухня-гостинная	19,31
3	Спальня	16,13
4	Санузел	5,65
5	Гардероб	1,85
		47,12

Спецификация плинтусов (пол)		
Изображение	Описание	Длина, пог.м
— — — —	Плинтус алюминевый	20,2

Устройство скрытого плинтуса

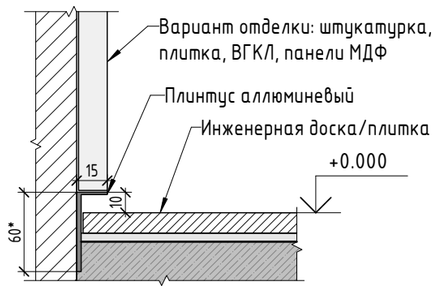

*Смотреть совместно с ПЛАНОМ ОТДЕЛКИ (л. 26)

Условные обозначения:


+0,000 – Отметка уровня пола

Примечание:

1. Все размеры уточнить по месту.
2. Количество материалов указано без запаса.

ПЛАН РАСПОЛОЖЕНИЯ ПЛИНТУСА

№ проекта	Раздел	Стадия	Лист	Листов
	АИ	РП	15	

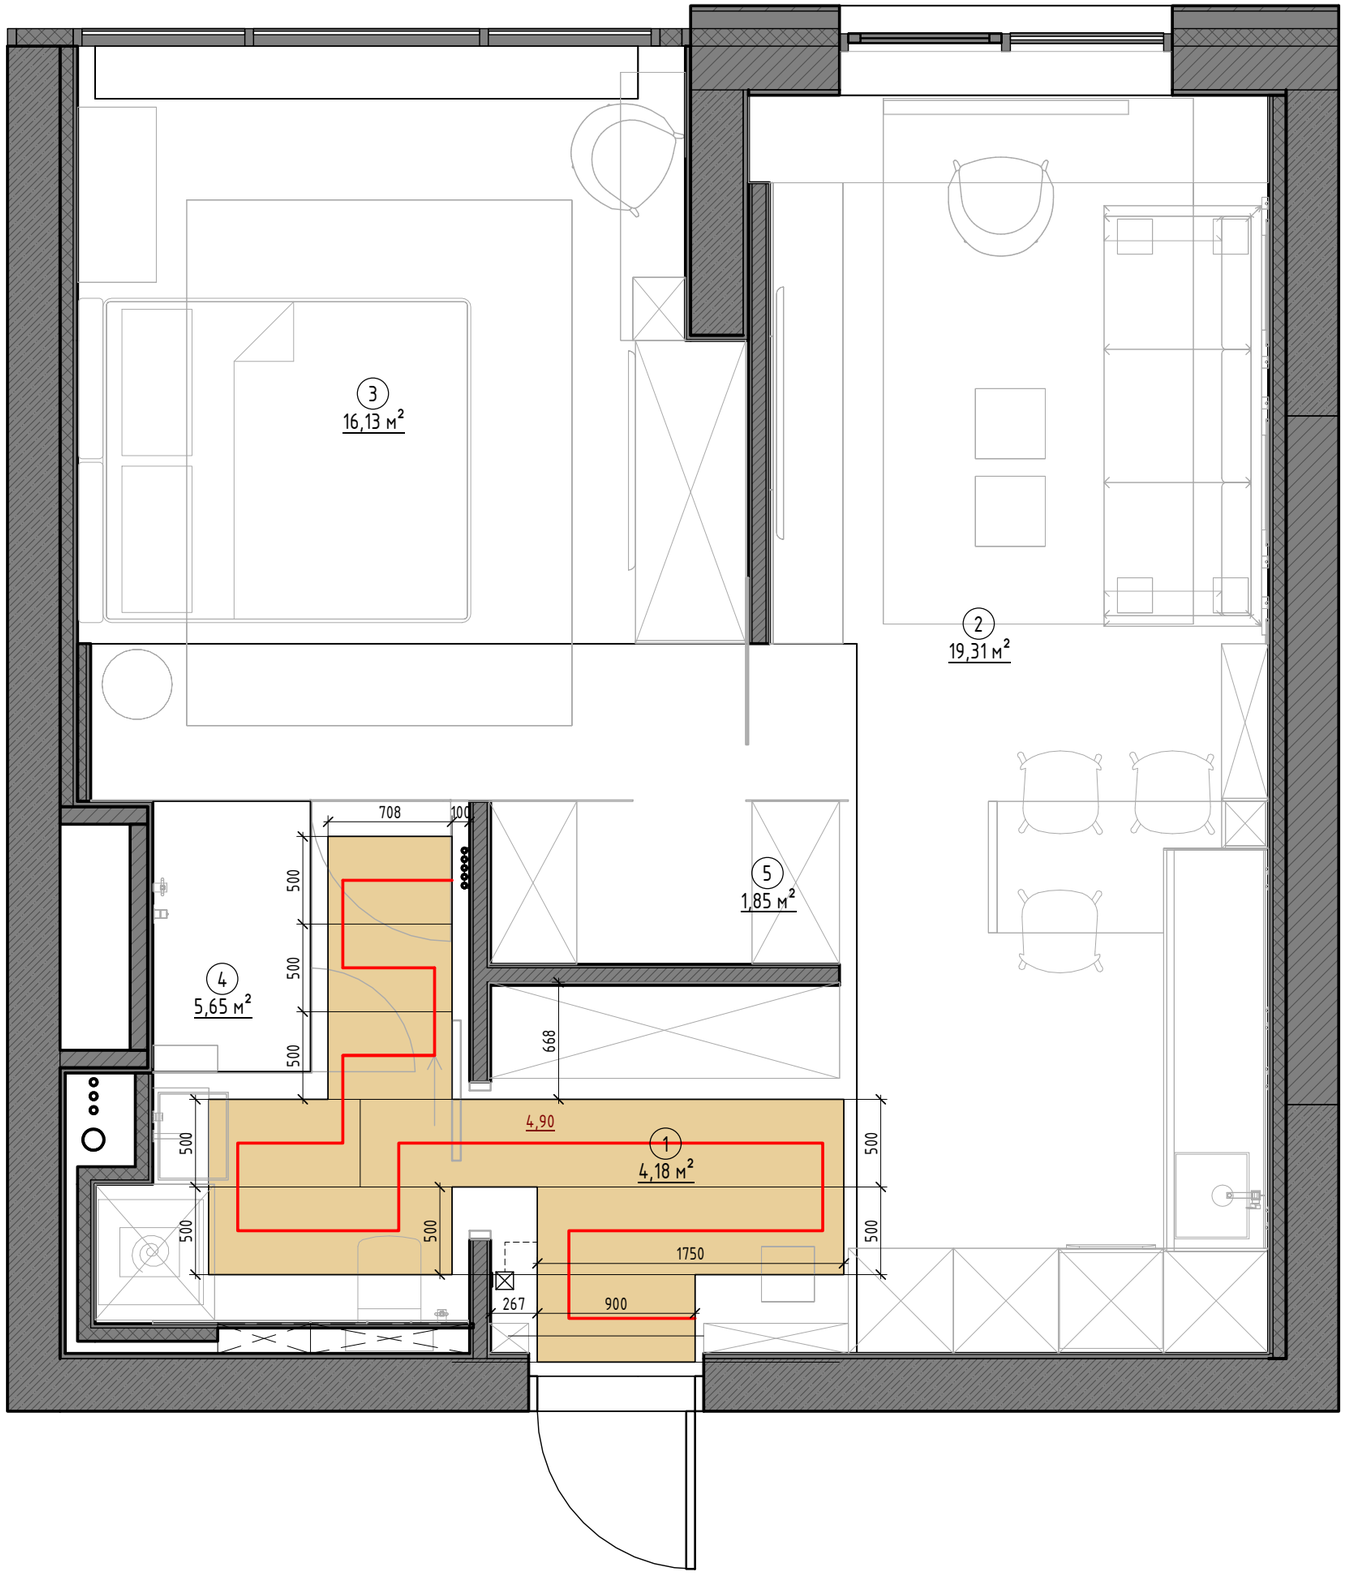

Экспликация помещений		
Номер	Наименование	Площадь, кв.м.
1	Прихожая	4,18
2	Кухня-гостинная	19,31
3	Спальня	16,13
4	Санузел	5,65
5	Гардероб	1,85
		47,12

Спецификация теплых полов		
Условное обозначение	Описание	Площадь, кв.м
	Теплый пол	4,90

Условные обозначения:


⊠ – Терморегулятор, h=900

Примечание:

1. Высота терморегулятора по умолчанию на 900 мм от чистого пола, если не указана другая высота.
2. Все размеры уточнить по месту.
3. Устройство теплого пола в клею плитки.
4. Теплый пол укладывать от стен, мебели на 100 мм, если не указан другой размер.
5. Терморегулятор установить по одной рамке с выключателями, см. лист 24.

ПЛАН ТЕПЛОГО ПОЛА

№ проекта	Раздел	Стадия	Лист	Листов
	АИ	РП	16	

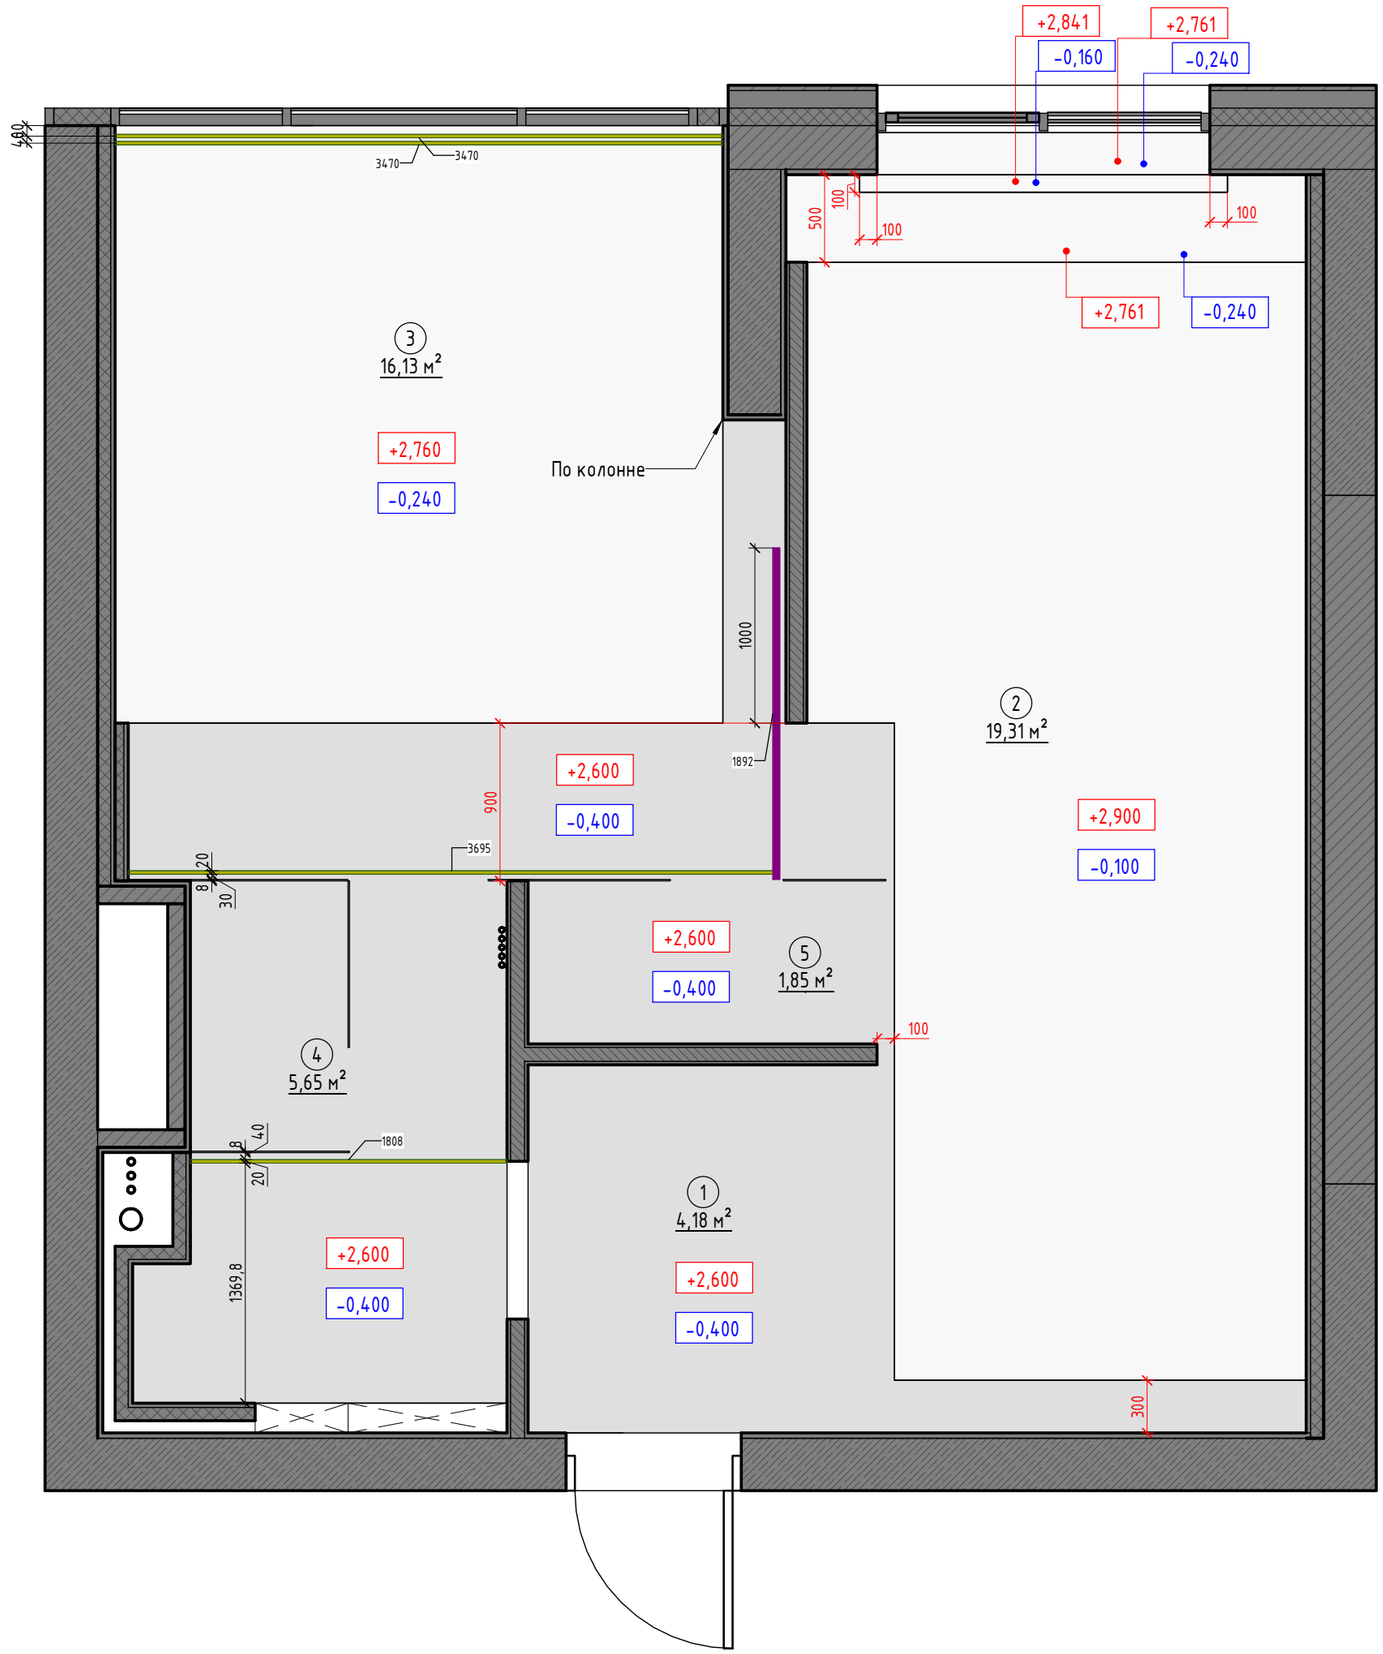

Экспликация помещений

Номер	Наименование	Площадь, кв.м.
1	Прихожая	4,18
2	Кухня-гостинная	19,31
3	Спальня	16,13
4	Санузел	5,65
5	Гардероб	1,85
		47,12

Спецификация потолков

Условное обозначение	Описание	Площадь, кв.м
	Потолок из ВГКЛ, покраска цвет белый	30,70
	Потолок из ВГКЛ на отм. +2.600, покраска цвет черный	17,50

Условные обозначения:

+2,700 – Отметка уровня от чистого пола (основная)

-0,250 – Отметка уровня от верхнего прекрытия

– Встроенный карниз для портьерных штор

– Встроенный профиль для передвижных пеперегородок


1800 – Длина профиля

Примечание:

1. Количество материалов в спецификации посчитано БЕЗ ЗАПАСА.
2. Точный цвет краски указан в комплектации.
3. Все отверстия в потолке под осветительные приборы выполнять после покупки освещения.
4. Учесть высоту встраеваемых светильников и других приборов.
5. Сечения см. л. 18.

ПЛАН ПОТОЛКА

№ проекта	Раздел	Стадия	Лист	Листов
	АИ	РП	17	

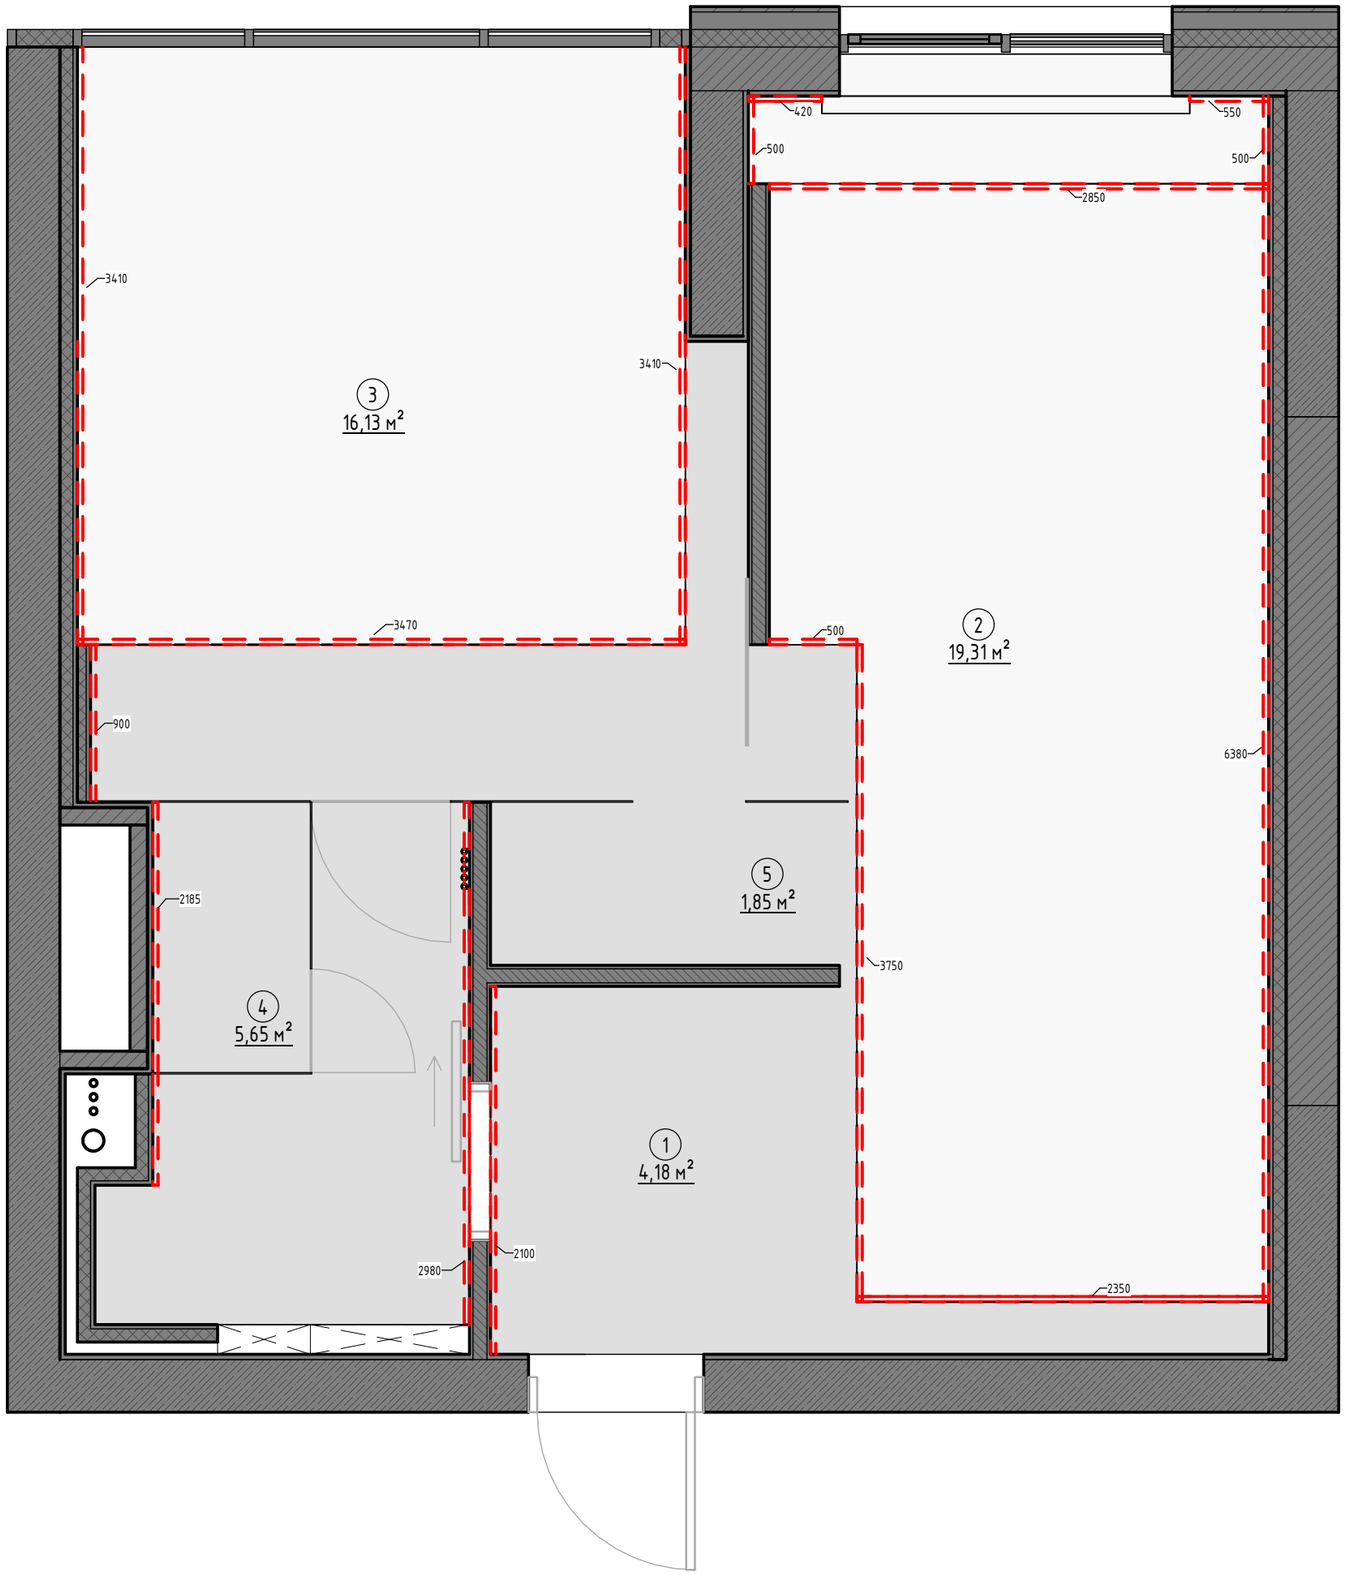


Экспликация помещений

Номер	Наименование	Площадь, кв.м.
1	Прихожая	4,18
2	Кухня-гостинная	19,31
3	Спальня	16,13
4	Санузел	5,65
5	Гардероб	1,85
		47,12

Спецификация потолочного плинтуса

Изображение	Описание	Кол-во, пог.м.
— — —	Профиль алюминевый	37,8

Устройство теневого зазора

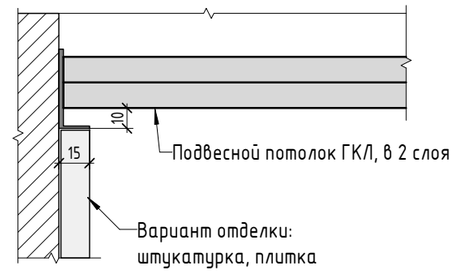


*Смотреть совместно с ПЛАНОМ ОТДЕЛКИ (л. 26)

Примечание:

1. Все размеры уточнить по месту.

ПЛАН РАСПОЛОЖЕНИЯ ТЕНЕВОГО ЗАЗОРА

№ проекта	Раздел	Стадия	Лист	Листов
	АИ	РП	19	

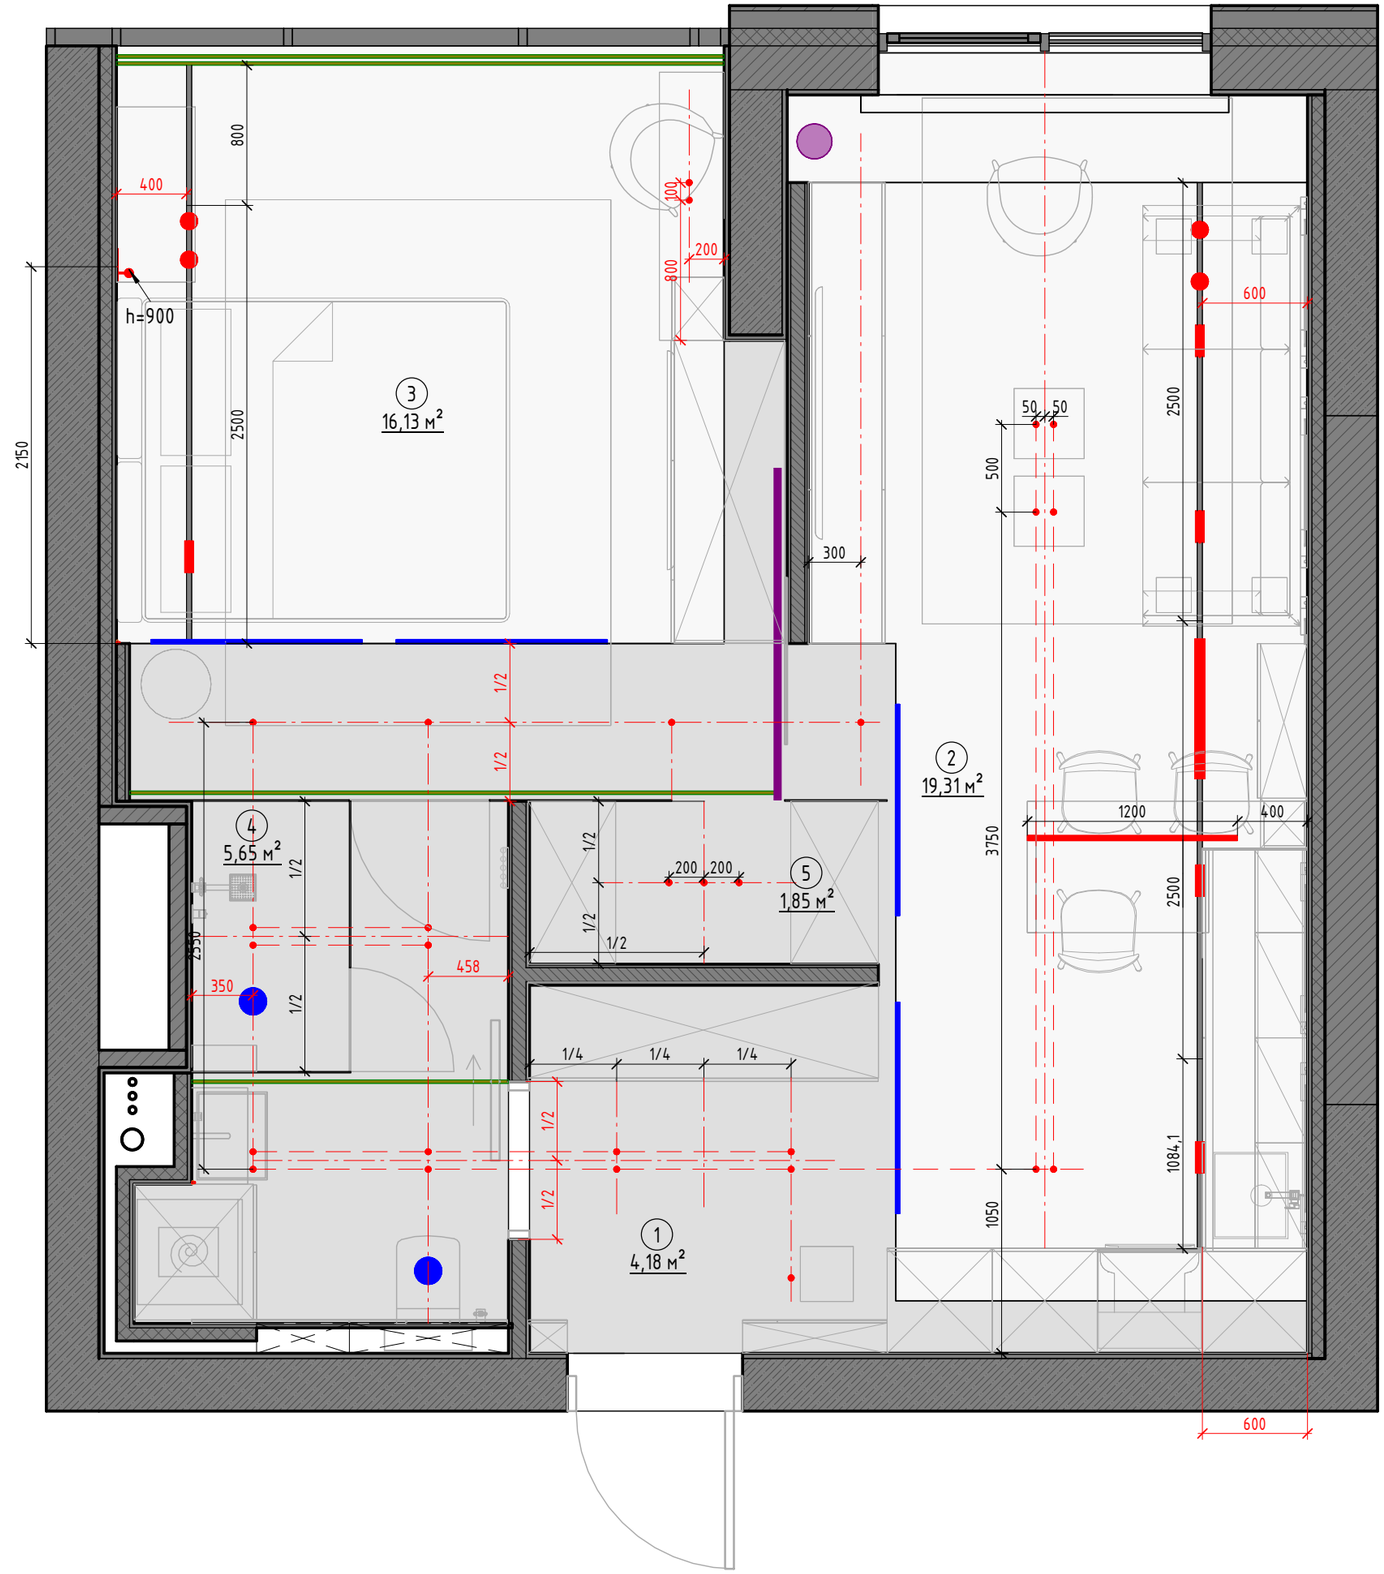

Экспликация помещений		
Номер	Наименование	Площадь, кв.м.
1	Прихожая	4,18
2	Кухня-гостинная	19,31
3	Спальня	16,13
4	Санузел	5,65
5	Гардероб	1,85
		47,12

Условные обозначения:


- Потолочные осветительные приборы
- Трековая система, встроенная в потолок
- Встроенный карниз для портьерных штор
- Встроенный профиль для передвижных пеперегородок
- Вентиляционные решетки
- Профиль со светодиодной лентой
- Линии постороения

Примечание:

1. Все размеры уточнить по месту.
2. Все отверстия в потолке под осветительные приборы выполнять после покупки освещения.
3. Учесть высоту встраеваемых светильников и других приборов.
4. Маркировку осветительного оборудования см. лист 21.
5. СПЕЦИФИКАЦИЮ ОСВЕТИТЕЛЬНЫХ ПРИБОРОВ см. лист 22.
6. Размеры со знаком * уточнить по месту.

ПЛАН РАССТАНОВКИ ОСВЕТИТЕЛЬНОГО ОБОРУДОВАНИЯ

№ проекта	Раздел	Стадия	Лист	Листов
	АИ	РП	20	

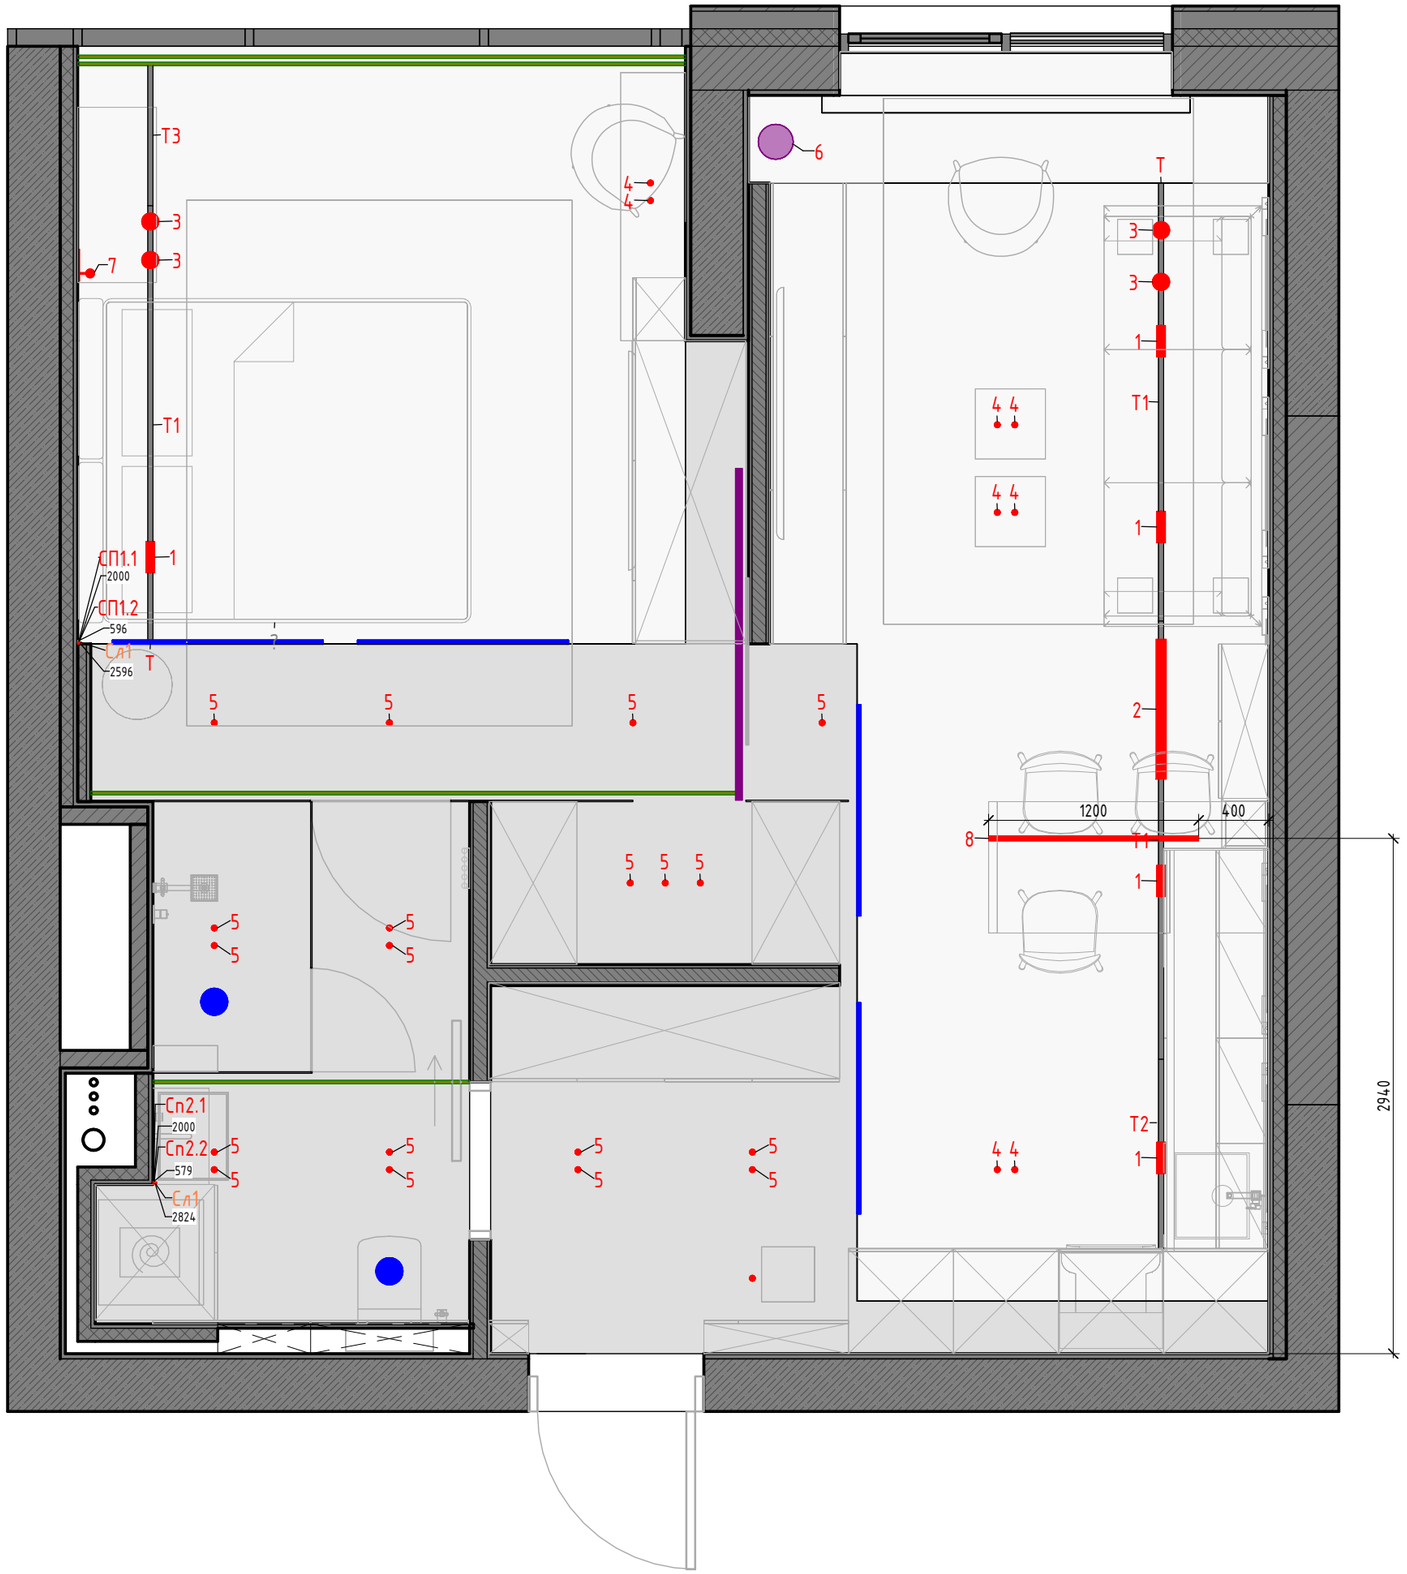

Экспликация помещений		
Номер	Наименование	Площадь, кв.м.
1	Прихожая	4,18
2	Кухня-гостинная	19,31
3	Спальня	16,13
4	Санузел	5,65
5	Гардероб	1,85
		47,12

Условные обозначения:

- 2 – Марка осветительных приборов
- – Потолочные осветительные приборы
- – Трековая система, встроенная в потолок
- – Встроенный карниз для портьерных штор
- – Встроенный профиль для передвижных пеперегородок
- – Вентиляционные решетки
- – Профиль со светодиодной лентой
- – Светодиодная лента
- Т1 – Марка встроенного трека
- Сл1 – Марка светодиодной ленты
- Сп1 – Марка профиля для светодиодной ленты
- 2700 – Длина вертикальных осветительных приборов

Примечание:

1. Привязку осветительного оборудования см. л. 20
2. Все отверстия в потолке под осветительные приборы выполнять после покупки освещения.
3. Учесть высоту встраеваемых светильников и других приборов.
4. СПЕЦИФИКАЦИЮ ОСВЕТИТЕЛЬНЫХ ПРИБОРОВ см. лист 22.

ПЛАН МАРКИРОВКА ОСВЕТИТЕЛЬНОГО ОБОРУДОВАНИЯ

№ проекта	Раздел	Стадия	Лист	Листов
	АИ	РП	21	

Спецификация осветительных приборов (шт.)

Тип	Изображение	Описание	Кол-во , шт
1		Светильник ЦЕНТРСВЕТ D LINE, 180x51x47 мм	5
2		Светильник ЦЕНТРСВЕТ INF DIRECT LINE 270, 800x24,5x48 мм	1
3		Светильник ЦЕНТРСВЕТ INF LOCUS M DALI, d52x90 мм	4
4		Светильник ЦЕНТРСВЕТ POINT S, белый, d35 мм	8
5		Светильник ЦЕНТРСВЕТ POINT S, черный, d35 мм	20
6		Настольная лампа	1
7		Настенный точечный светильник	1
8		Подвесной светильник, 30x1200xh100	1

Спецификация осветительных приборов (пог.м.)

Тип	Изображение	Описание	Кол-во, пог.м.
Сл		Светодиодная лента	5,4
Сп1		Профиль 10x10 мм	2,6
Сп2		Профиль, 15x15 мм	2,6
Т		Трек встроенный ЦЕНТРСВЕТ INFINITY	9,4

Спецификация встроенного трека

Марка	Описание	Длина, пог.м.	Кол-во, шт
Т1	Трек встроенный ЦЕНТРСВЕТ INFINITY	2,5	3
Т2	Трек встроенный ЦЕНТРСВЕТ INFINITY	1,1	1
Т3	Трек встроенный ЦЕНТРСВЕТ INFINITY	0,8	1

Спецификация профиля для светодиодной ленты

Марка	Описание	Длина, пог.м.	Кол-во, шт
СП1.1	Профиль 10x10 мм	2,0	1
СП1.2	Профиль 10x10 мм	0,6	1
Сп2.1	Профиль, 15x15 мм	2,0	1
Сп2.2	Профиль, 15x15 мм	0,6	1

Спецификация светодиодной ленты


Марка	Описание	Длина, пог.м.	Кол-во, шт
Сл1	Светодиодная лента	<варианты>	2

Примечание:

1. Смотреть совместно с ПЛАНОМ МАРКИРОВКИ ОСВЕТИТЕЛЬНОГО ОБОРУДОВАНИЯ (лист 21)

СПЕЦИФИКАЦИЯ ОСВЕТИТЕЛЬНОГО ОБОРУДОВАНИЯ

№ проекта	Раздел	Стадия	Лист	Листов
	АИ	РП	22	

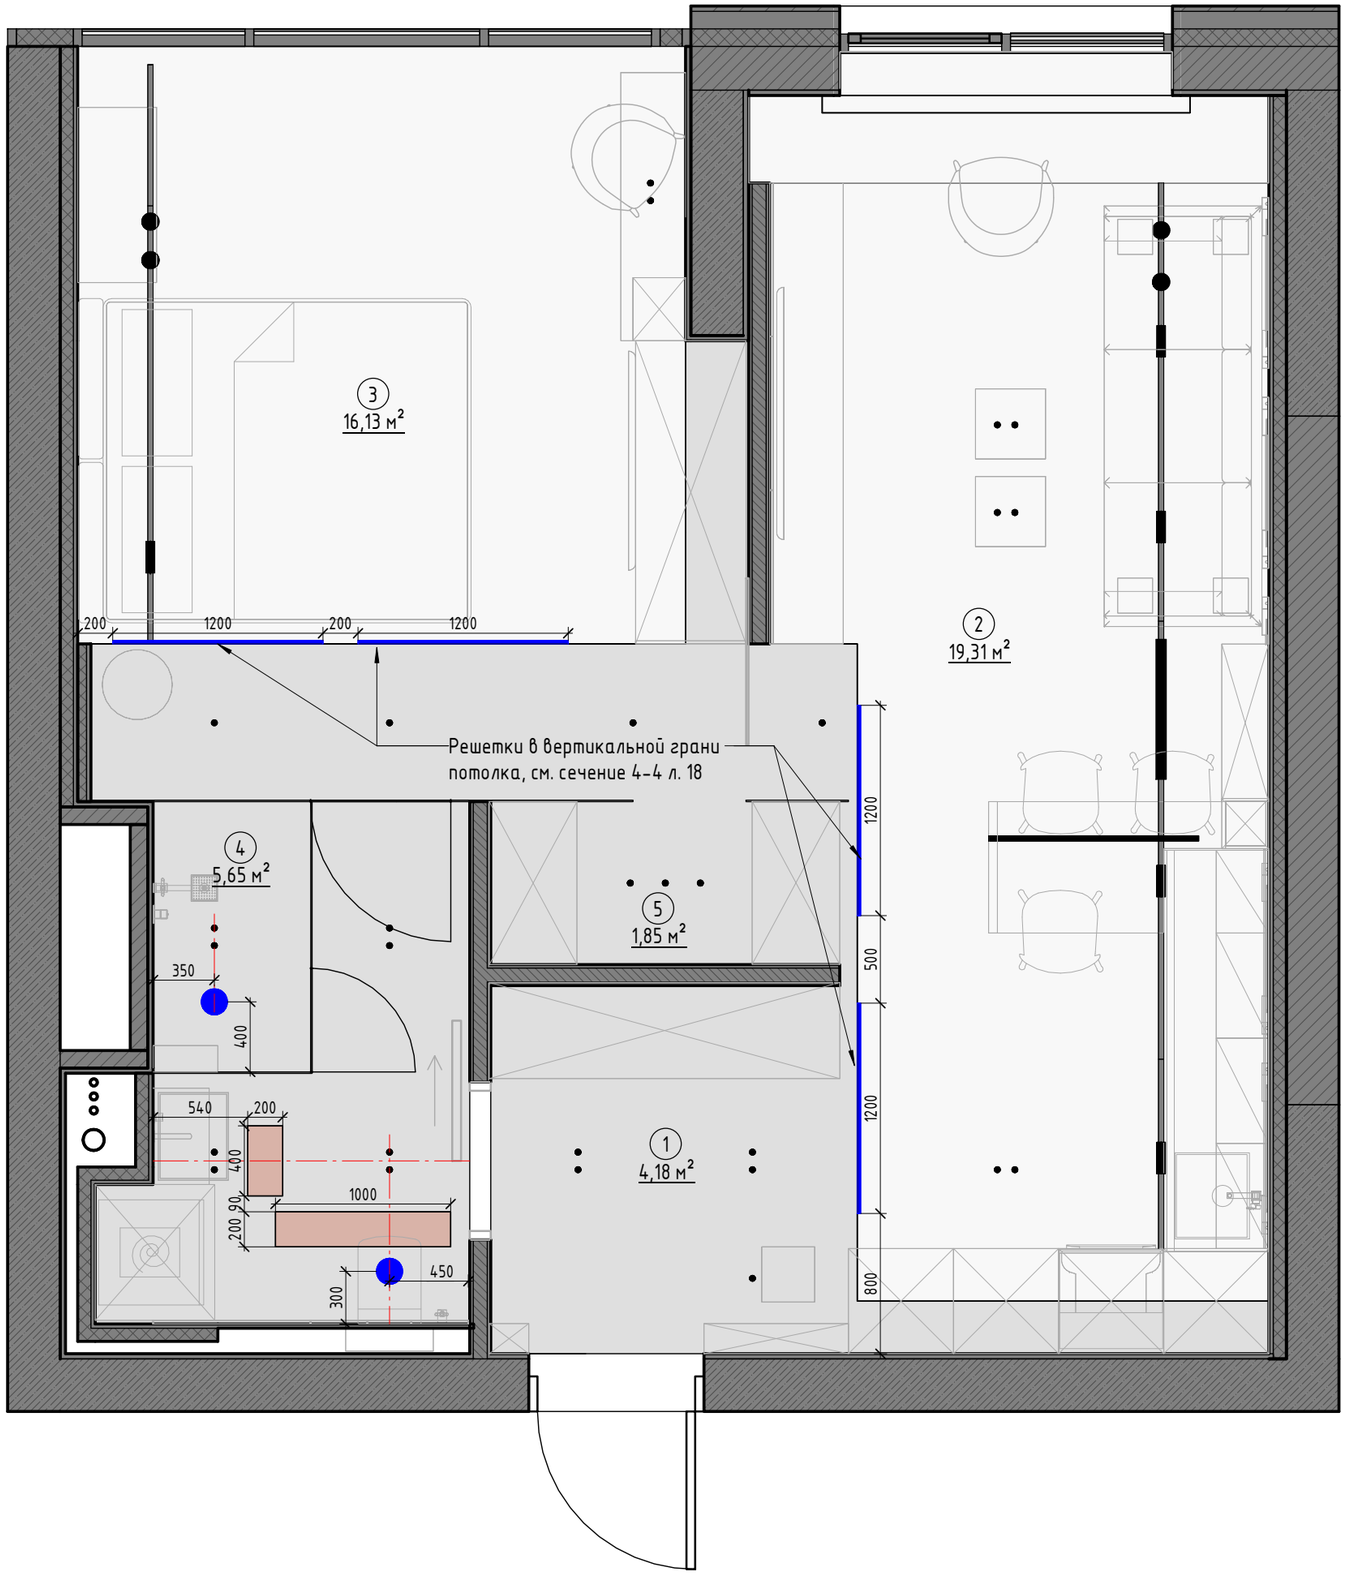

Экспликация помещений		
Номер	Наименование	Площадь, кв.м.
1	Прихожая	4,18
2	Кухня-гостинная	19,31
3	Спальня	16,13
4	Санузел	5,65
5	Гардероб	1,85
		47,12

Условные обозначения:

- Вент. решетки
- Люки доступа
- Потолочные осветительные приборы
- Трековая система, встроенная в потолок
- Линии построения


Примечание:

1. Все размеры уточнить по месту.
2. Учесть высоту встраеваемых элементов.

ПЛАН ВЕНТИЛЯЦИИ

№ проекта	Раздел	Стадия	Лист	Листов
	АИ	РП	23	

Экспликация помещений		
Номер	Наименование	Площадь, кв.м.
1	Прихожая	4,18
2	Кухня-гостинная	19,31
3	Спальня	16,13
4	Санузел	5,65
5	Гардероб	1,85
		47,12

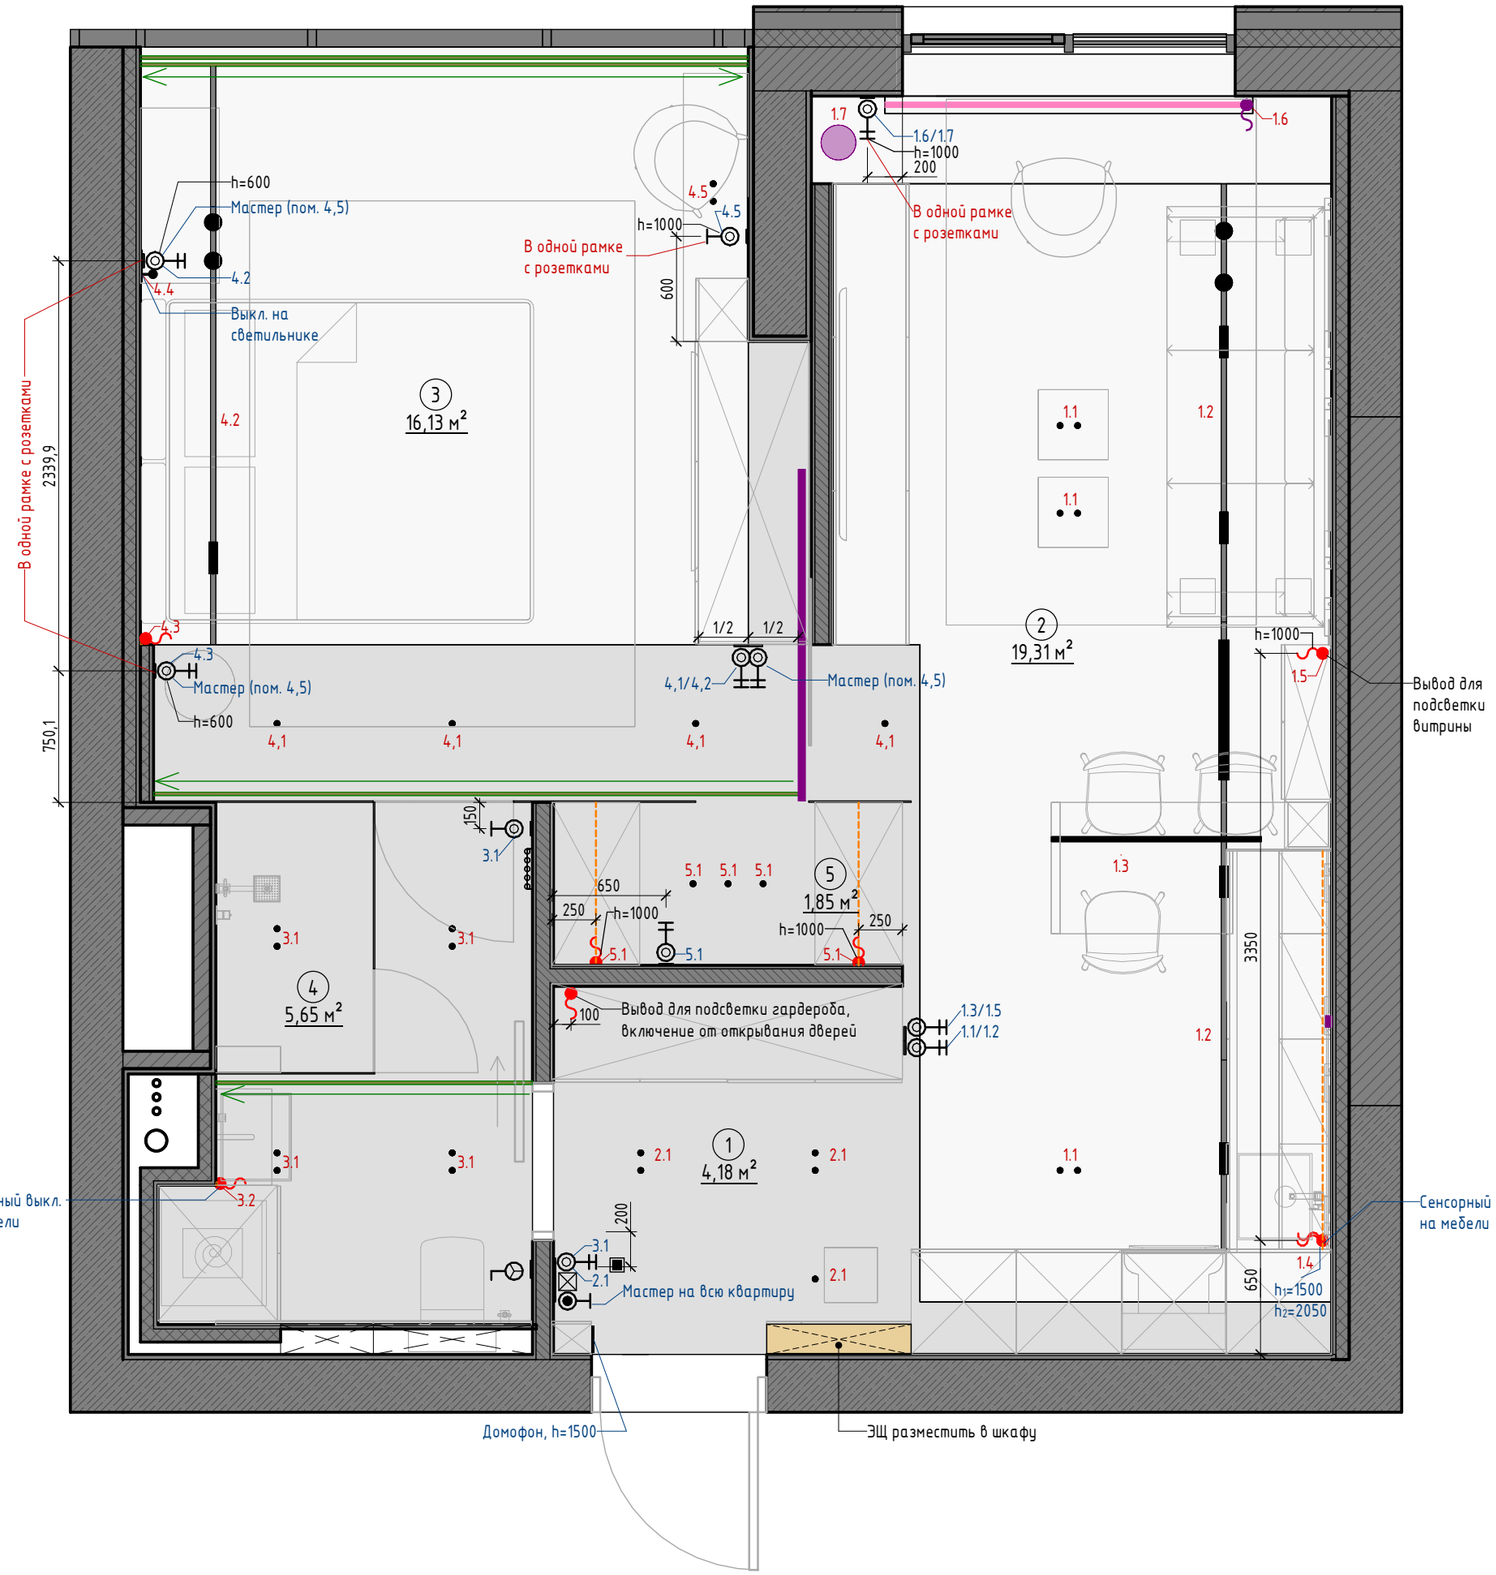

Условные обозначения:


- 5 Группа включения
- 5 – Потолочные осветительные приборы
- 5 – Трековая система, встроенная в потолок
- – Встроенный карниз для портьерных штор
- – Встроенный профиль для передвижных пеперегородок
- – Жалюзи
- 5 – Профиль со светодиодной лентой
- – Подсветка мебели
- 5 – Вывод провода слаботочный (для светодиодной ленты)
- 5 – Вывод провода 220В
- 5 – Переключатель одноклавишный
- 5 – Переключатель двухклавишный
- 5 Группа включения


Примечание:


1. Высота выключателей по умолчанию 900 мм от чистого пола, если не указана другая.
2. Выводы по умолчанию делать на -50 от потолка, если не указана другая высота. Вывод для подсветки потолка в нише для подсветки.
3. Все высоты указаны от чистового пола.
4. СМОТРЕТЬ СОВМЕСТНО С РАЗВЕРТКАМИ ПОМЕЩЕНИЙ.

ПЛАН УПРАВЛЕНИЯ СВЕТОМ

№ проекта	Раздел	Стадия	Лист	Листов
	АИ	РП	24	

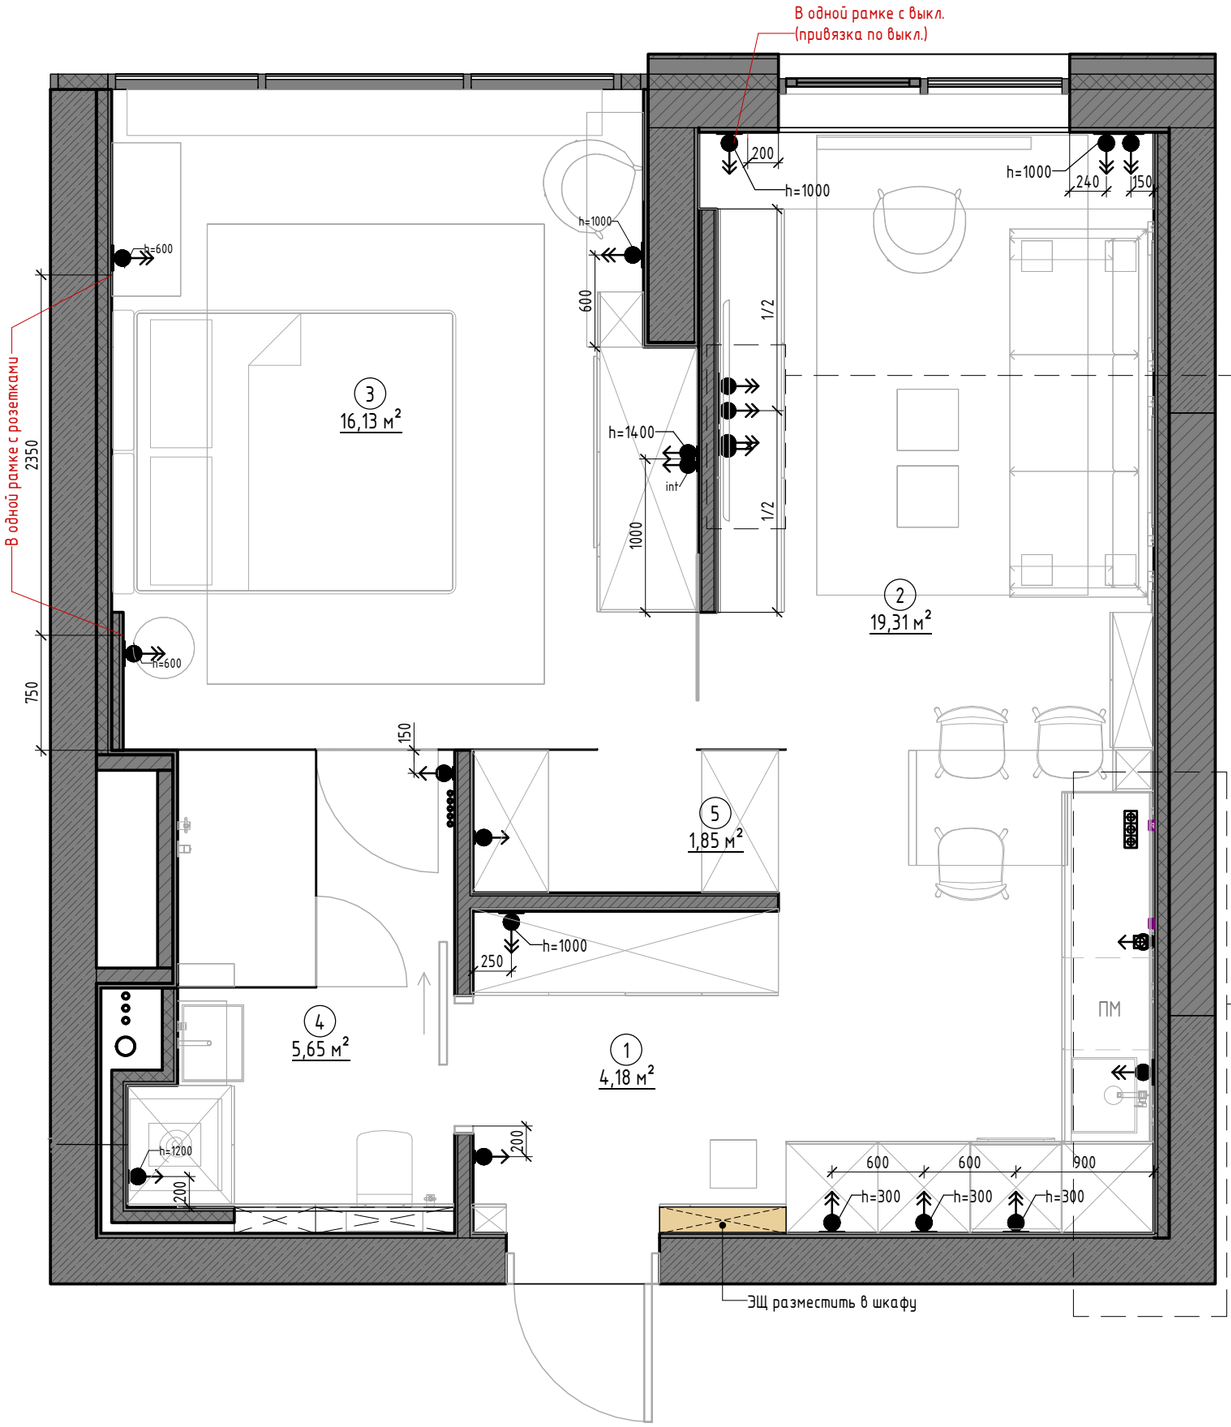

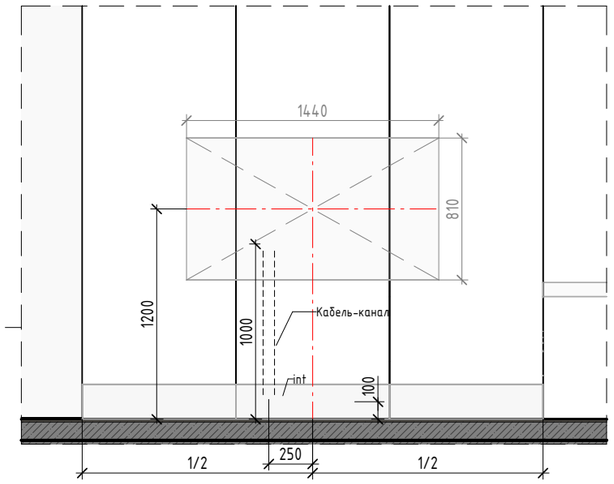

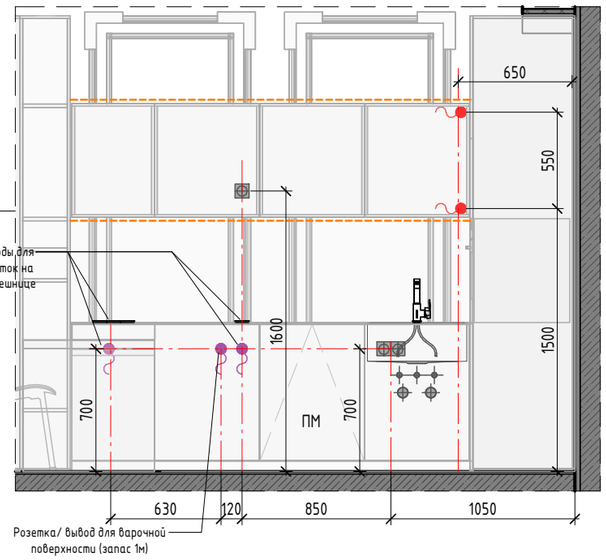

Экспликация помещений

Номер	Наименование	Площадь, кв.м.
1	Прихожая	4,18
2	Кухня-гостинная	19,31
3	Спальня	16,13
4	Санузел	5,65
5	Гардероб	1,85
		47,12

Условные обозначения:

5 – Управляемая розетка для торшера

– Розетка 220V, одинарная

– Розетка 220V, двойная

– Розетка 220V, тройная

– Розетка 220V, четверная

– Вывод провода 220V

– Вывод провода слаботочный (для светодиодной ленты)


int – Розетка для интернета

Примечание:

1. Высота розеток по умолчанию 200 мм от уровня чистого пола до середины розетки.
2. Розетки во "влажных" помещениях должны быть защищены УЗО (устройство защитного отключения)с током срабатывания до 30мА.
3. Укладку проводов по потолку необходимо производить не ближе, чем 300мм от угла и стен.
4. Все высоты указаны от чистового пола.
5. СМОТРЕТЬ СОВМЕСТНО С РАЗВЕРТКАМИ ПОМЕЩЕНИЙ.

ПЛАН РОЗЕТОК

№ проекта	Раздел	Стадия	Лист	Листов
	АИ	РП	25	

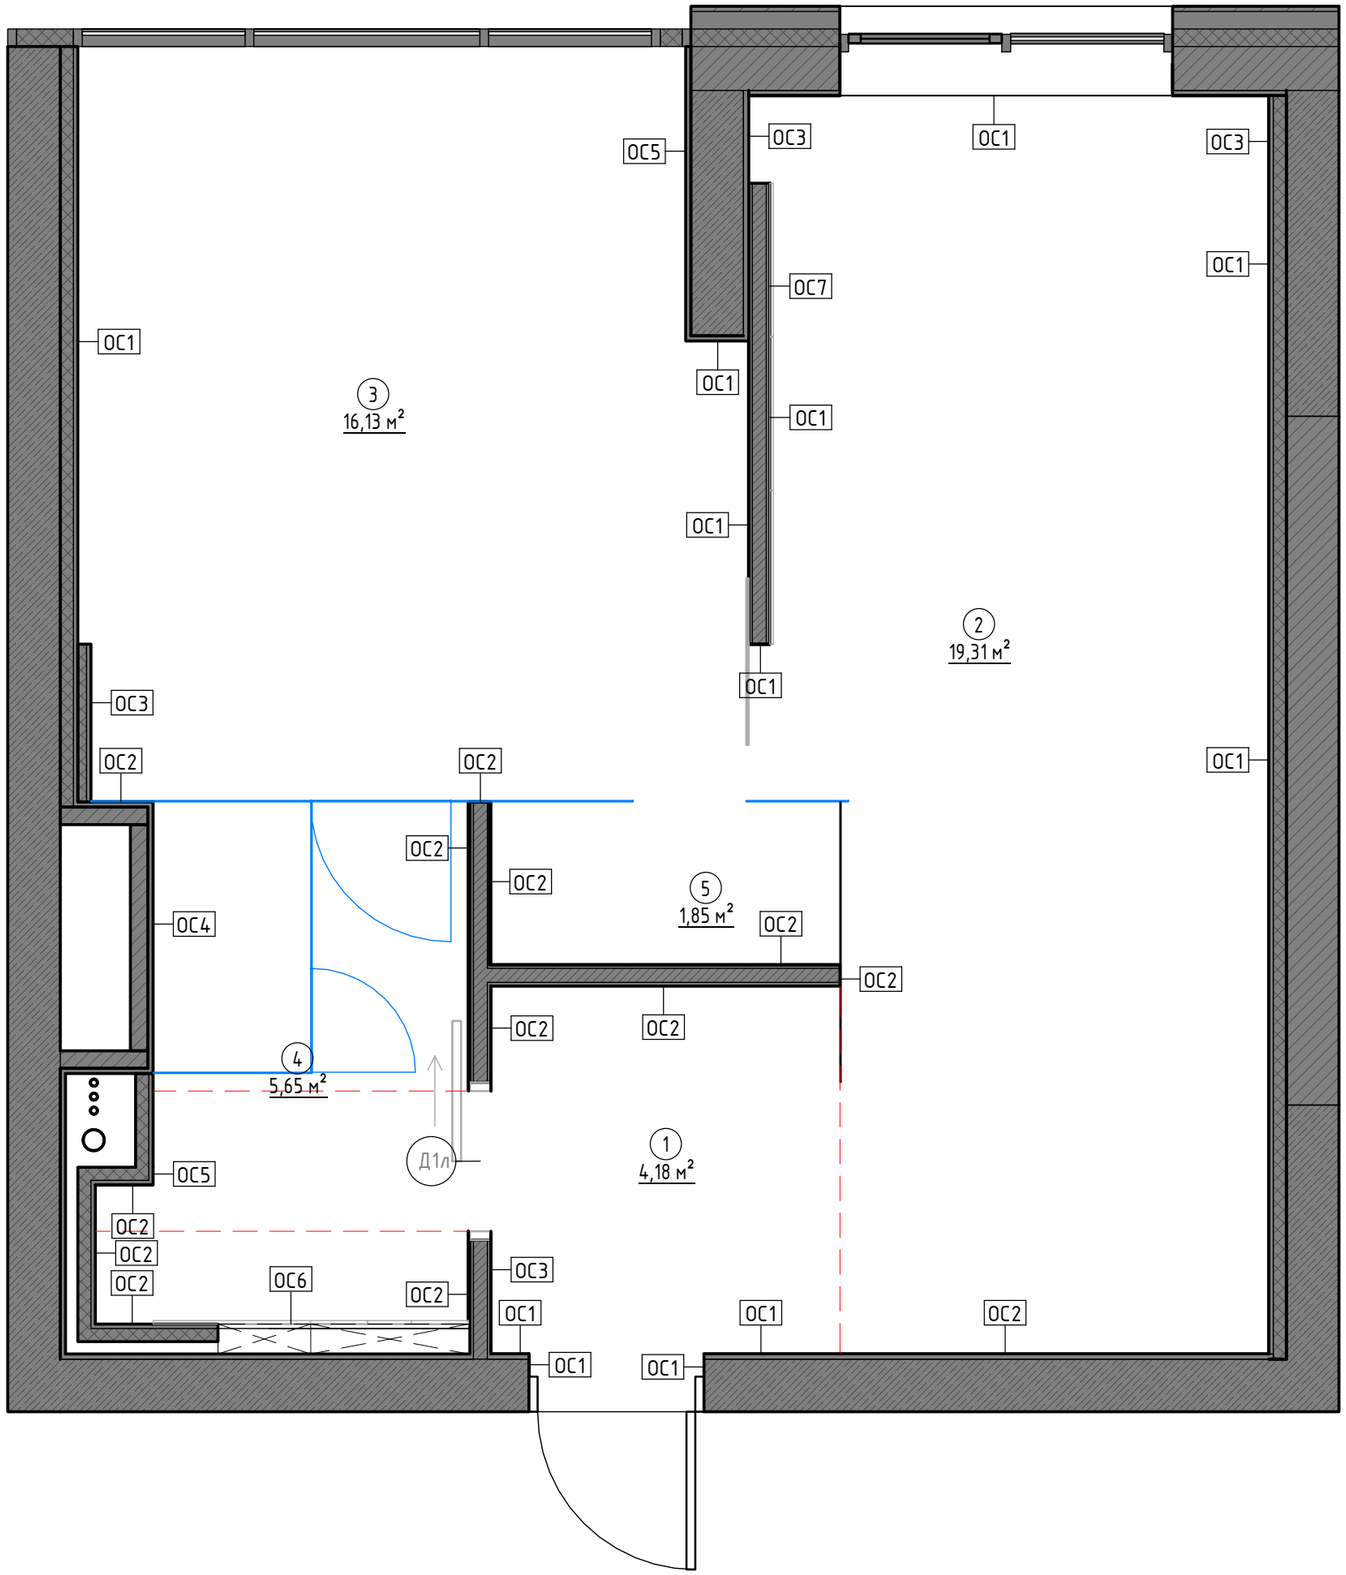

Экспликация помещений		
Номер	Наименование	Площадь, кв.м.
1	Прихожая	4,18
2	Кухня-гостинная	19,31
3	Спальня	16,13
4	Санузел	5,65
5	Гардероб	1,85
		47,12

Спецификация отделки стен		
Тип	Описание	Площадь, кв.м
ОС1	Покраска, цвет белый	46,27
ОС2	Покраска, цвет черный	34,04
ОС3	Зеркало тонированное	7,57
ОС4	Плитка ARCHSKIN WLLPPAPERS 101 DECO 100 W, 1000x1000x5.6 мм	3,87
ОС5	<варианты>	9,08
ОС6	Панели МДФ, цвет белый	4,68
ОС7	Текстильные панели	6,84

Условные обозначения:


ОС1 - Марка отделки стен

Примечание:

1. Количество материалов в спецификации посчитано БЕЗ ЗАПАСА.
2. Точный цвет краски указан в комплектаци.
3. Отделка дверных откосов соответствует отделке помещения, плитка/покраска соответственно помещению.
4. Развертки помещений см. листы 28-32.

ПЛАН ОТДЕЛКИ СТЕН

№ проекта	Раздел	Стадия	Лист	Листов
	АИ	РП	26	

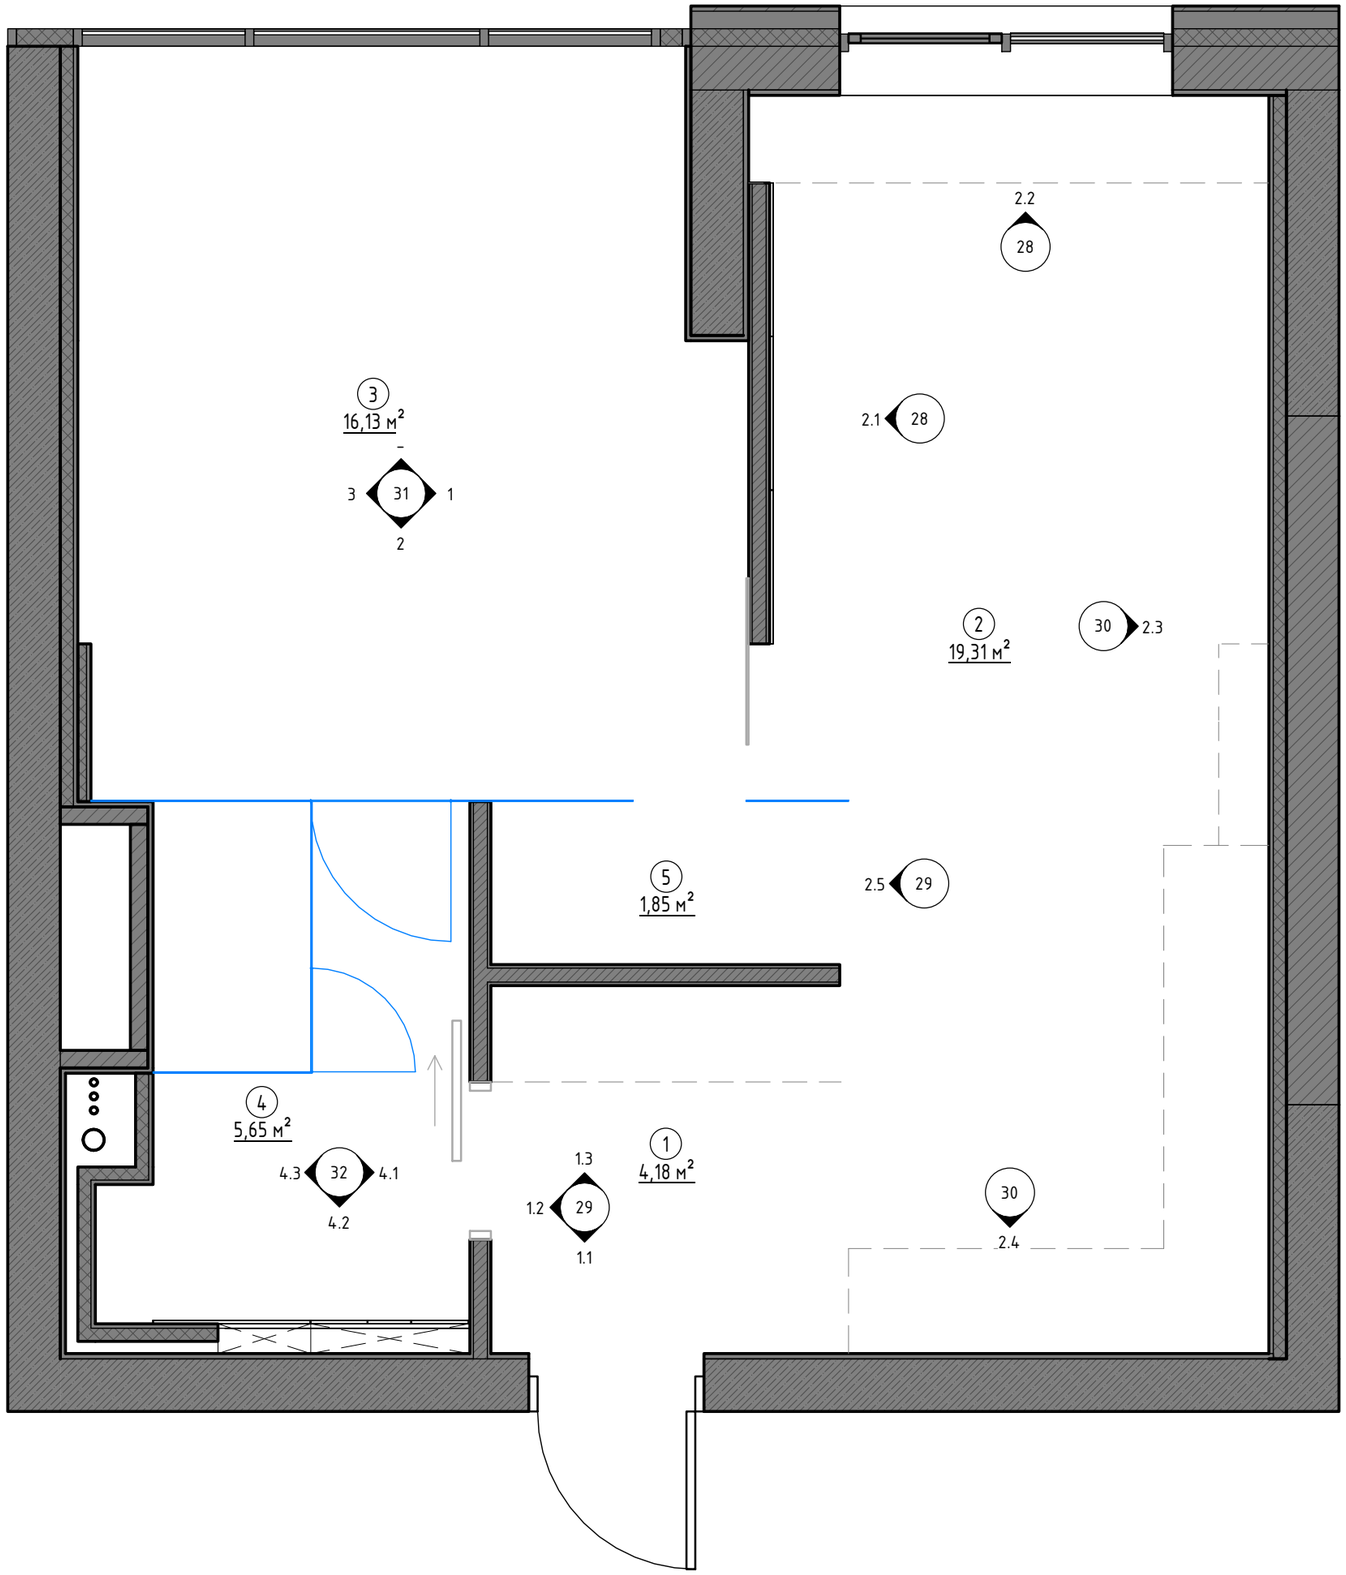

Экспликация помещений		
Номер	Наименование	Площадь, кв.м.
1	Прихожая	4,18
2	Кухня-гостинная	19,31
3	Спальня	16,13
4	Санузел	5,65
5	Гардероб	1,85
		47,12

Условные обозначения:




Примечание:

1. Развертки помещений см. листы 28-32.


ПЛАН РАЗВЕРТОК

№ проекта	Раздел	Стадия	Лист	Листов
	АИ	РП	27	


Вид 1.1

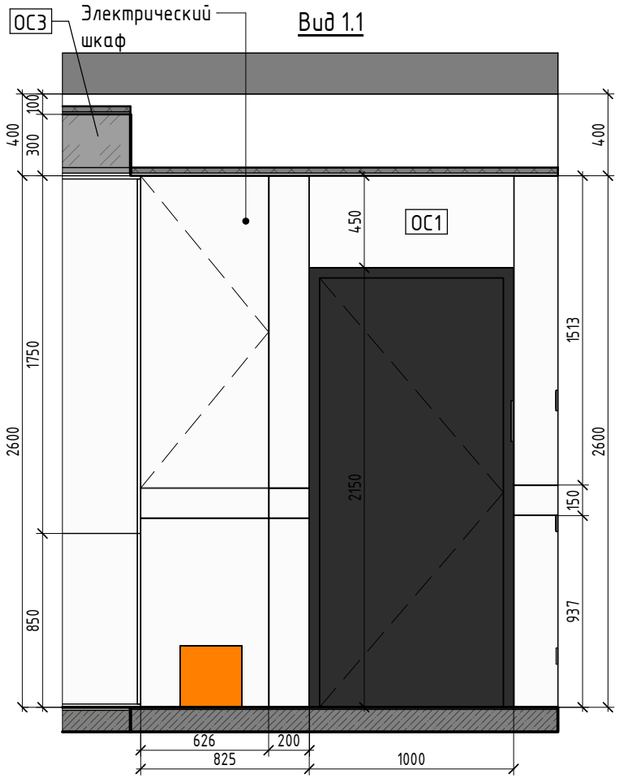

Вид 1.2

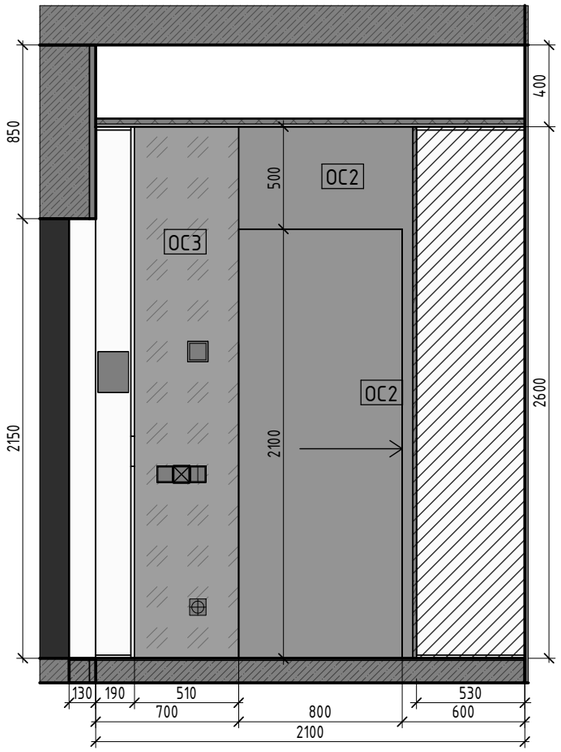

Вид 1.3

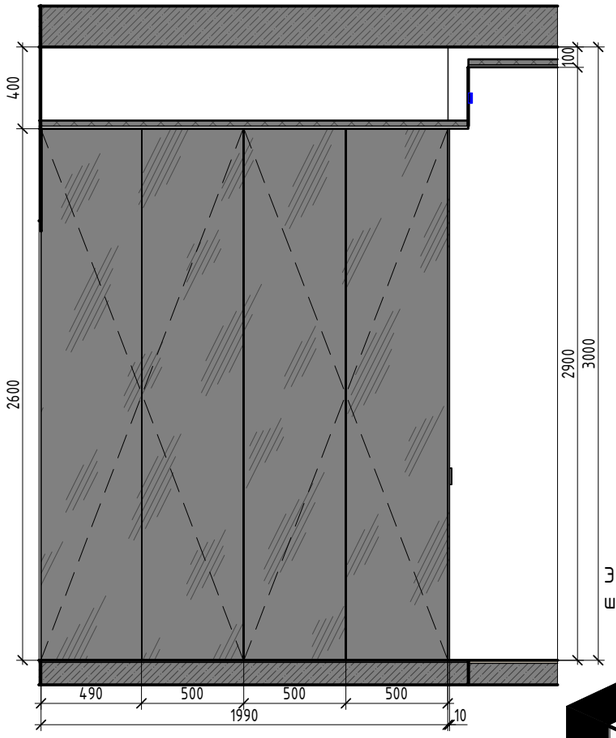

Условные обозначения:

ОС1 – Марка отделки стен


– МДФ, цвет графитовый

– МДФ шпонированный


– Стекло тонированное


– Зеркало тонированное

– Открывание фасадов

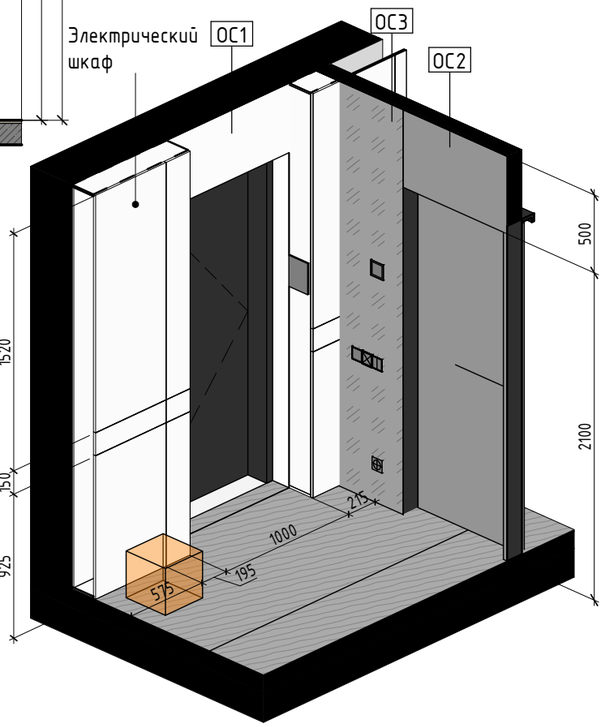

Вид 2.5

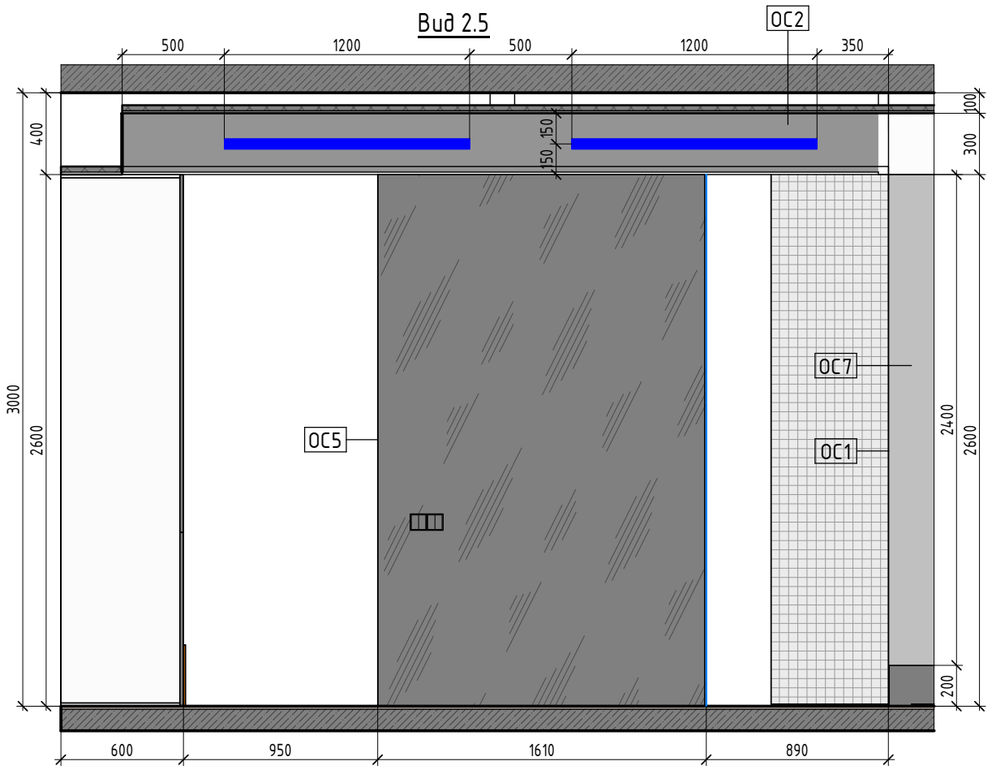


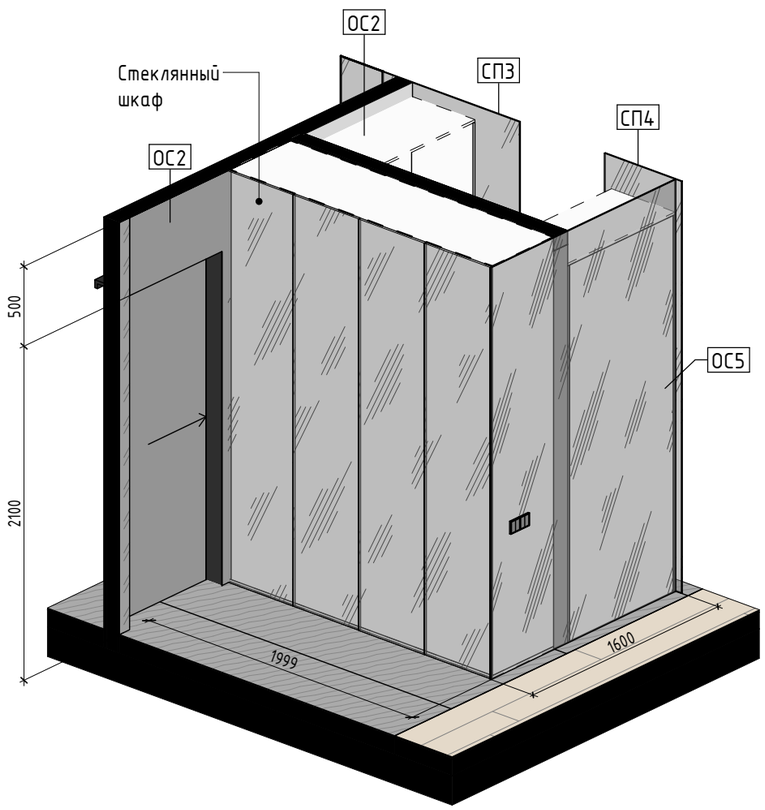


РАЗВЕРТКИ пом. № 1, Прихожая


№ проекта	Раздел	Стадия	Лист	Листов
	АИ	РП	29	

Вид 2.1

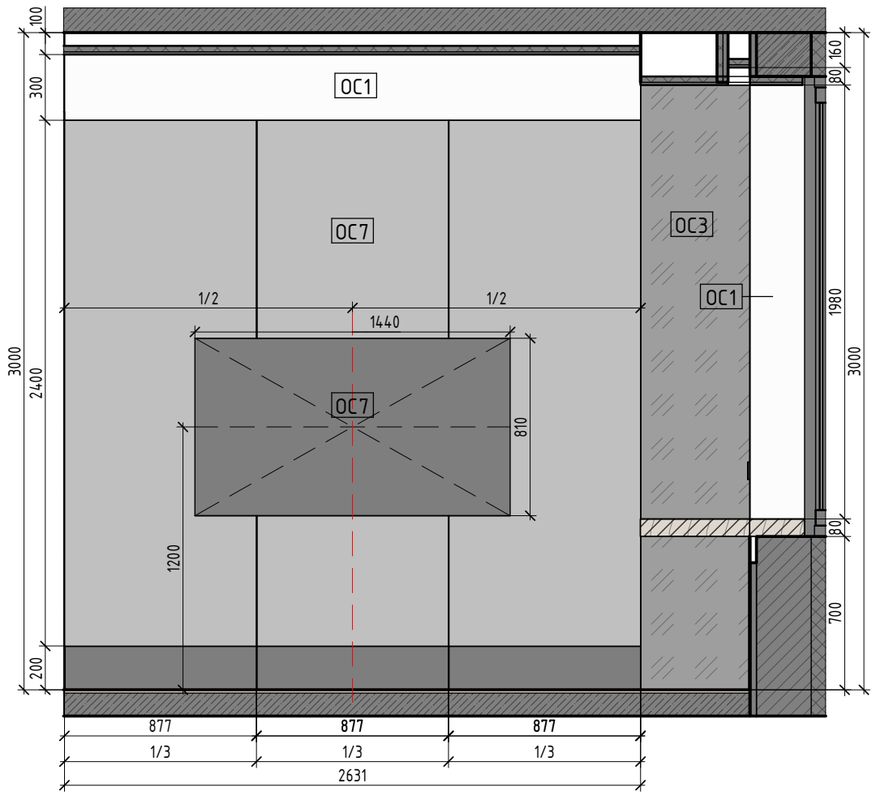

Вид 2.2

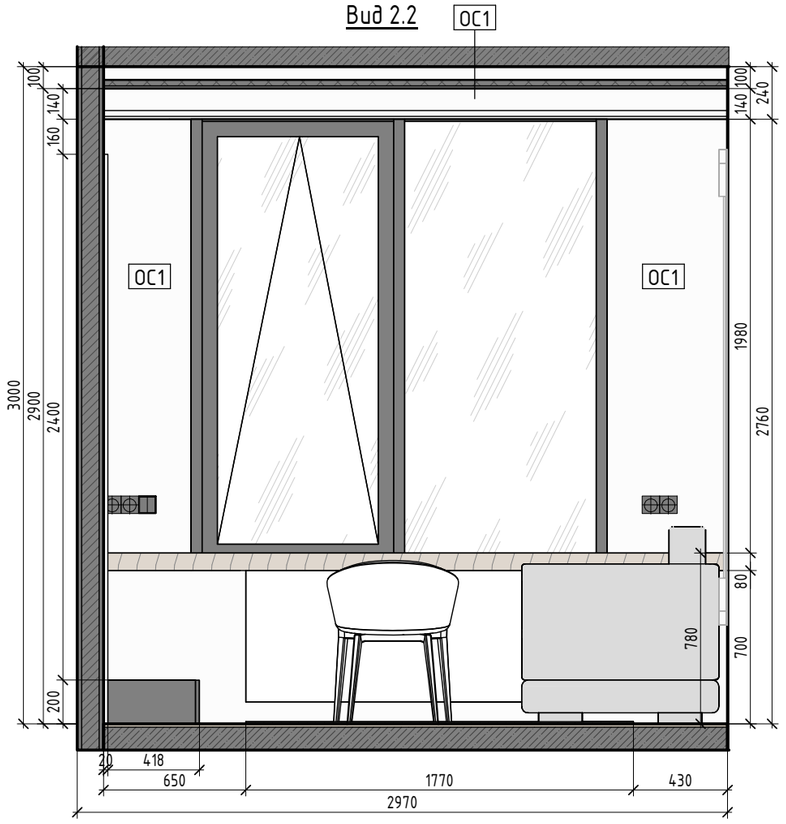

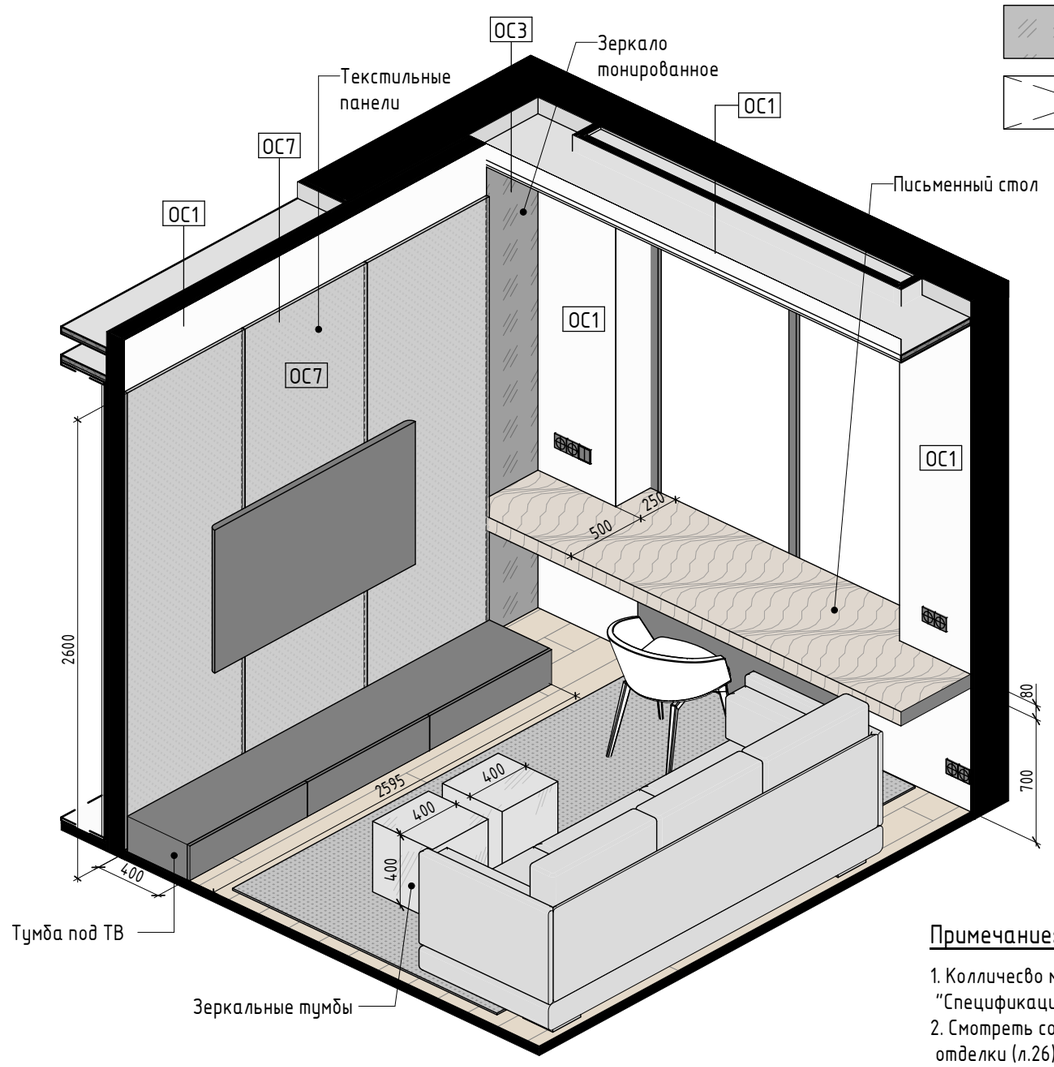

Условные обозначения:

- ОС1 – Марка отделки стен
- – МДФ, цвет графитовый
- – МДФ шпонированный
- – МДФ, отделка тканью
- – Зеркало тонированное
- – Открывание фасадов


Примечание:

1. Колличесво материалов посчитано в "Спецификации отделки", см. лист 26.
2. Смотреть совместно с планами мебели (л.9) и отделки (л.26)
3. Все развертки по мебели разработаны условно и являются заданием для подрядчиков.


РАЗВЕРТКИ пом. № 2, Гостиная


№ проекта	Раздел	Стадия	Лист	Листов
	АИ	РП	28	

Вид 2.3

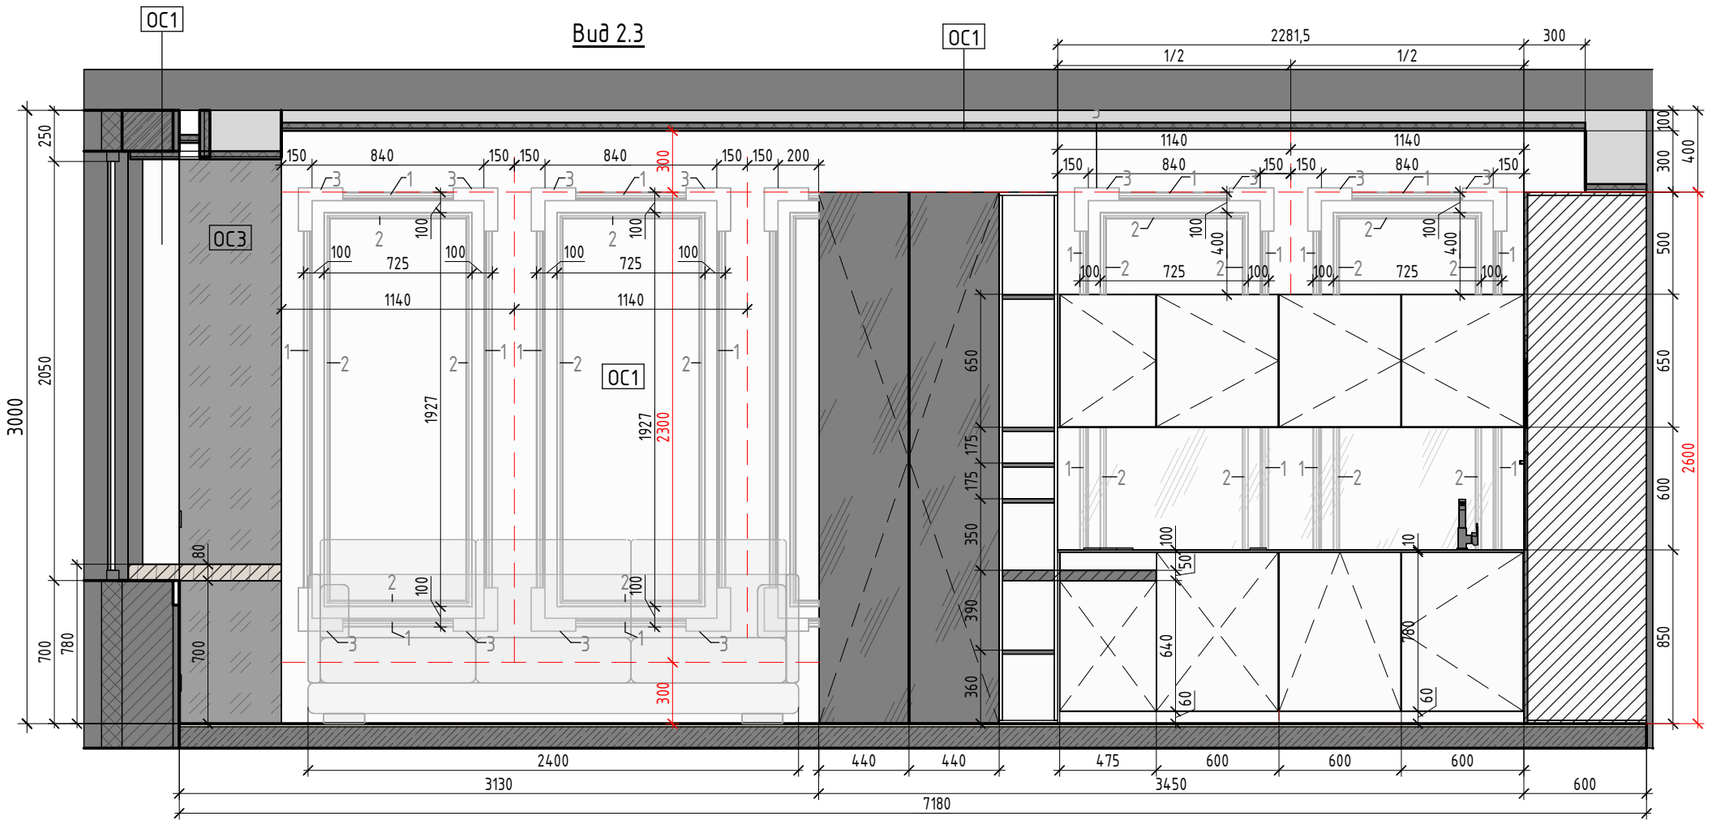

Вид 2.4

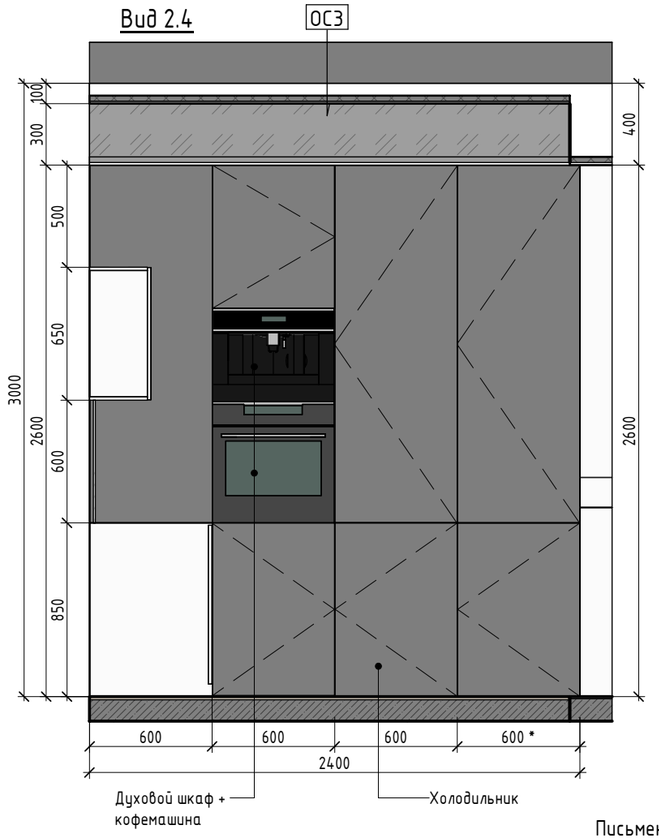

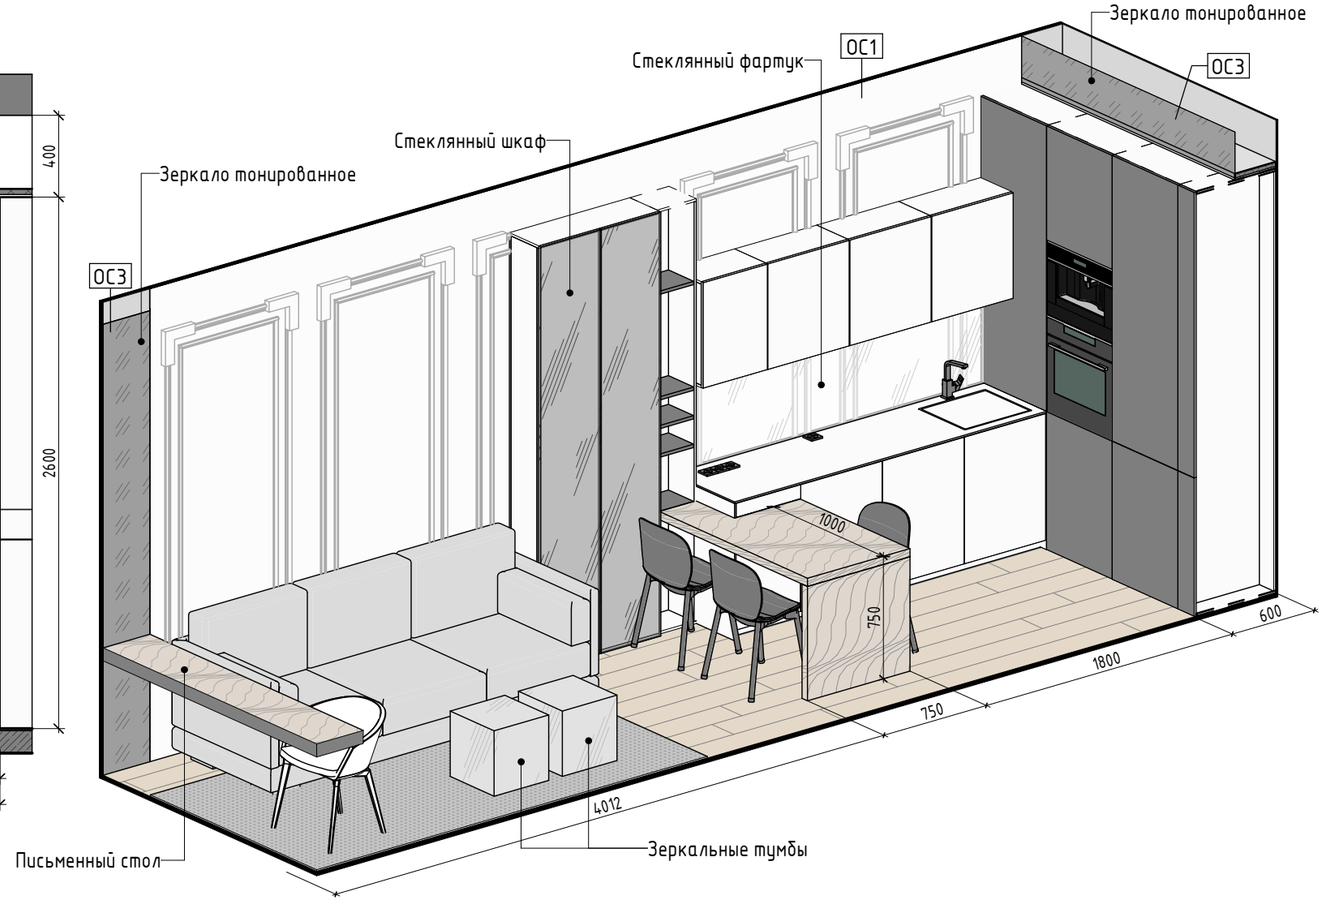

Условные обозначения:

- ОС1 – Марка отделки стен
- – МДФ, цвет графитовый
- – Стекло тонированное
- – Зеркало тонированное
- – Открывание фасадов

Спецификация Молдингов (пог.м)

Марка	Изображение	Описание	Длина, мм
1		Молдинг ORAC DECOR - P4020, 50x29 мм	15693
2		Молдинг ORAC DECOR - P8030, 17x41 мм	18256

Спецификация Молдингов (шт.)

Марка	Изображение	Описание	Кол-во, шт
3		Угол Ду-60, 243x247x38 мм	14


Примечание:

1. Колличесво материалов посчитано в "Спецификации отделки", см. лист 26.
2. Смотреть совместно с планами мебели (л.9) и отделки (л.26)
3. Все развертки по мебели разработаны условно и являются заданием для подрядчиков.


РАЗВЕРТКИ пом. № 2, Кухня

№ проекта	Раздел	Стадия	Лист	Листов
	АИ	РП	30	

Вид 3.1

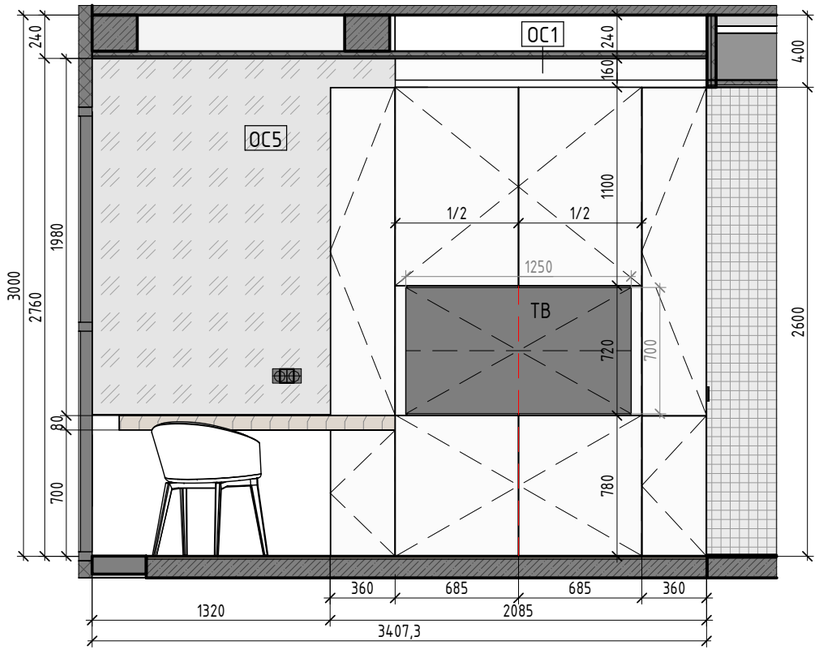

Вид 3.2

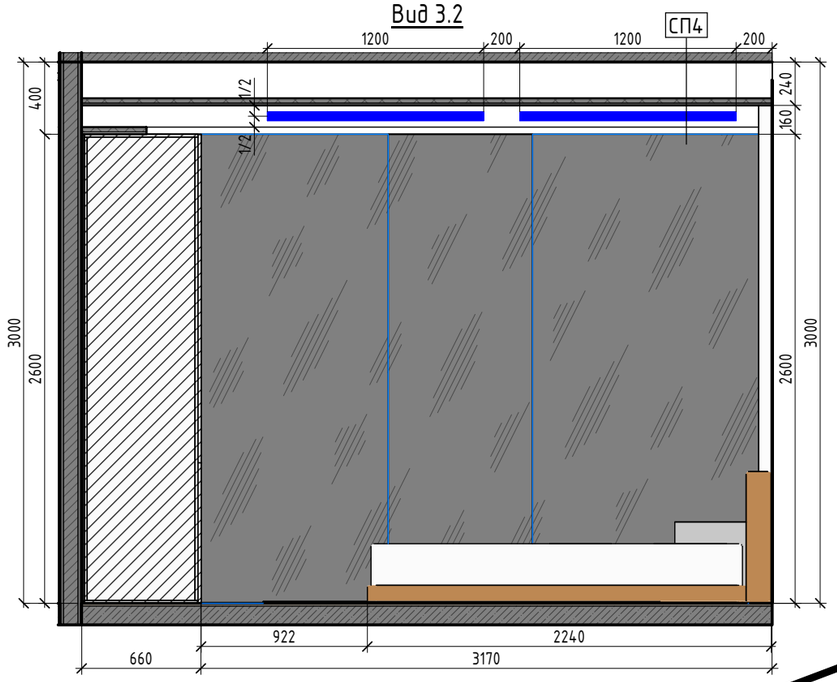

Условные обозначения:

ОС1 – Марка отделки стен


– МДФ, цвет графитовый

– Стекло тонированное


– Зеркало тонированное


– Зеркало

– Открывание фасадов

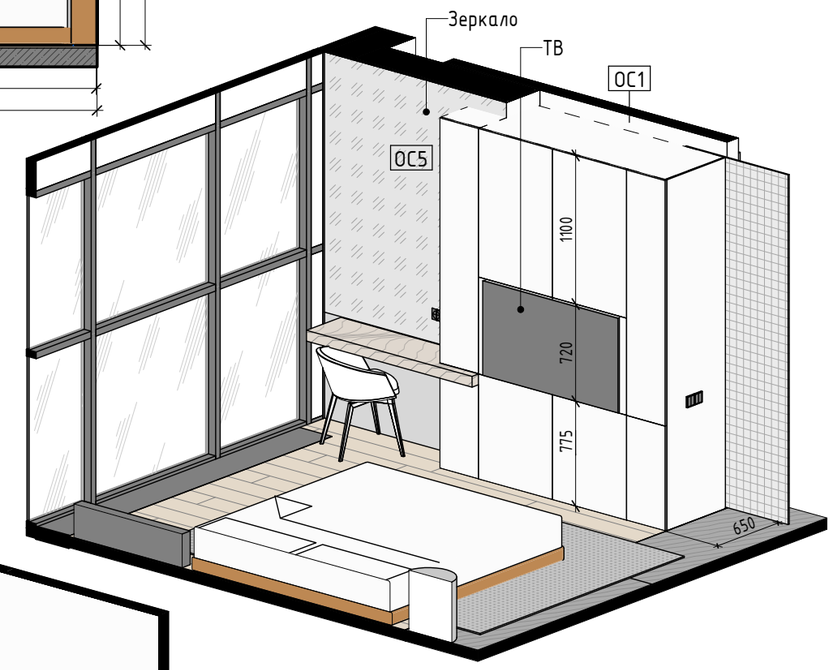

Вид 3.3

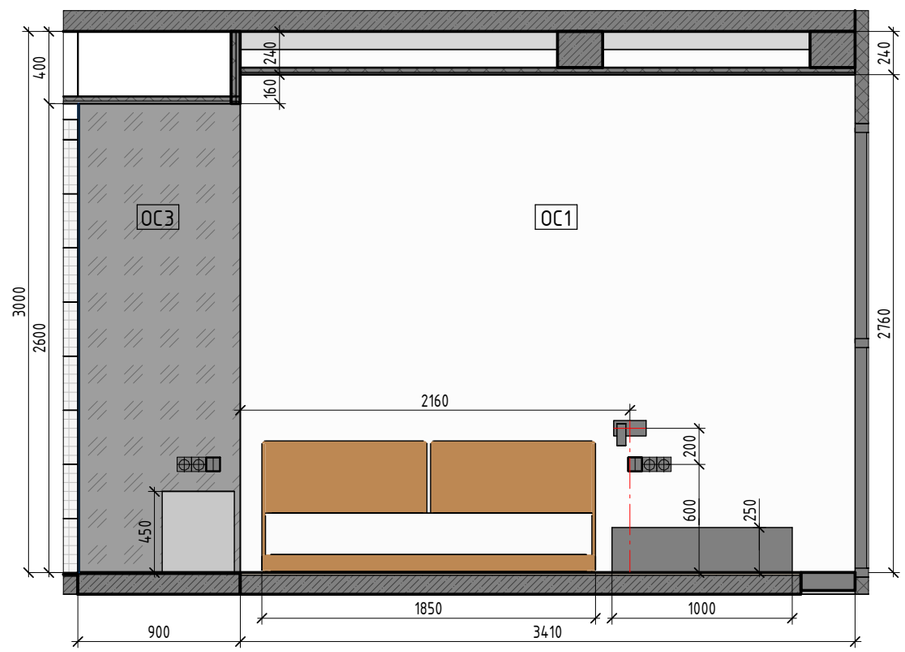

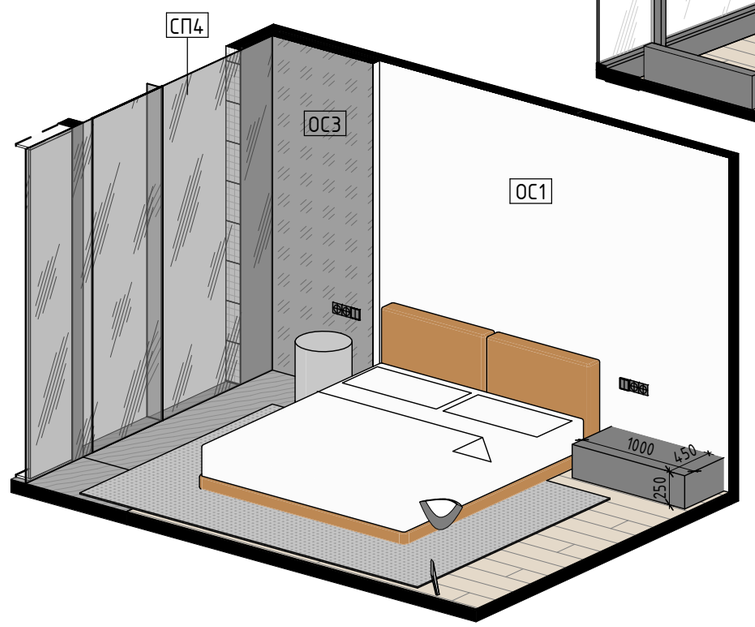


Примечание:

1. Колличесво материалов посчитано в "Спецификации отделки", см. лист 26.
2. Смотреть совместно с планами мебели (л.9) и отделки (л.26)
3. Все развертки по мебели разработаны условно и являются заданием для подрядчиков.


РАЗВЕРТКИ пом. № 3, Сальня

№ проекта	Раздел	Стадия	Лист	Листов
	АИ	РП	31	


Вид 4.1

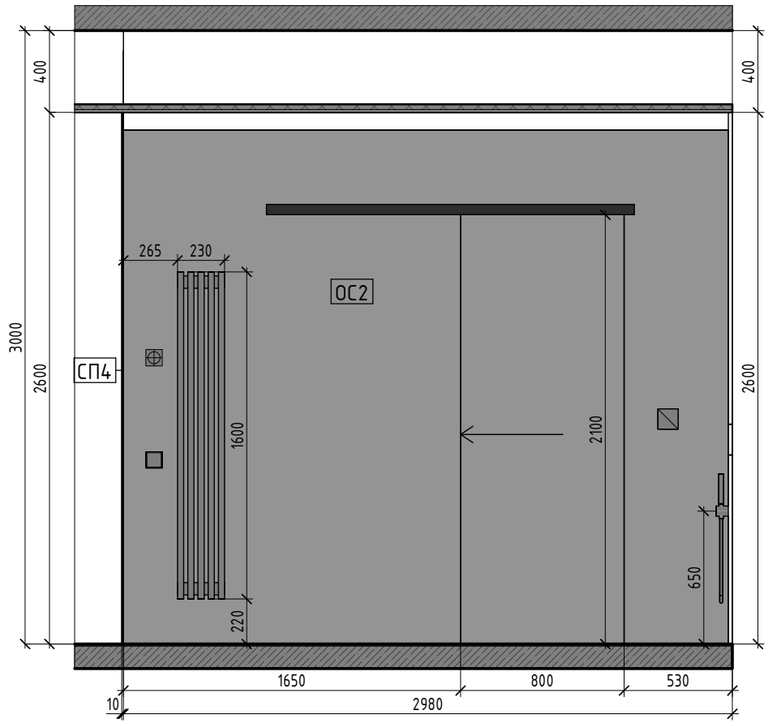


Вид 4.2

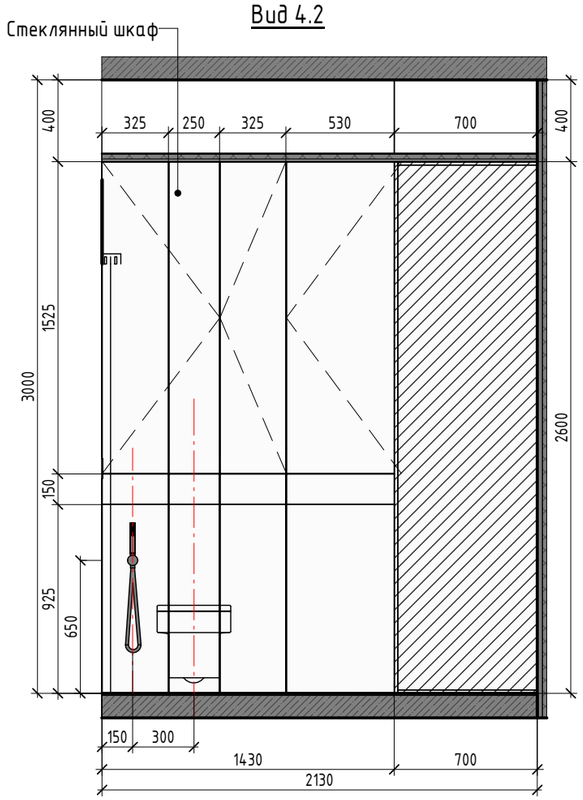

Вид 4.3

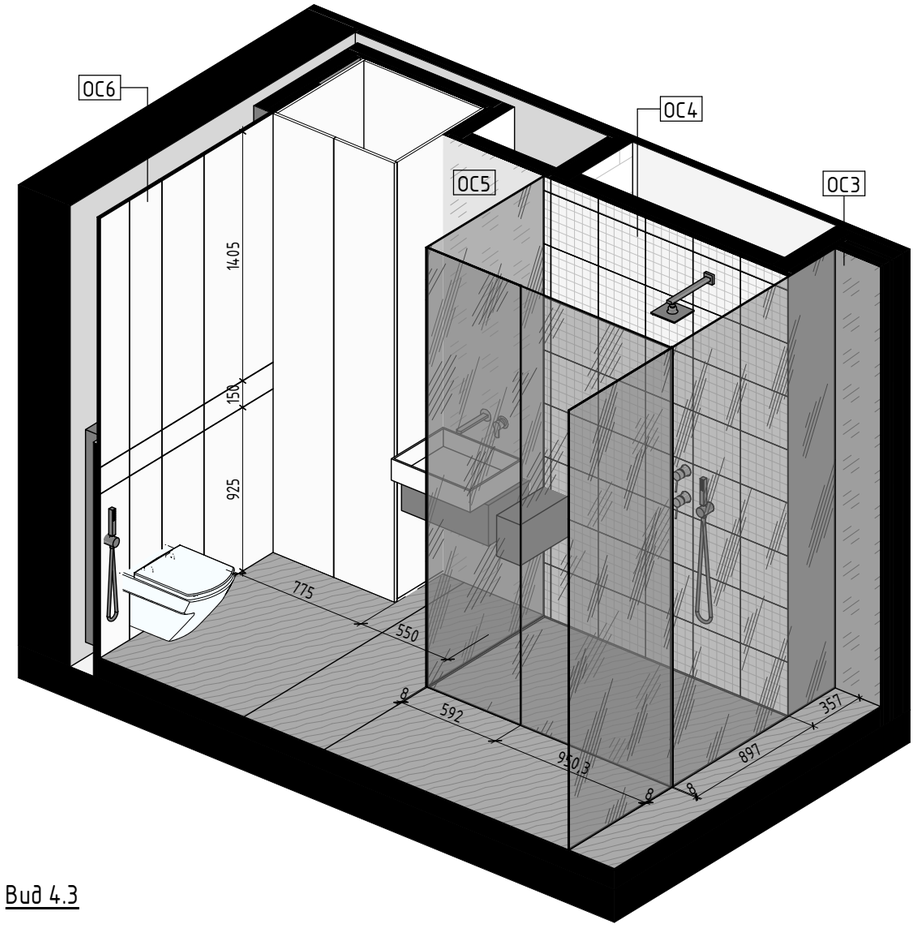

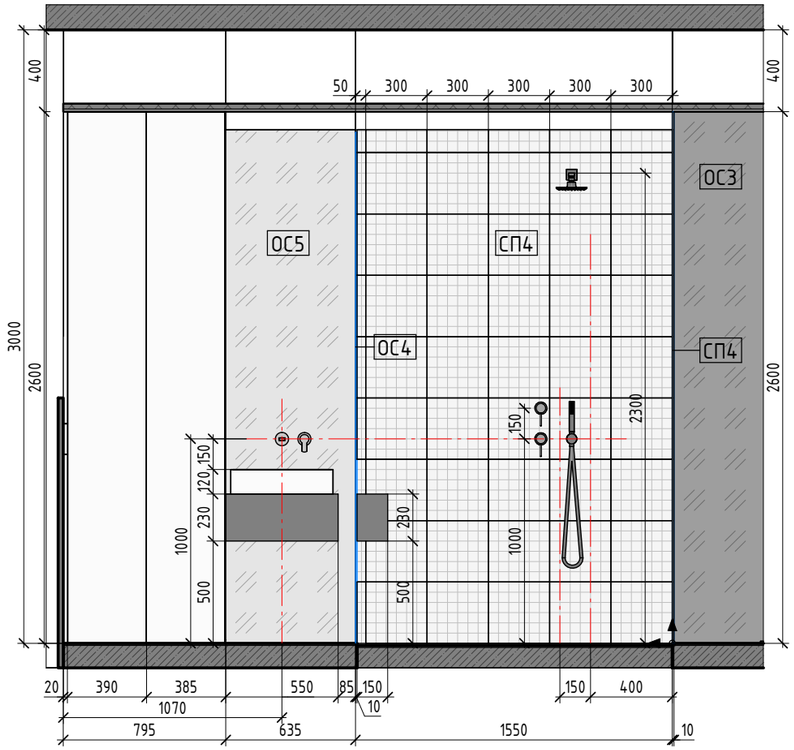

Условные обозначения:

ОС1 – Марка отделки стен

– МДФ, цвет графитовый

– Стекло тоннированное

– Зеркало тонированное

– Зеркало

– Плитка-мозайка

– Открывание фасадов

Примечание:

1. Колличесво материалов посчитано в "Спецификации отделки", см. лист 26.
2. Смотреть совместно с планами мебели (л.9) и отделки (л.26)
3. Все развертки по мебели разработаны условно и являются заданием для подрядчиков.

РАЗВЕРТКИ пом. № 4, Санузел

№ проекта	Раздел	Стадия	Лист	Листов
	АИ	РП	32	